


A generous plot, with a clear arrival

Site proposal | 1:300 on A3 at 100% | South-facing rear garden assumed

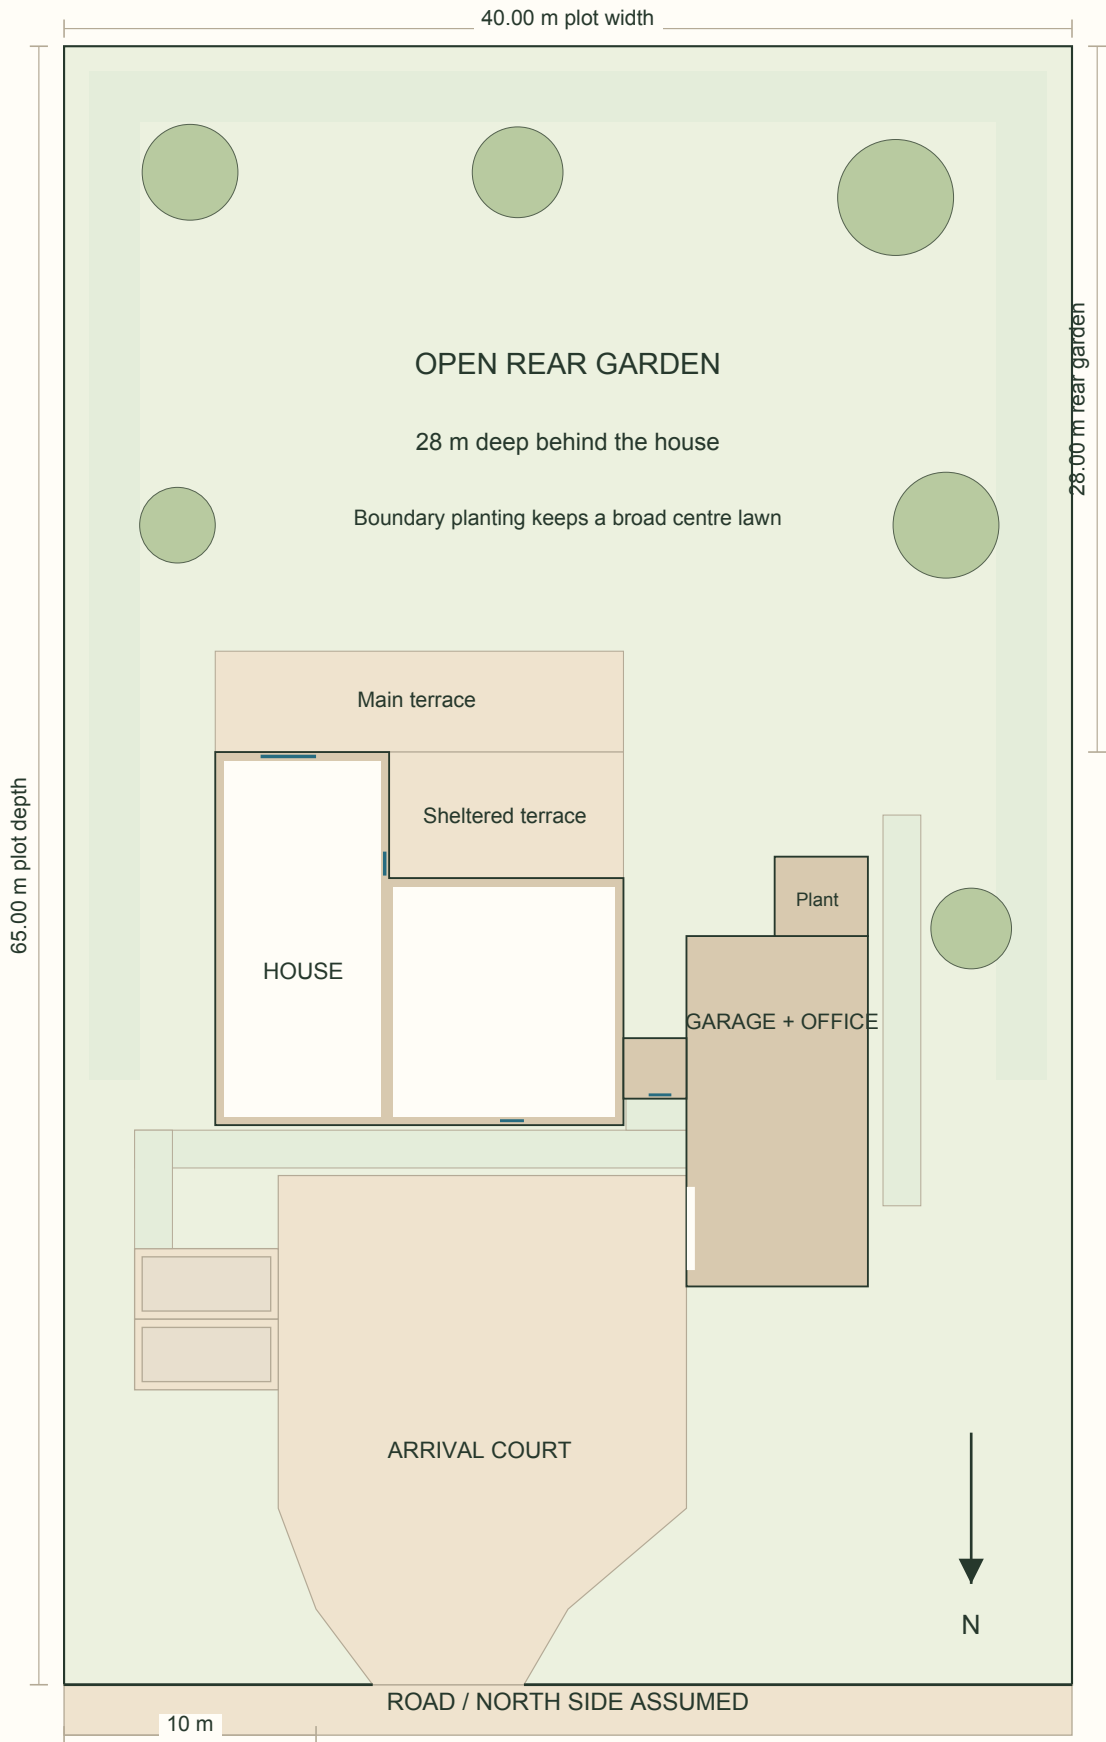

A working plot, not a real-site claim

A 40 x 65 m plot provides 2,600 m² of land. The house starts 28 m from the rear boundary. The garage stays beside the house and forward of it, with the enclosed ground-floor link retained.

Room for the garden

The full-width rear strip is 1,120 m² before terrace and planting. A 4 m-deep main terrace and the sheltered recess beside dining connect to the garden. The centre remains open for lawn, play and distant views. Trees are planting zones, not selected species.

Arrival that has a purpose


One 6 m-wide road entrance opens into a broad turning court. Two visitor bays sit to the left. A 1.5 m walking path leads to the front door; the link door serves everyday arrivals and shopping. The vehicle door faces the house.

Orientation and site checks

The road is assumed to be north of the house, with the rear garden to the south. Sun, slope, drainage, boundary conditions and road sightlines need a real site. No neighbouring buildings or protected trees are assumed.

Drive in, park, and leave facing forward

Arrival study | 1:150 on A3 at 100% | Illustrative car envelope: 5.10 x 2.15 m

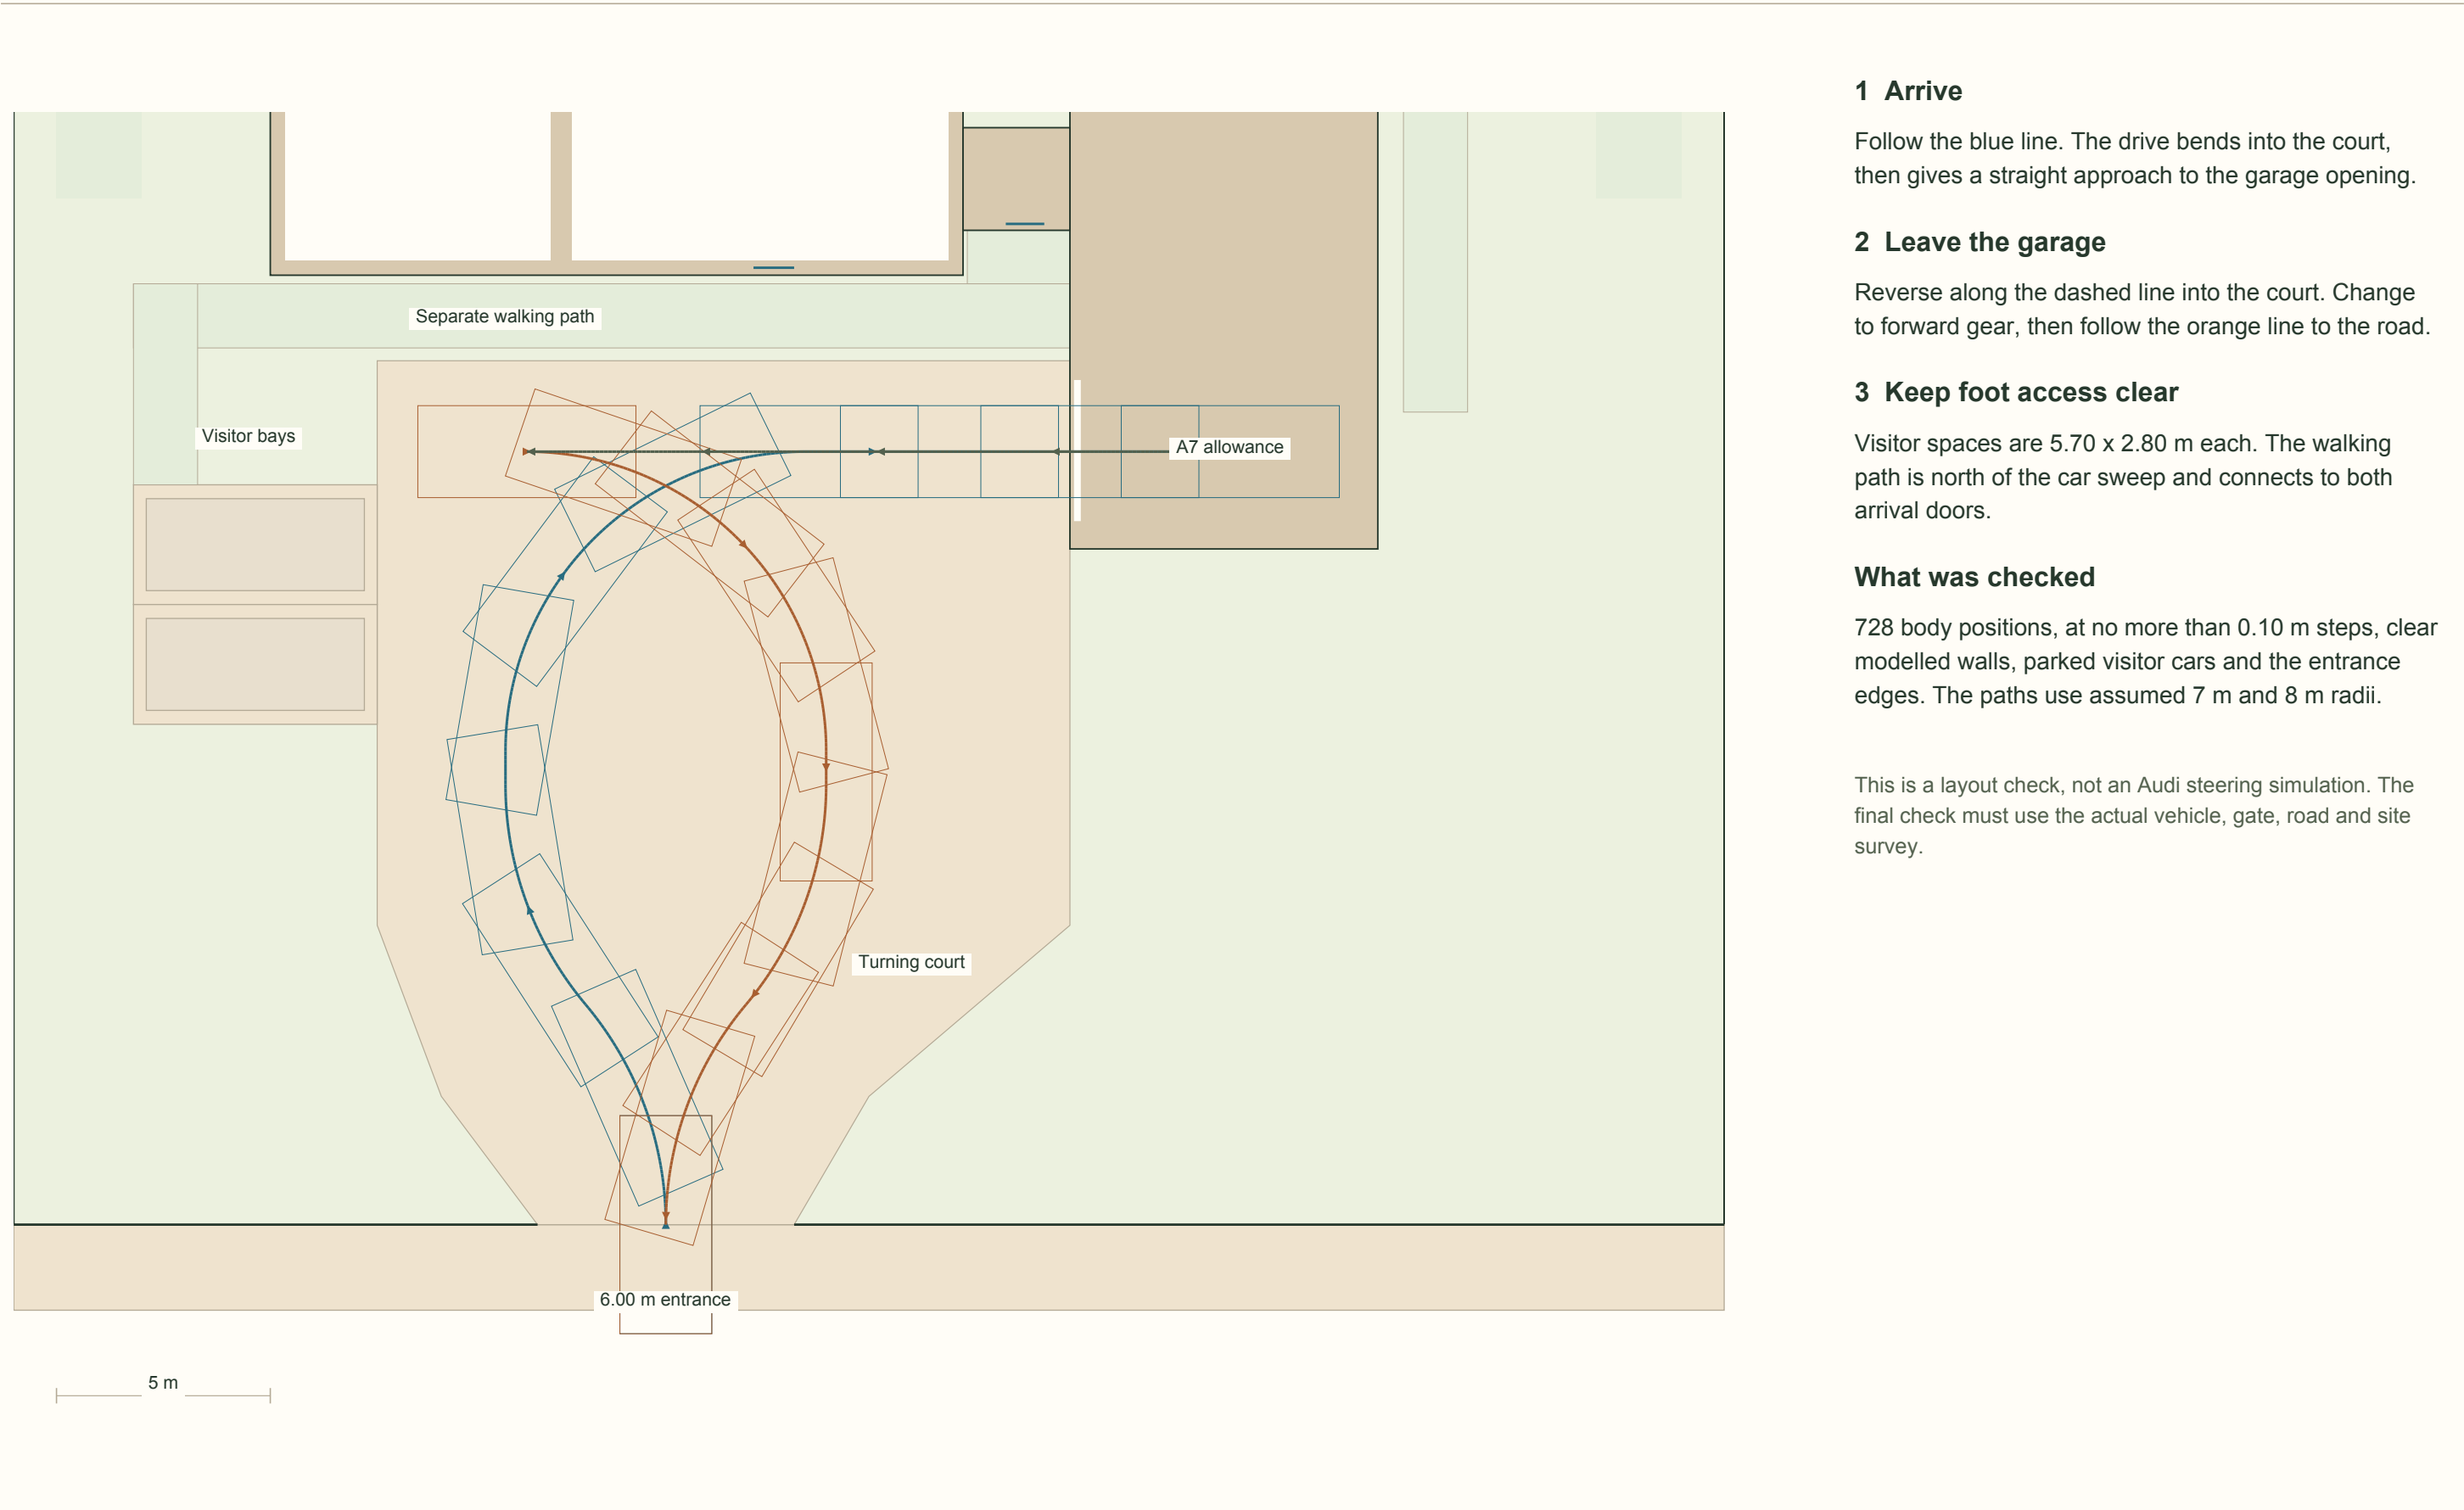

1 Arrive

Follow the blue line. The drive bends into the court, then gives a straight approach to the garage opening.

2 Leave the garage

Reverse along the dashed line into the court. Change to forward gear, then follow the orange line to the road.

3 Keep foot access clear

Visitor spaces are 5.70 x 2.80 m each. The walking path is north of the car sweep and connects to both arrival doors.


What was checked

728 body positions, at no more than 0.10 m steps, clear modelled walls, parked visitor cars and the entrance edges. The paths use assumed 7 m and 8 m radii.

This is a layout check, not an Audi steering simulation. The final check must use the actual vehicle, gate, road and site survey.


Ground floor: daily life and two arrivals

Main house | 1:100 on A3 at 100% | Default: short pantry divider and open passage

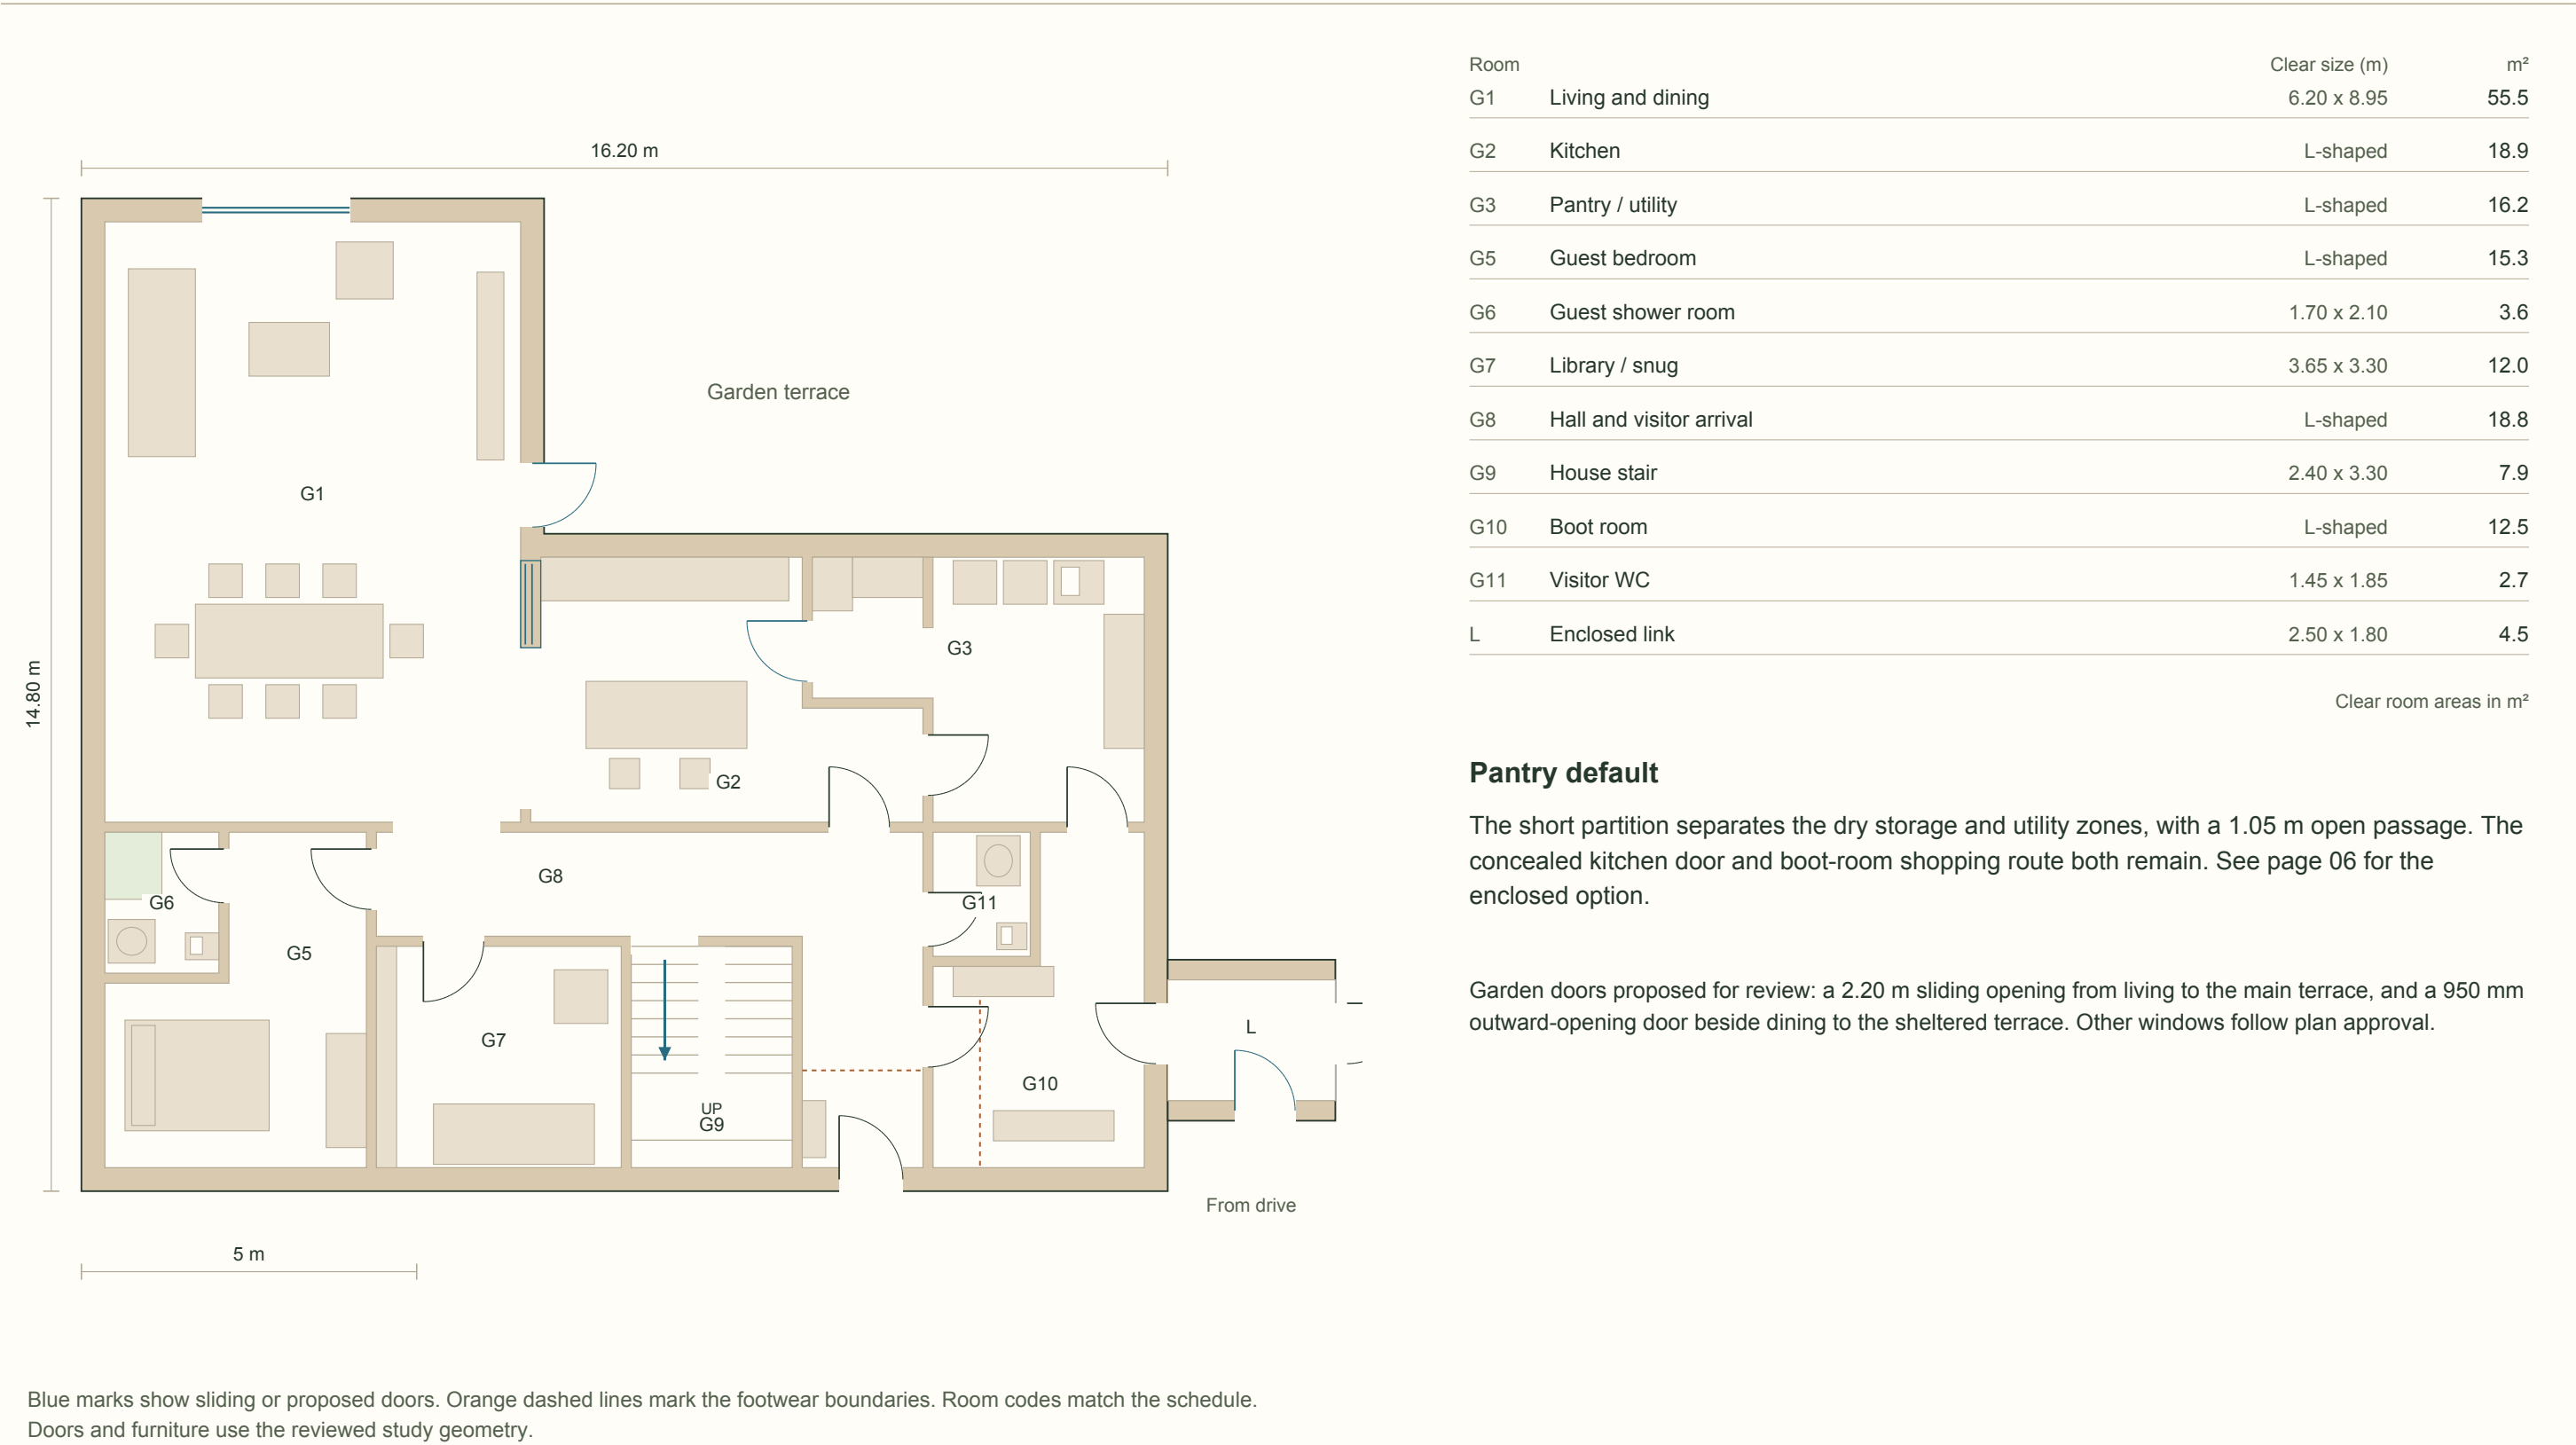

First floor: family rooms and a private suite

Main house | 1:100 on A3 at 100% | Approved separate suite gallery

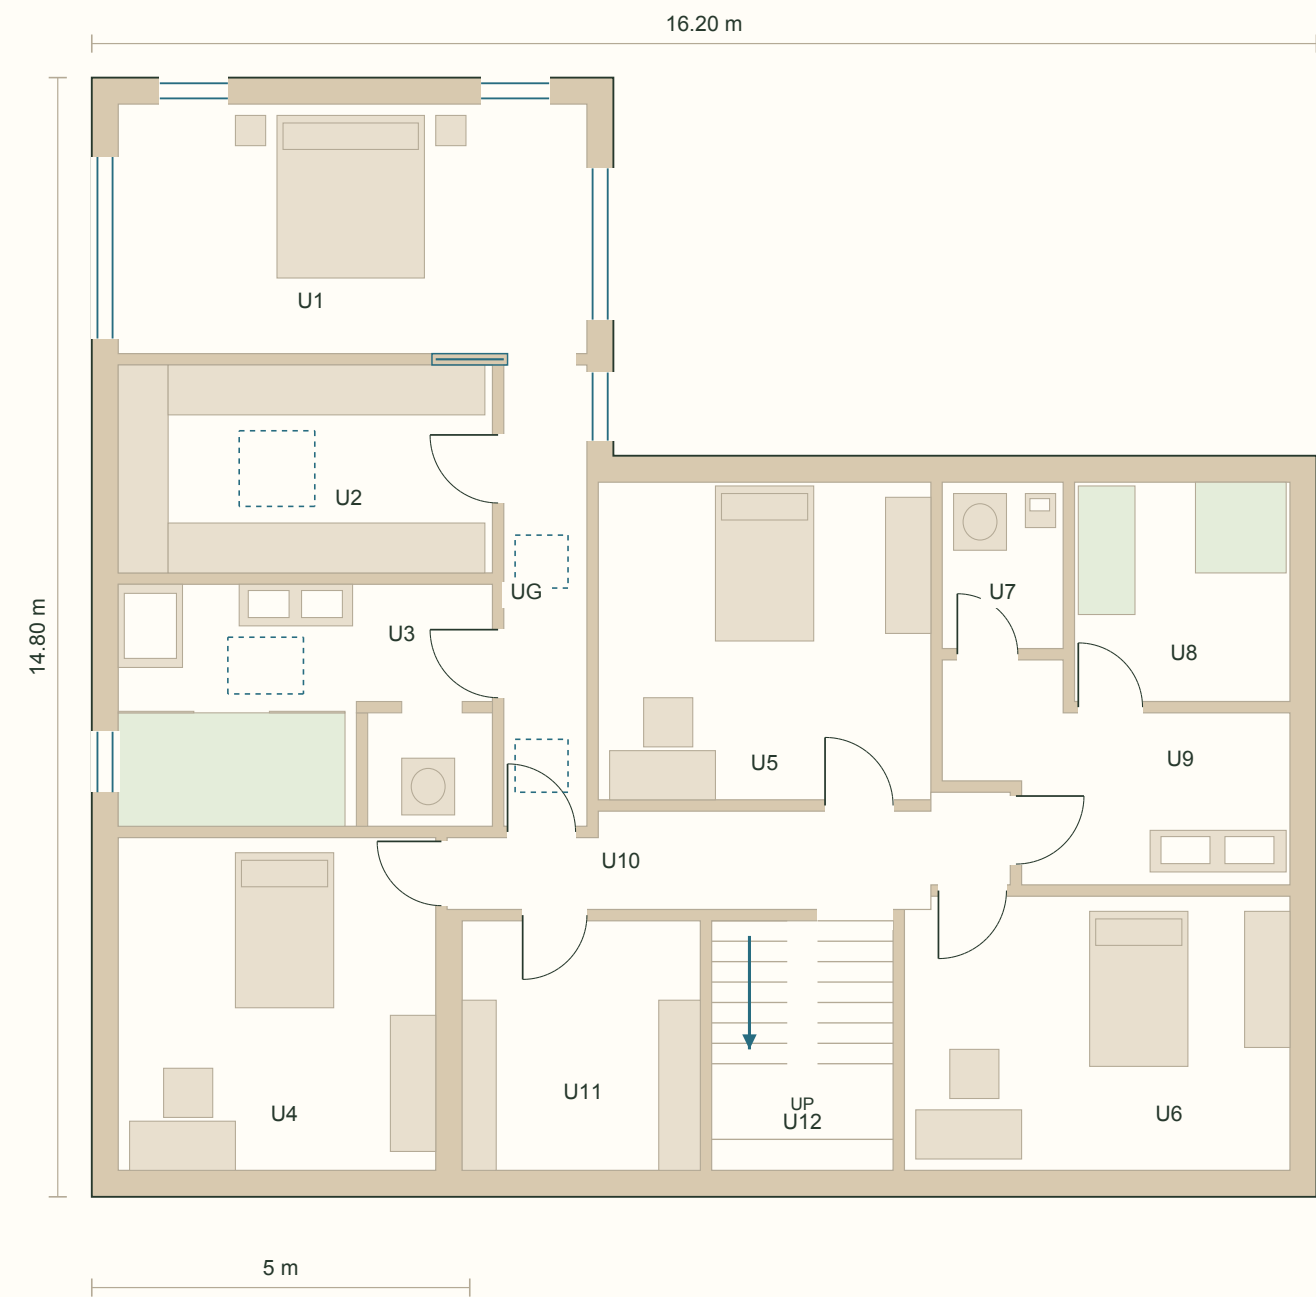

Room	Clear size (m)	m²
U1Parents' bedroom	6.20 x 3.30	20.5
U2Dressing room	4.95 x 2.75	13.6
U3Parents' ensuite	4.95 x 3.20	15.8
UGPrivate suite gallery	1.10 x 6.10	6.7
U4Child 1	4.20 x 4.40	18.5
U5Child 2	4.40 x 4.20	18.5
U6Child 3	5.10 x 3.62	18.5
U7Family WC	1.60 x 2.20	3.5
U8Bath and separate shower	2.85 x 2.90	8.3
U9Shared dry basin area	L-shaped	10.1
U10Landing	L-shaped	8.9
U11Linen / household storage	3.15 x 3.30	10.4
U12House stair	2.40 x 3.30	7.9

Clear room areas in m²

Separate suite access

Landing > private gallery > separate bedroom, dressing and bathroom doors. The gallery stops at the rectangular bedroom. Dressing is not a through-route.


Equal child-room provision

The three rooms are each about 18.5 m². Each keeps the same bed-frame, desk and wardrobe allowance. The family WC, wet room and dry basins can be used separately.

Both floors keep the same stair. Blue double lines mark suite windows; dashed boxes mark rooflight zones. The bedroom garden window is 2.00 m wide; the gallery window is 0.90 m wide.

Garage, gym and office remain usable together


Garage ground floor and office first floor | 1:100 on A3 at 100% | No upper bridge to the house

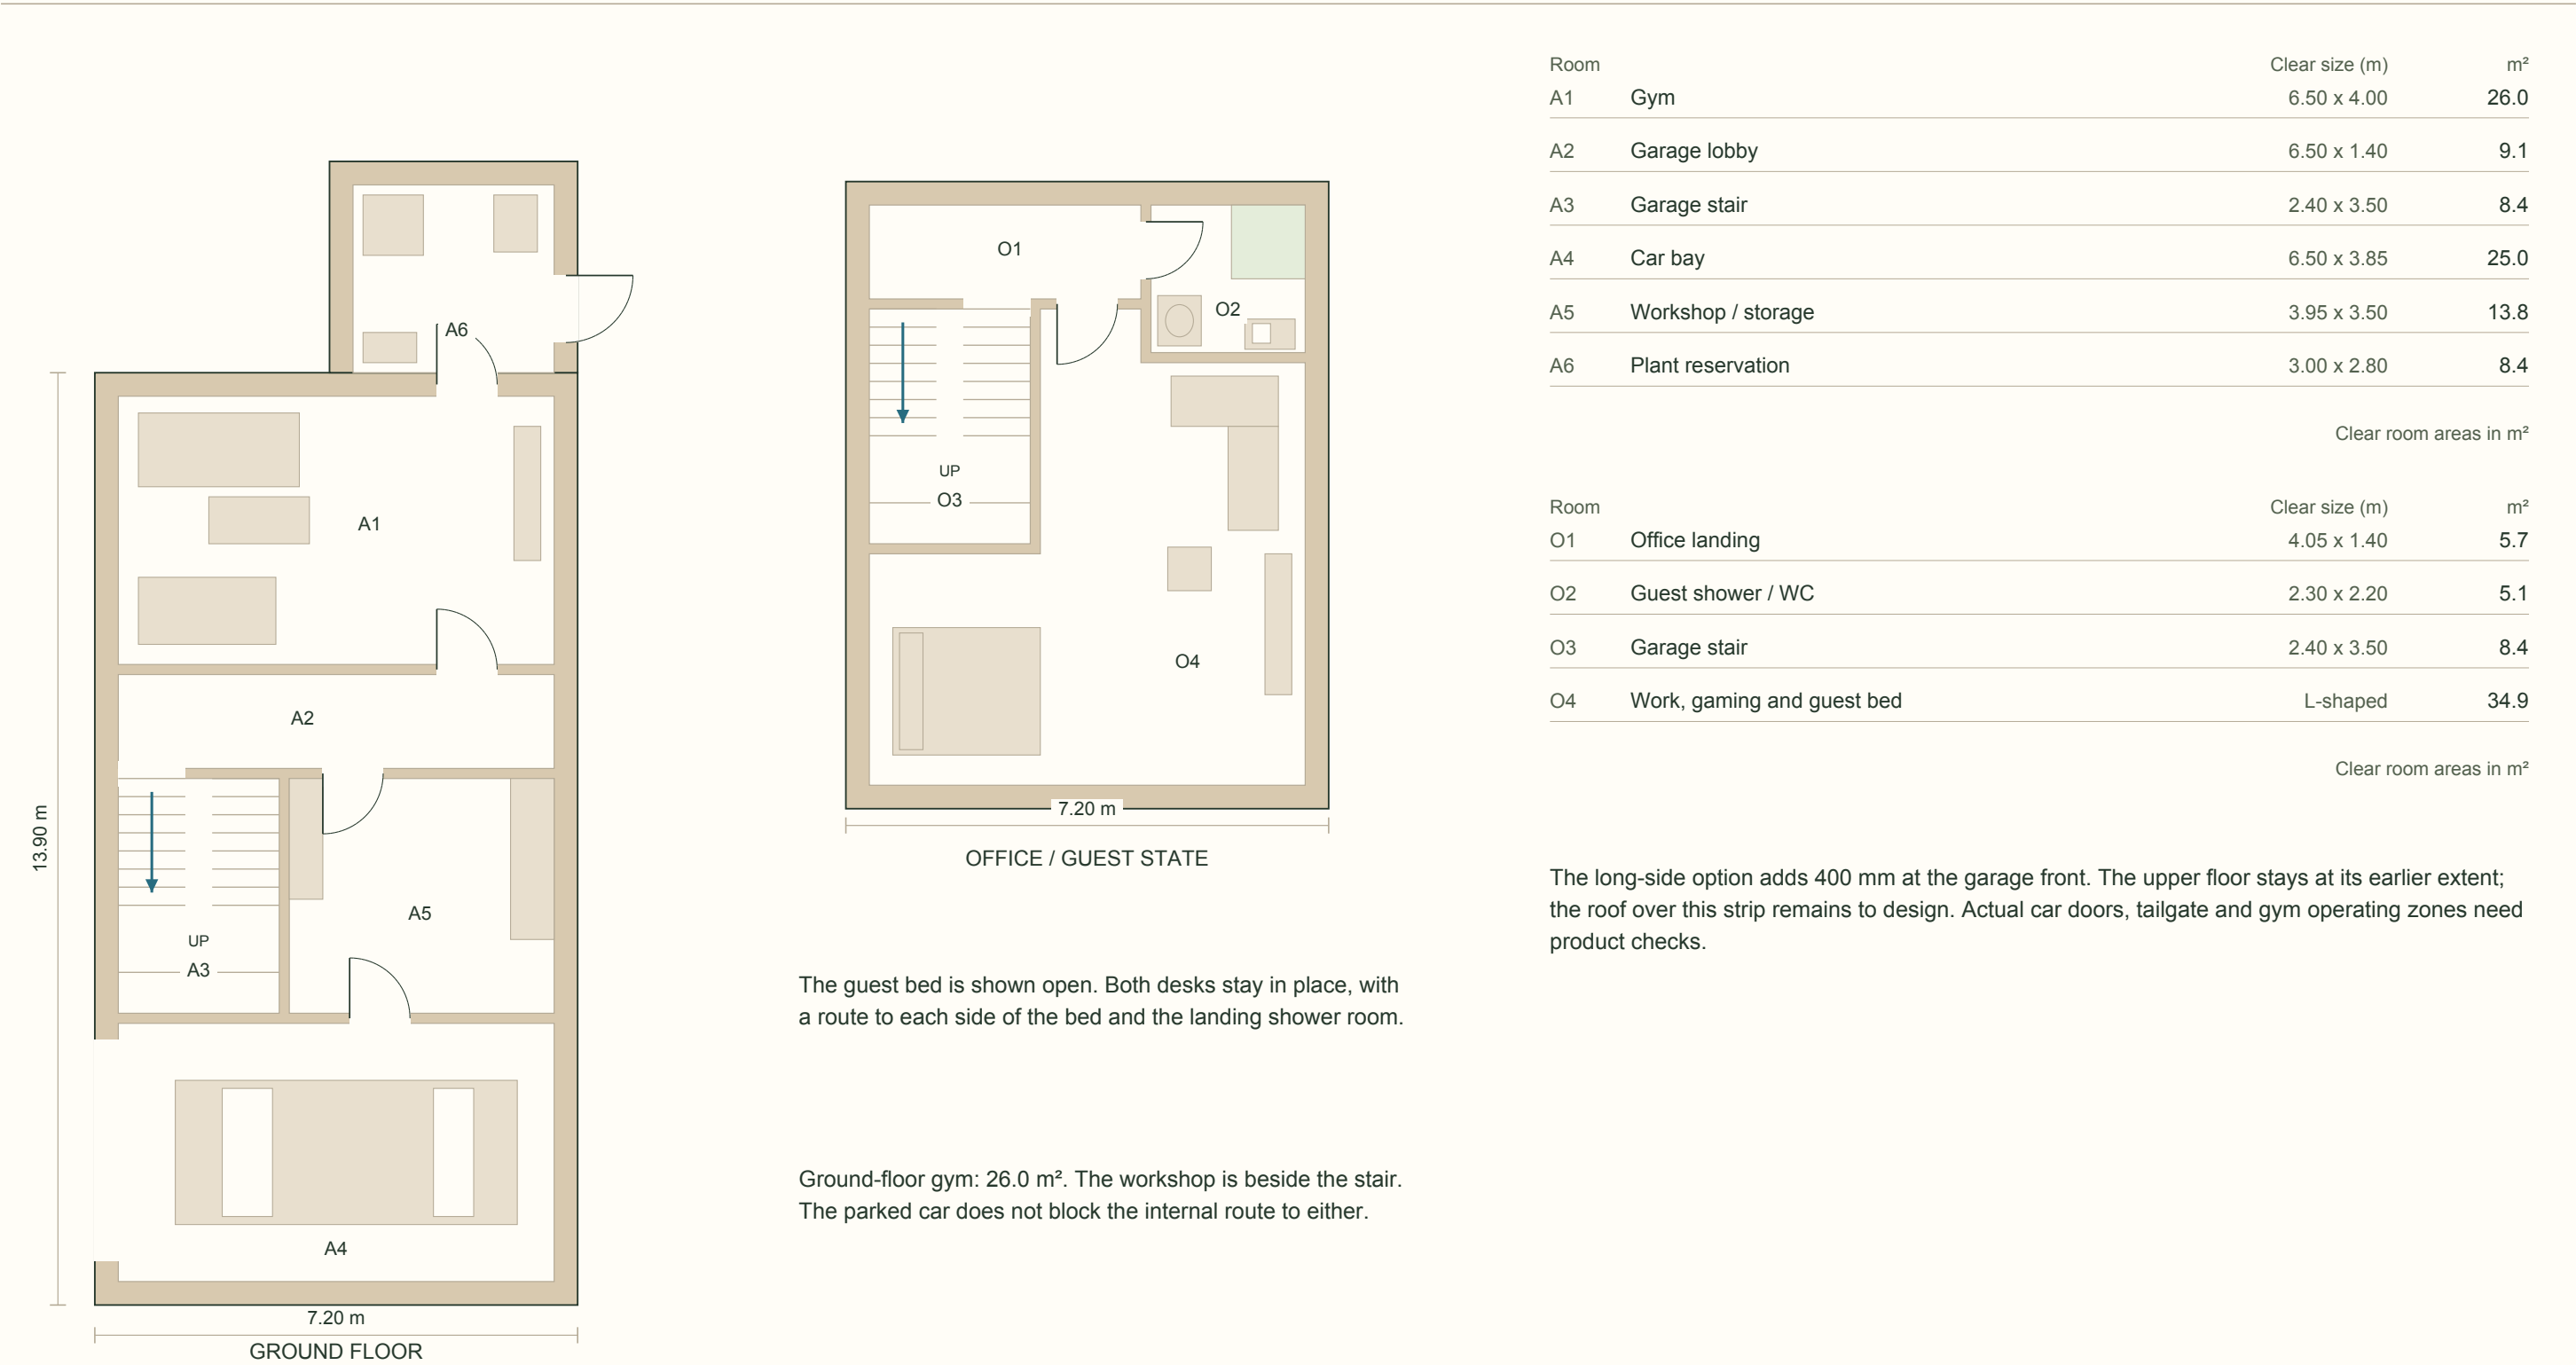

Pantry choice: connected by default, enclosed if preferred

Default kitchen and utility 1:50 | Enclosed pantry detail 1:50 | Both options keep direct kitchen access

DEFAULT / SHORT DIVIDER

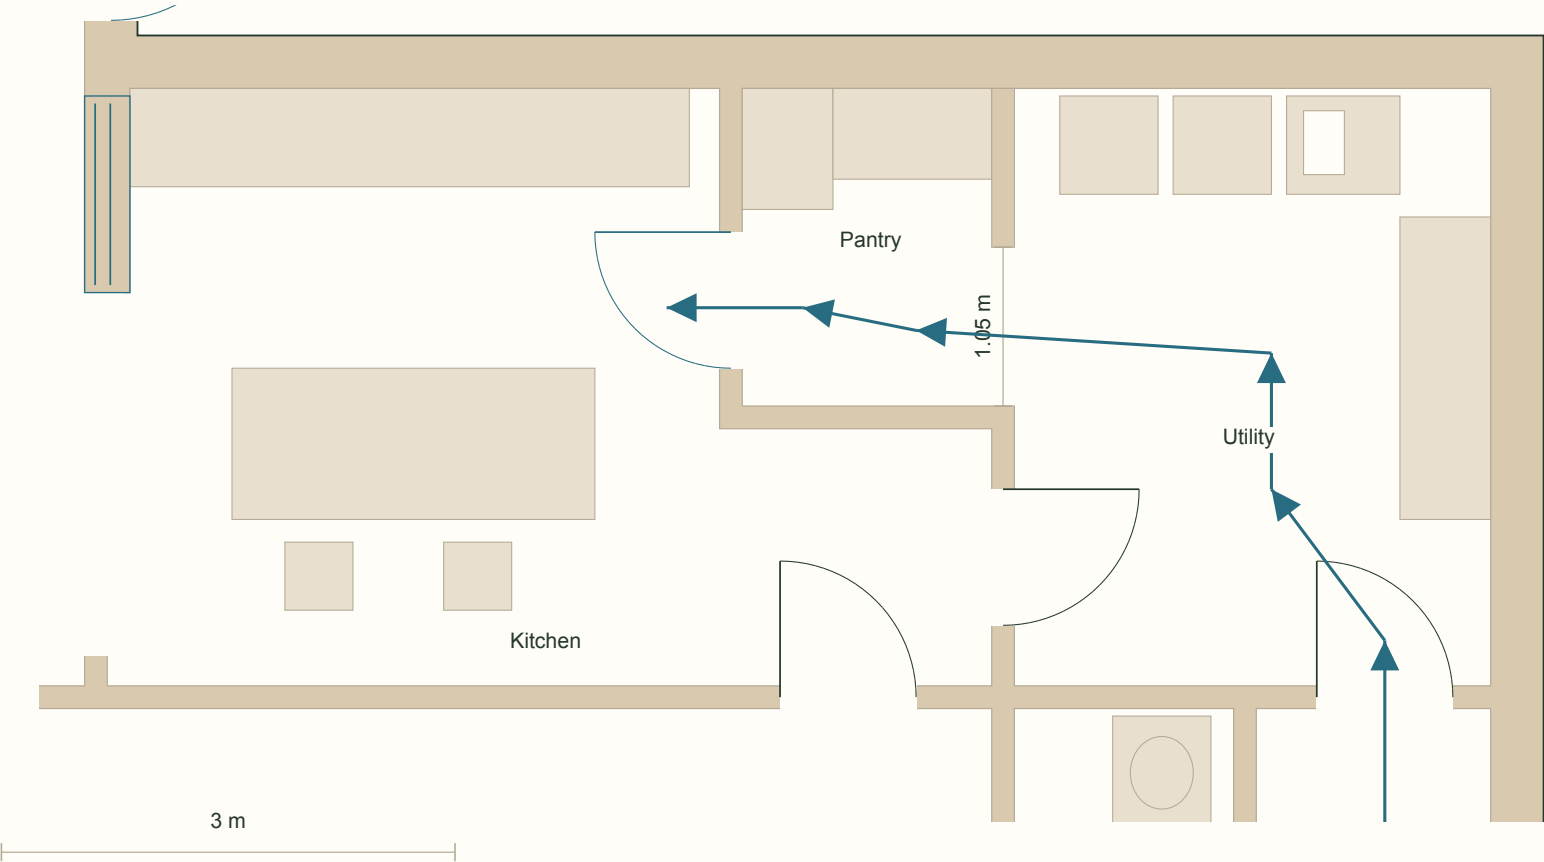


Default: two zones with an open connection

A full-height, 150 mm-thick divider projects 1.05 m from the rear wall. A 1.05 m passage connects pantry and utility. Dry storage stops clear of the partition. The shopping route runs directly from boot room to utility to pantry.

The kitchen door has a cabinet-style face and opens into the kitchen. The 2.40 m kitchen / dining opening can close with sliding panels. The drawing shows the panels retracted.

OPTION / ENCLOSED PANTRY

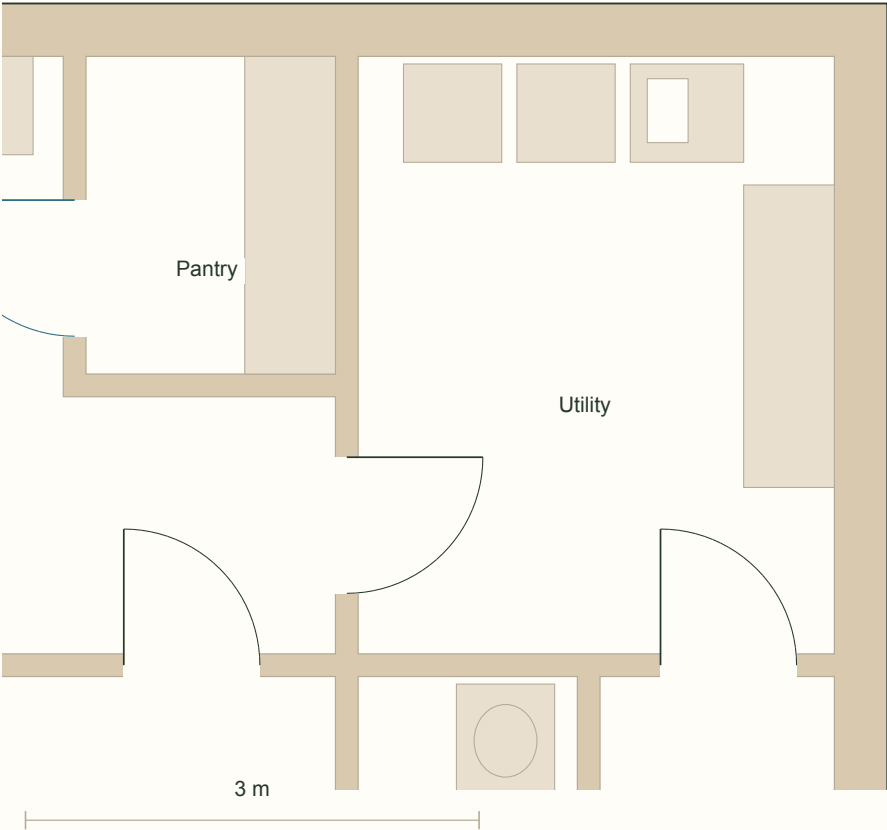



Enclosed option retained

This restores the full dividing wall and the earlier pantry shelving. The pantry opens directly from the kitchen; the utility keeps its kitchen and boot-room doors.

Trade-off: shopping reaches the pantry through the kitchen. There is no connecting pantry / utility door in this retained option.

Parents suite: separate access and garden light

Suite 1:75 | Bathroom detail 1:40 | Same external suite boundary

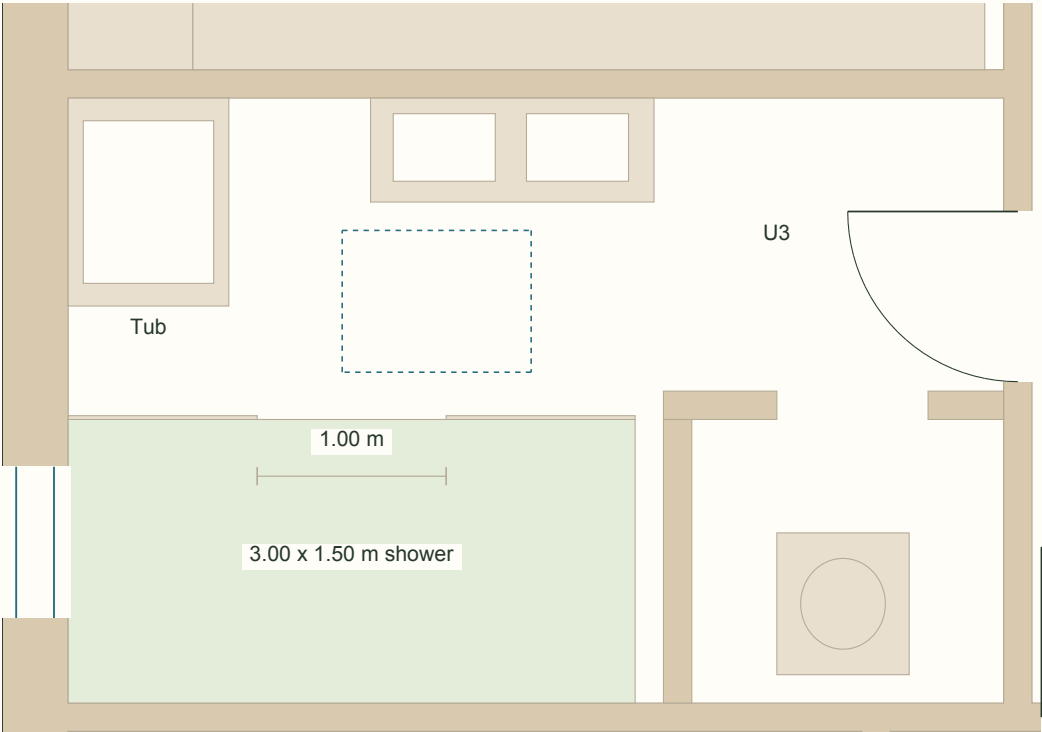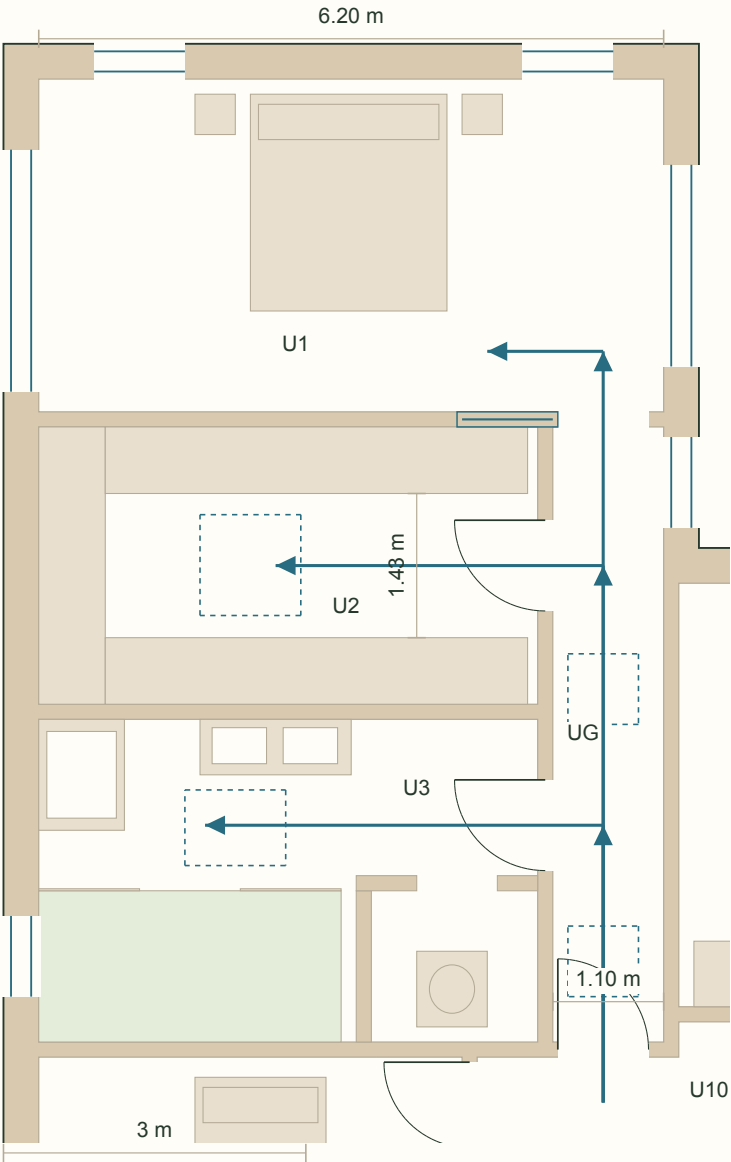

Bathroom: 4.95 x 3.20 m. Tub allowance: 0.85 x 1.10 m. Vanity: 1.50 x 0.55 m. Filled weight, entry, waterproofing and drainage remain product and construction checks.

The window widths and rooflight zones carry the approved daylight direction. Window sill heights, roof slopes, trimmers and light wells remain provisional.

Bathroom features retained

Two basins, compact soaking tub, screened WC and a 3.00 x 1.50 m shower. Two fixed screens retain a 1.00 m central entry.

Three separate room doors

All openings are 900 mm. The bedroom has a wall pocket; dressing and bathroom doors open into their rooms. Hardware remains provisional.


Natural light

A 2.00 m bedroom garden window and 0.90 m gallery window. Four dashed rooflight zones serve dressing, bathroom and gallery. Roof openings and light wells need design.

Dressing: 4.95 x 2.75 m with 660 mm-deep wardrobes on three sides. Clear aisle: 1.43 m; one 0.50 m open drawer leaves 0.93 m. Bedroom: 6.20 x 3.30 m with 1.00 m at the bed foot.


Family bathroom and stair assumptions

Family bathroom 1:50 | Stair diagram 1:50 | Heights remain design assumptions

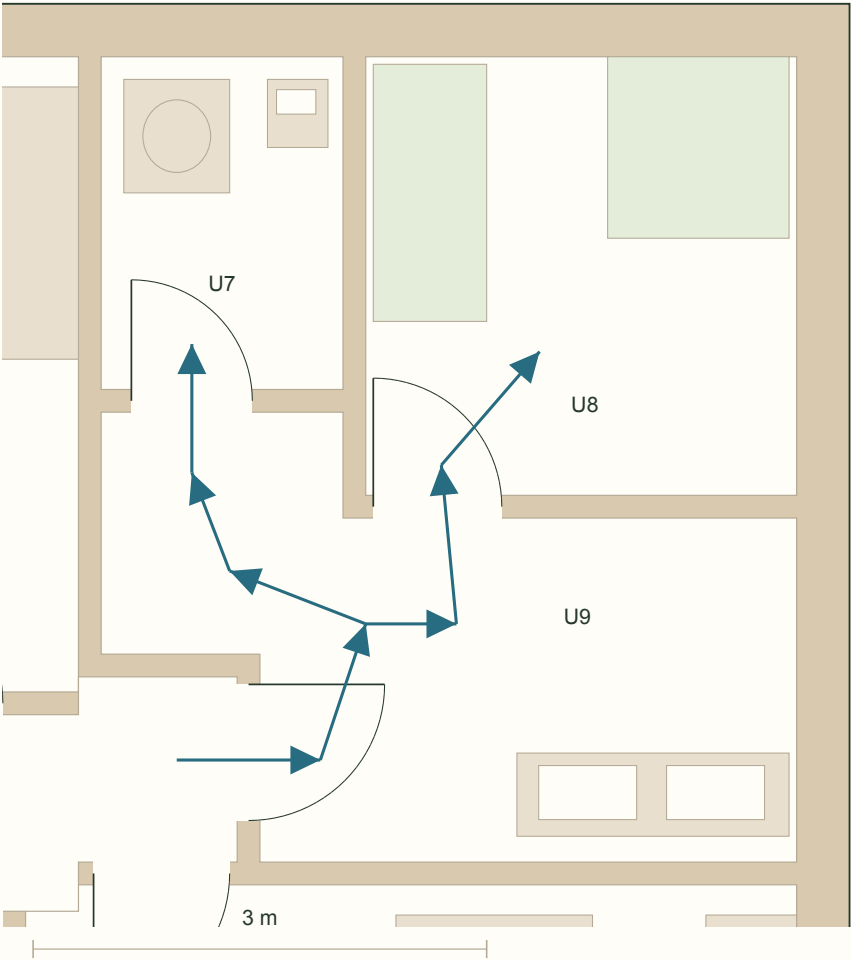

Three separate activities

Separate WC, separate bath / shower room, and a shared dry basin area. The WC also has its own hand basin. Changing space stays inside the wet room.

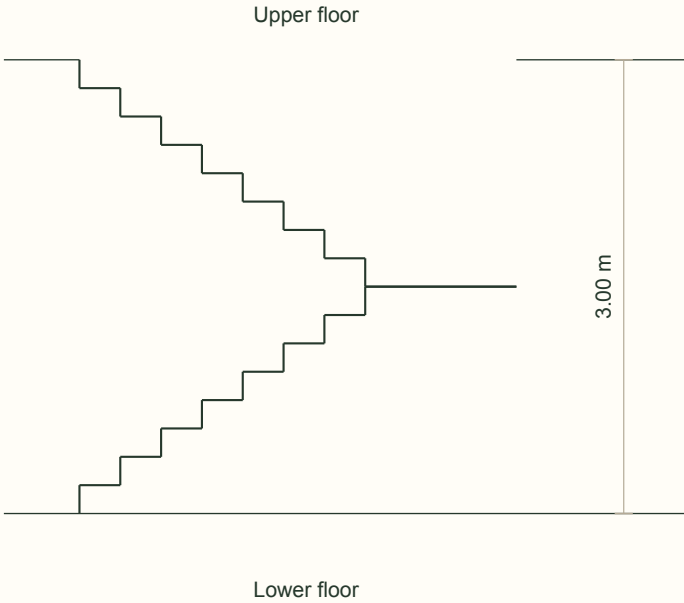

Both stairs

16 rises of 187.5 mm. Going 270 mm. Two 1.00 m clear flights and a 1.00 m half landing.

Section assumptions

Floor to floor: 3.00 m. Floor zone: 300 mm. Clear ceiling: 2.70 m. A full opening above both flights is reserved.

The drawing explains the assumed stair rise and run. Final headroom needs the roof, beams, landings and floor openings to be designed together. It is not a verified building-regulation section.

The next design stage will establish roof shapes, windows and structure, then build the approved plan in 3D. Detailed services routes must also be reworked for two storeys.

Approved suite direction for the next 3D model

Area summary, retained brief and decisions | L01.1 suite revision, 8 October 2026

Proposed plot	2,600 m²
Rear garden strip before terrace / planting	1,120 m²
House external floor area, both floors	386.52 m²
Garage, gym, workshop and stair footprint	100.08 m²
Office external floor area	67.32 m²
Plant and enclosed link footprints	17.66 m²
Total building footprint	311.00 m²
Total external floor envelopes	571.58 m²

External areas include walls and stairs. Room schedules use clear room polygons, so the totals differ. These are study measurements, not certified floor areas. The garden strip is not a net lawn-area claim.

Full plans and room details share the same revised geometry. Suite routes have new sampled footprint checks; older layout checks apply to the original source only. Later kitchen / living render studies remain separate inputs for the next coordinated model.

Approved suite revision

Keep the rectangular parents bedroom, separate gallery, enlarged U-shaped dressing room and retained bathroom fittings. Add the two garden windows and four rooflight zones shown on page 07.

Carry into the next stage

Warm stone, timber and ivory; no grey finish palette. Retain footwear boundaries, separate family bathroom uses, landscape views, wet underfloor heating, active cooling and solar contribution.

Resolve after floor-plan approval

Roof and window design, stair headroom, structure above the garage opening, bathroom and plant routes, ventilation, and a real-site car-turning check. The former courtyard vault and glazed garden-room roof are not resolved by this two-storey plan.

Next: establish the vertical design and update the furnished 3D model. Coordinate the later selected kitchen and living studies with this suite. The existing courtyard model stays available for comparison.