


A generous plot, with a clear arrival

Site proposal | 1:300 on A3 at 100% | South-facing rear garden assumed

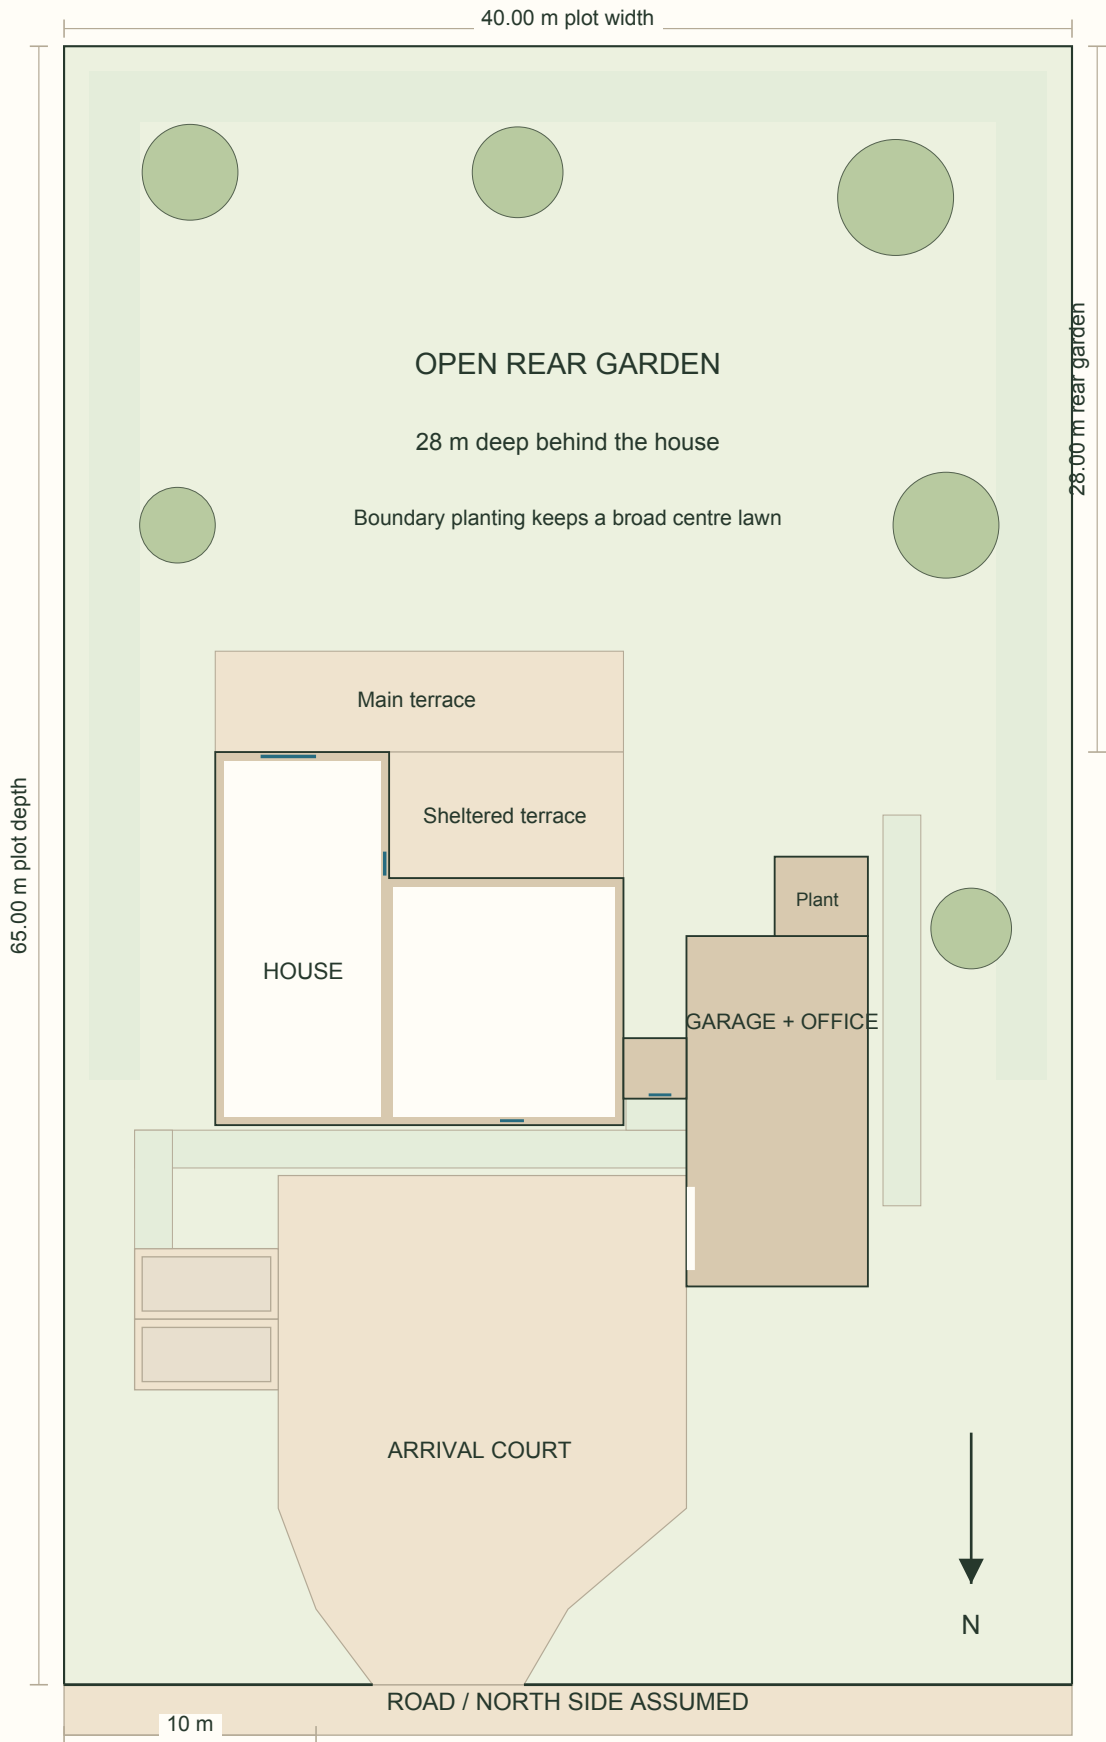

A working plot, not a real-site claim

A 40 x 65 m plot provides 2,600 m² of land. The house starts 28 m from the rear boundary. The garage stays beside the house and forward of it, with the enclosed ground-floor link retained.

Room for the garden

The full-width rear strip is 1,120 m² before terrace and planting. A 4 m-deep main terrace and the sheltered recess beside dining connect to the garden. The centre remains open for lawn, play and distant views. Trees are planting zones, not selected species.

Arrival that has a purpose


One 6 m-wide road entrance opens into a broad turning court. Two visitor bays sit to the left. A 1.5 m walking path leads to the front door; the link door serves everyday arrivals and shopping. The vehicle door faces the house.

Orientation and site checks

The road is assumed to be north of the house, with the rear garden to the south. Sun, slope, drainage, boundary conditions and road sightlines need a real site. No neighbouring buildings or protected trees are assumed.


Drive in, park, and leave facing forward

Arrival study | 1:150 on A3 at 100% | Illustrative car envelope: 5.10 x 2.15 m

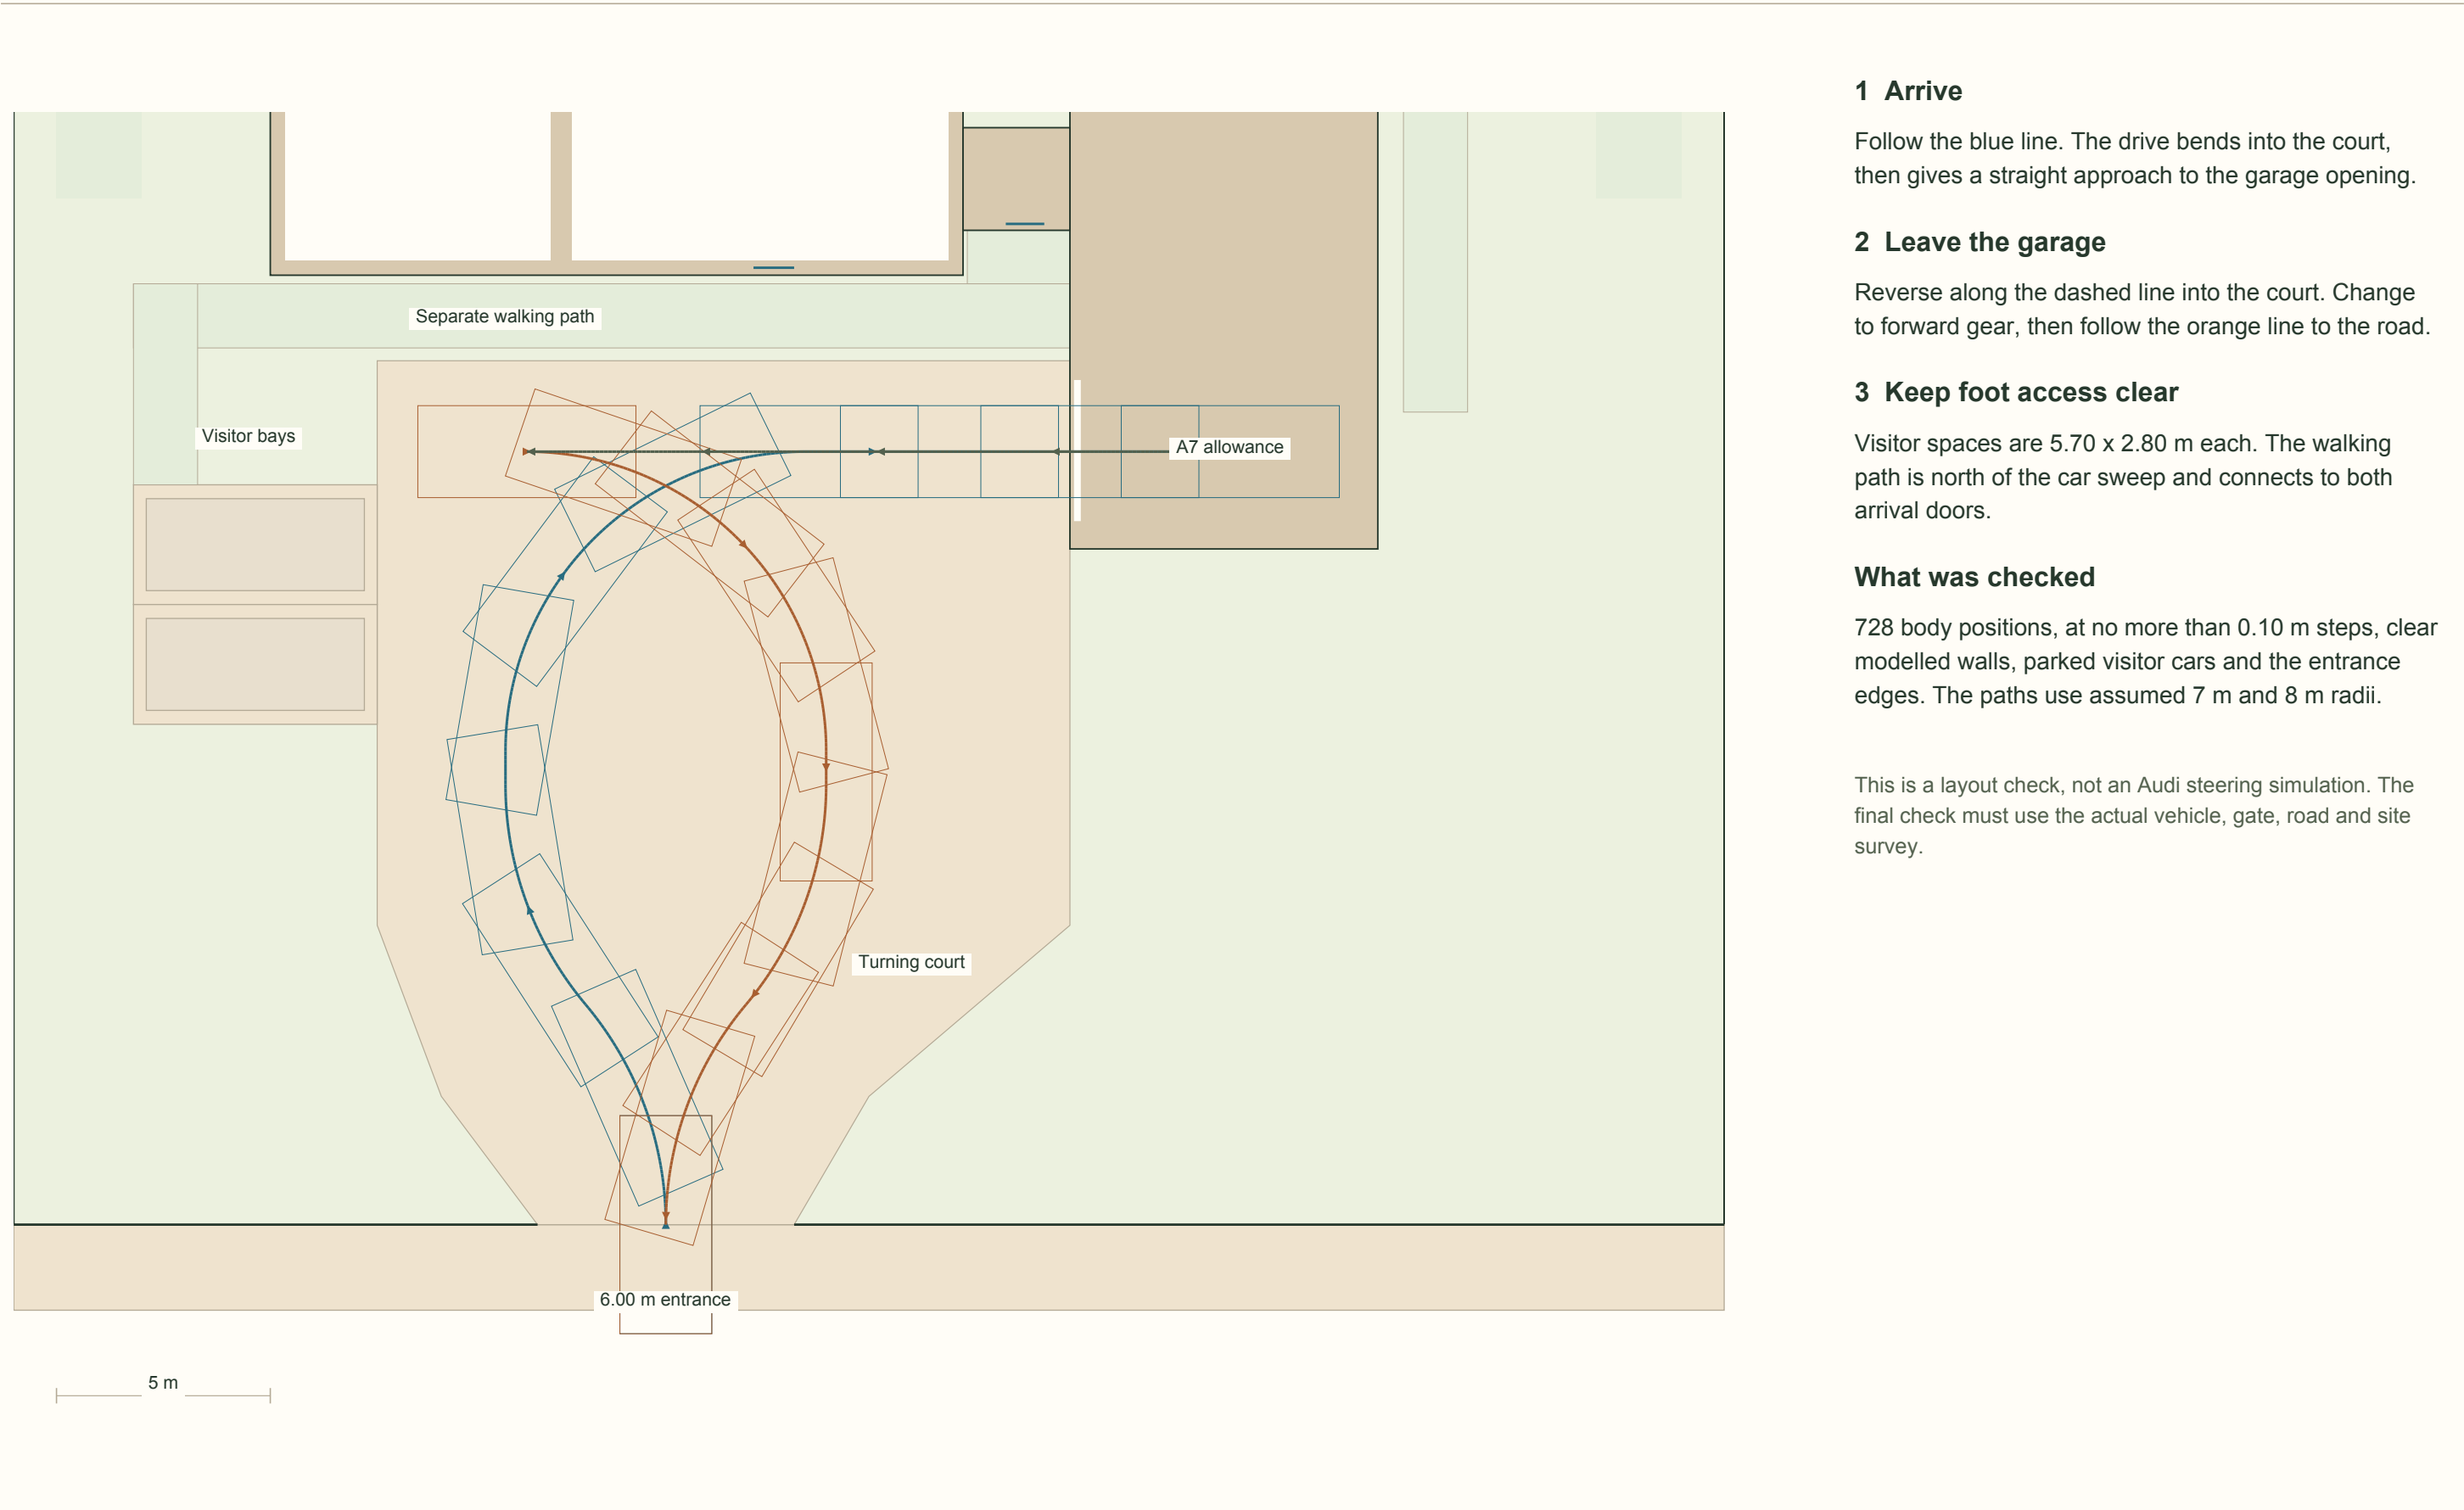

Ground floor: daily life and two arrivals

Main house | 1:100 on A3 at 100% | Default: short pantry divider and open passage

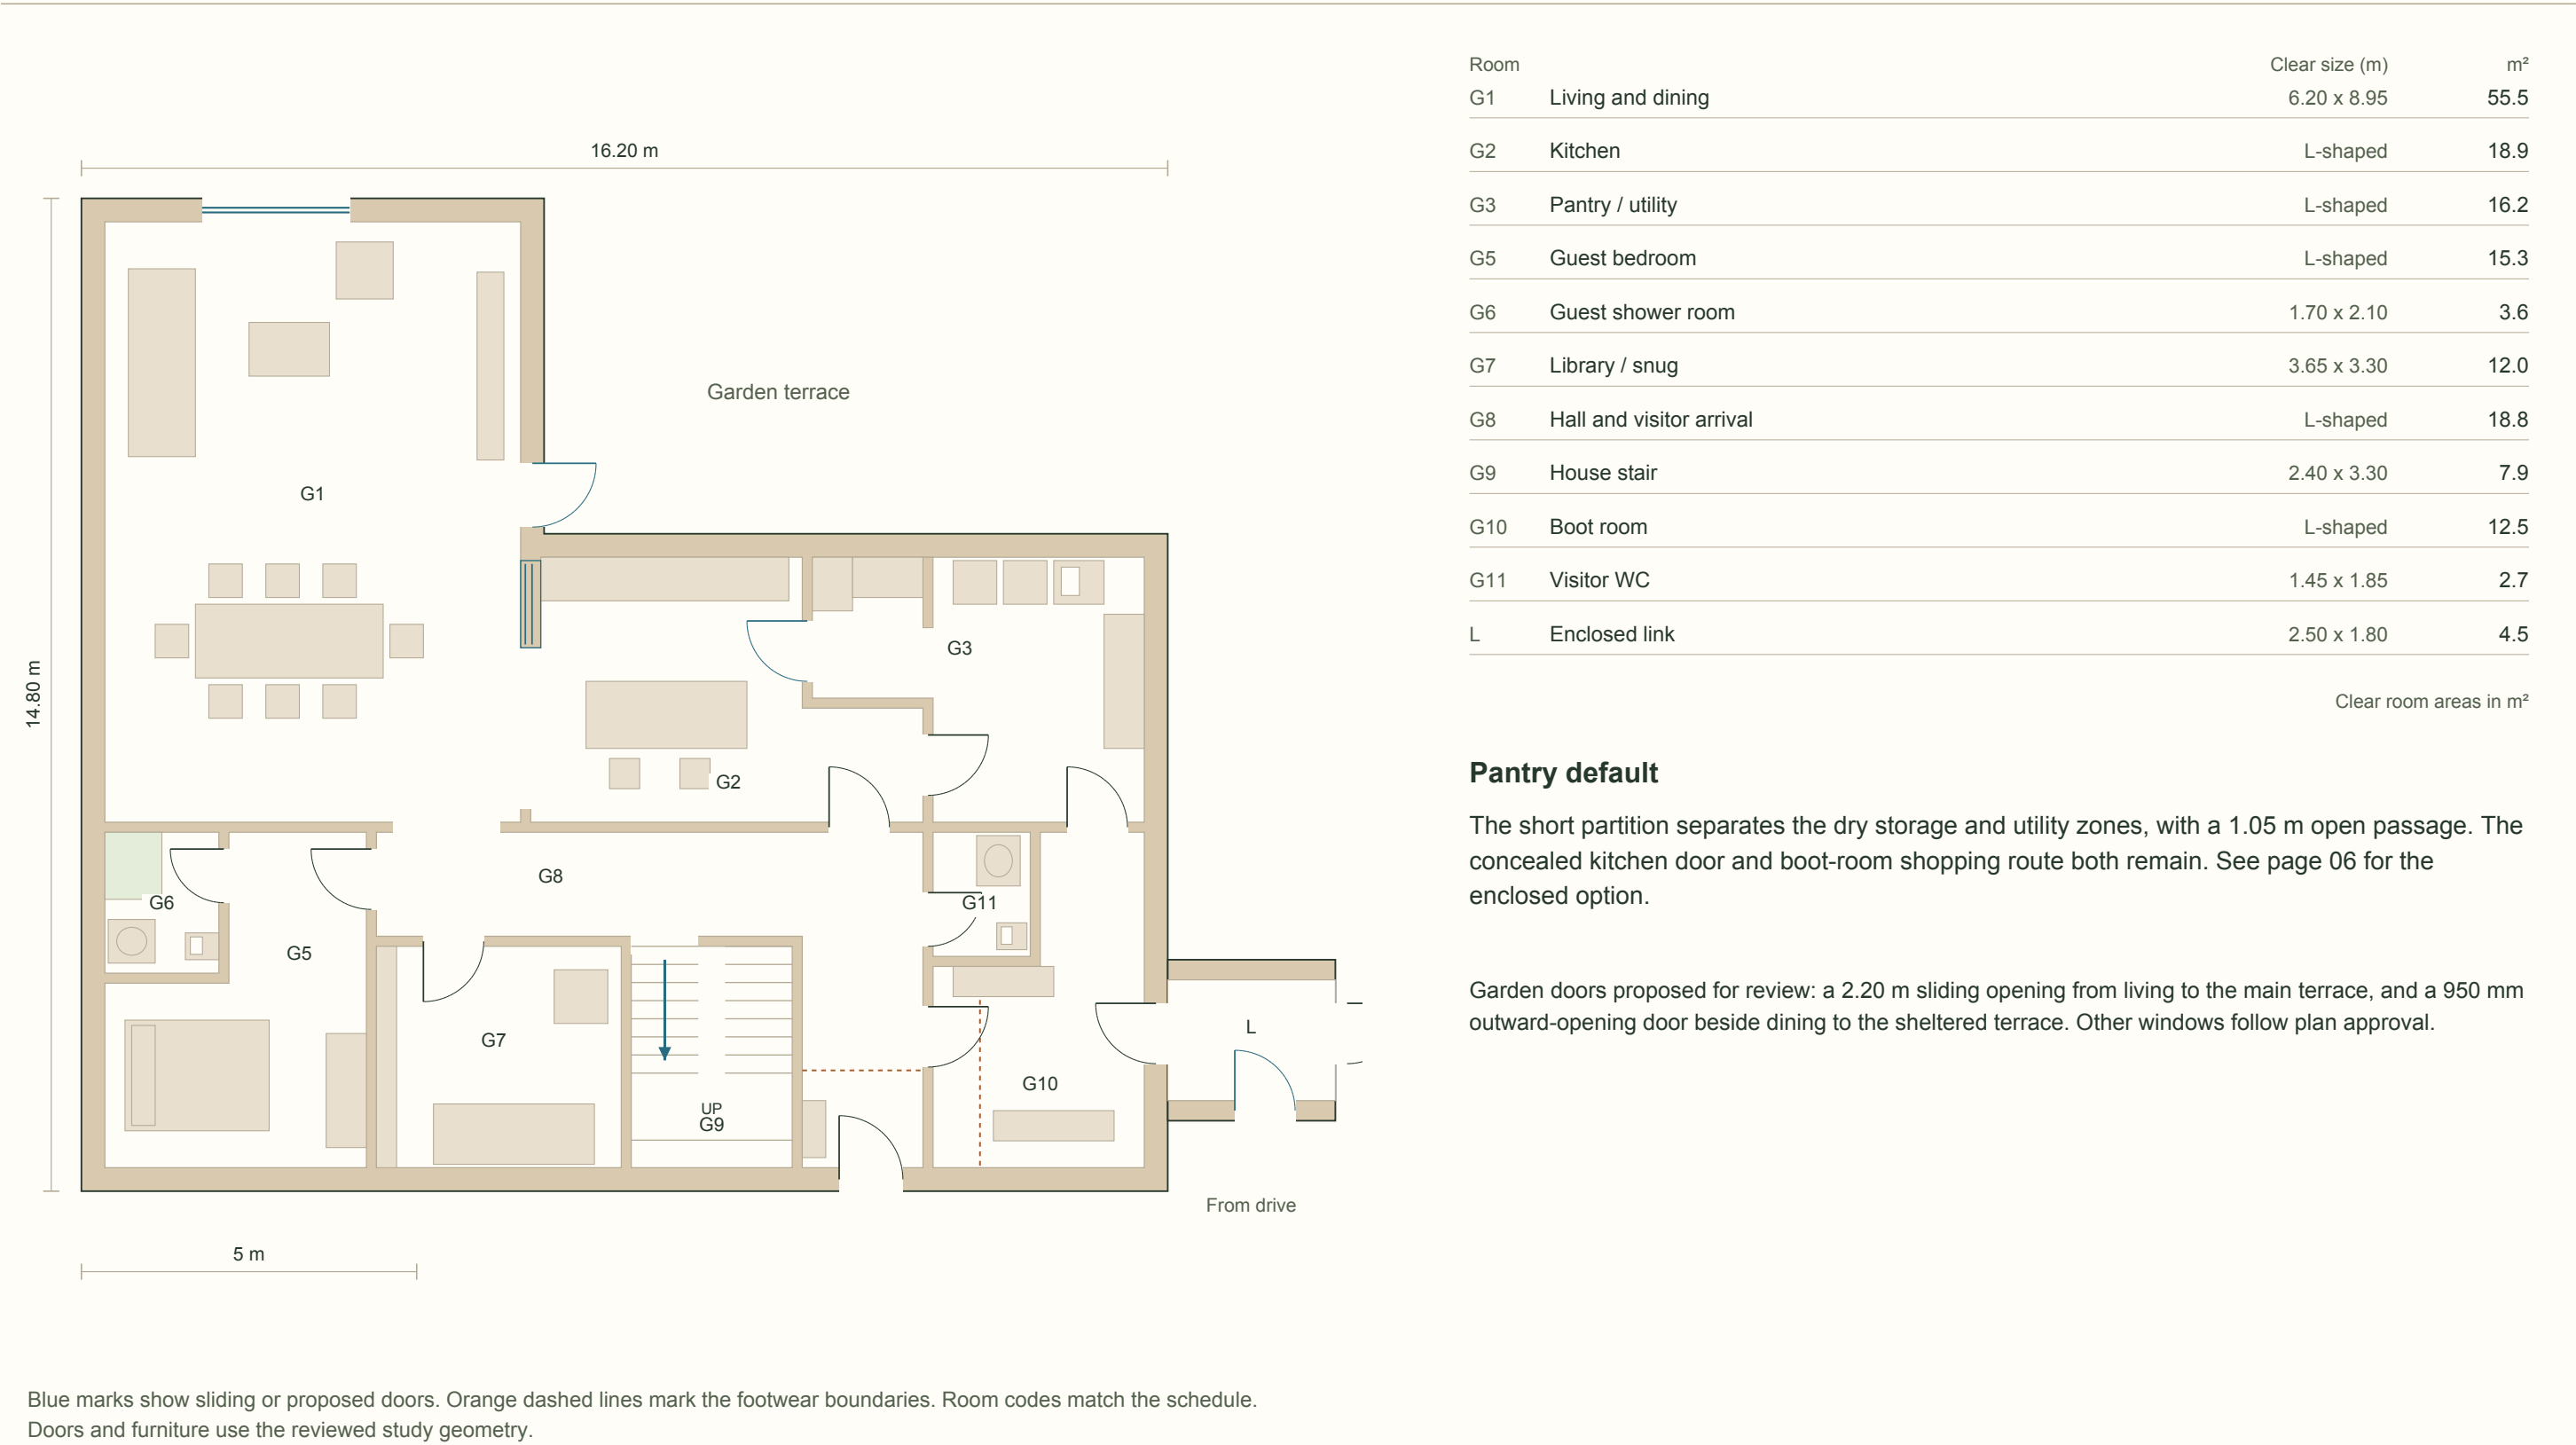


First floor: family rooms and a private suite

Main house | 1:100 on A3 at 100% | Approved room boundaries retained



Garage, gym and office remain usable together


Garage ground floor and office first floor | 1:100 on A3 at 100% | No upper bridge to the house

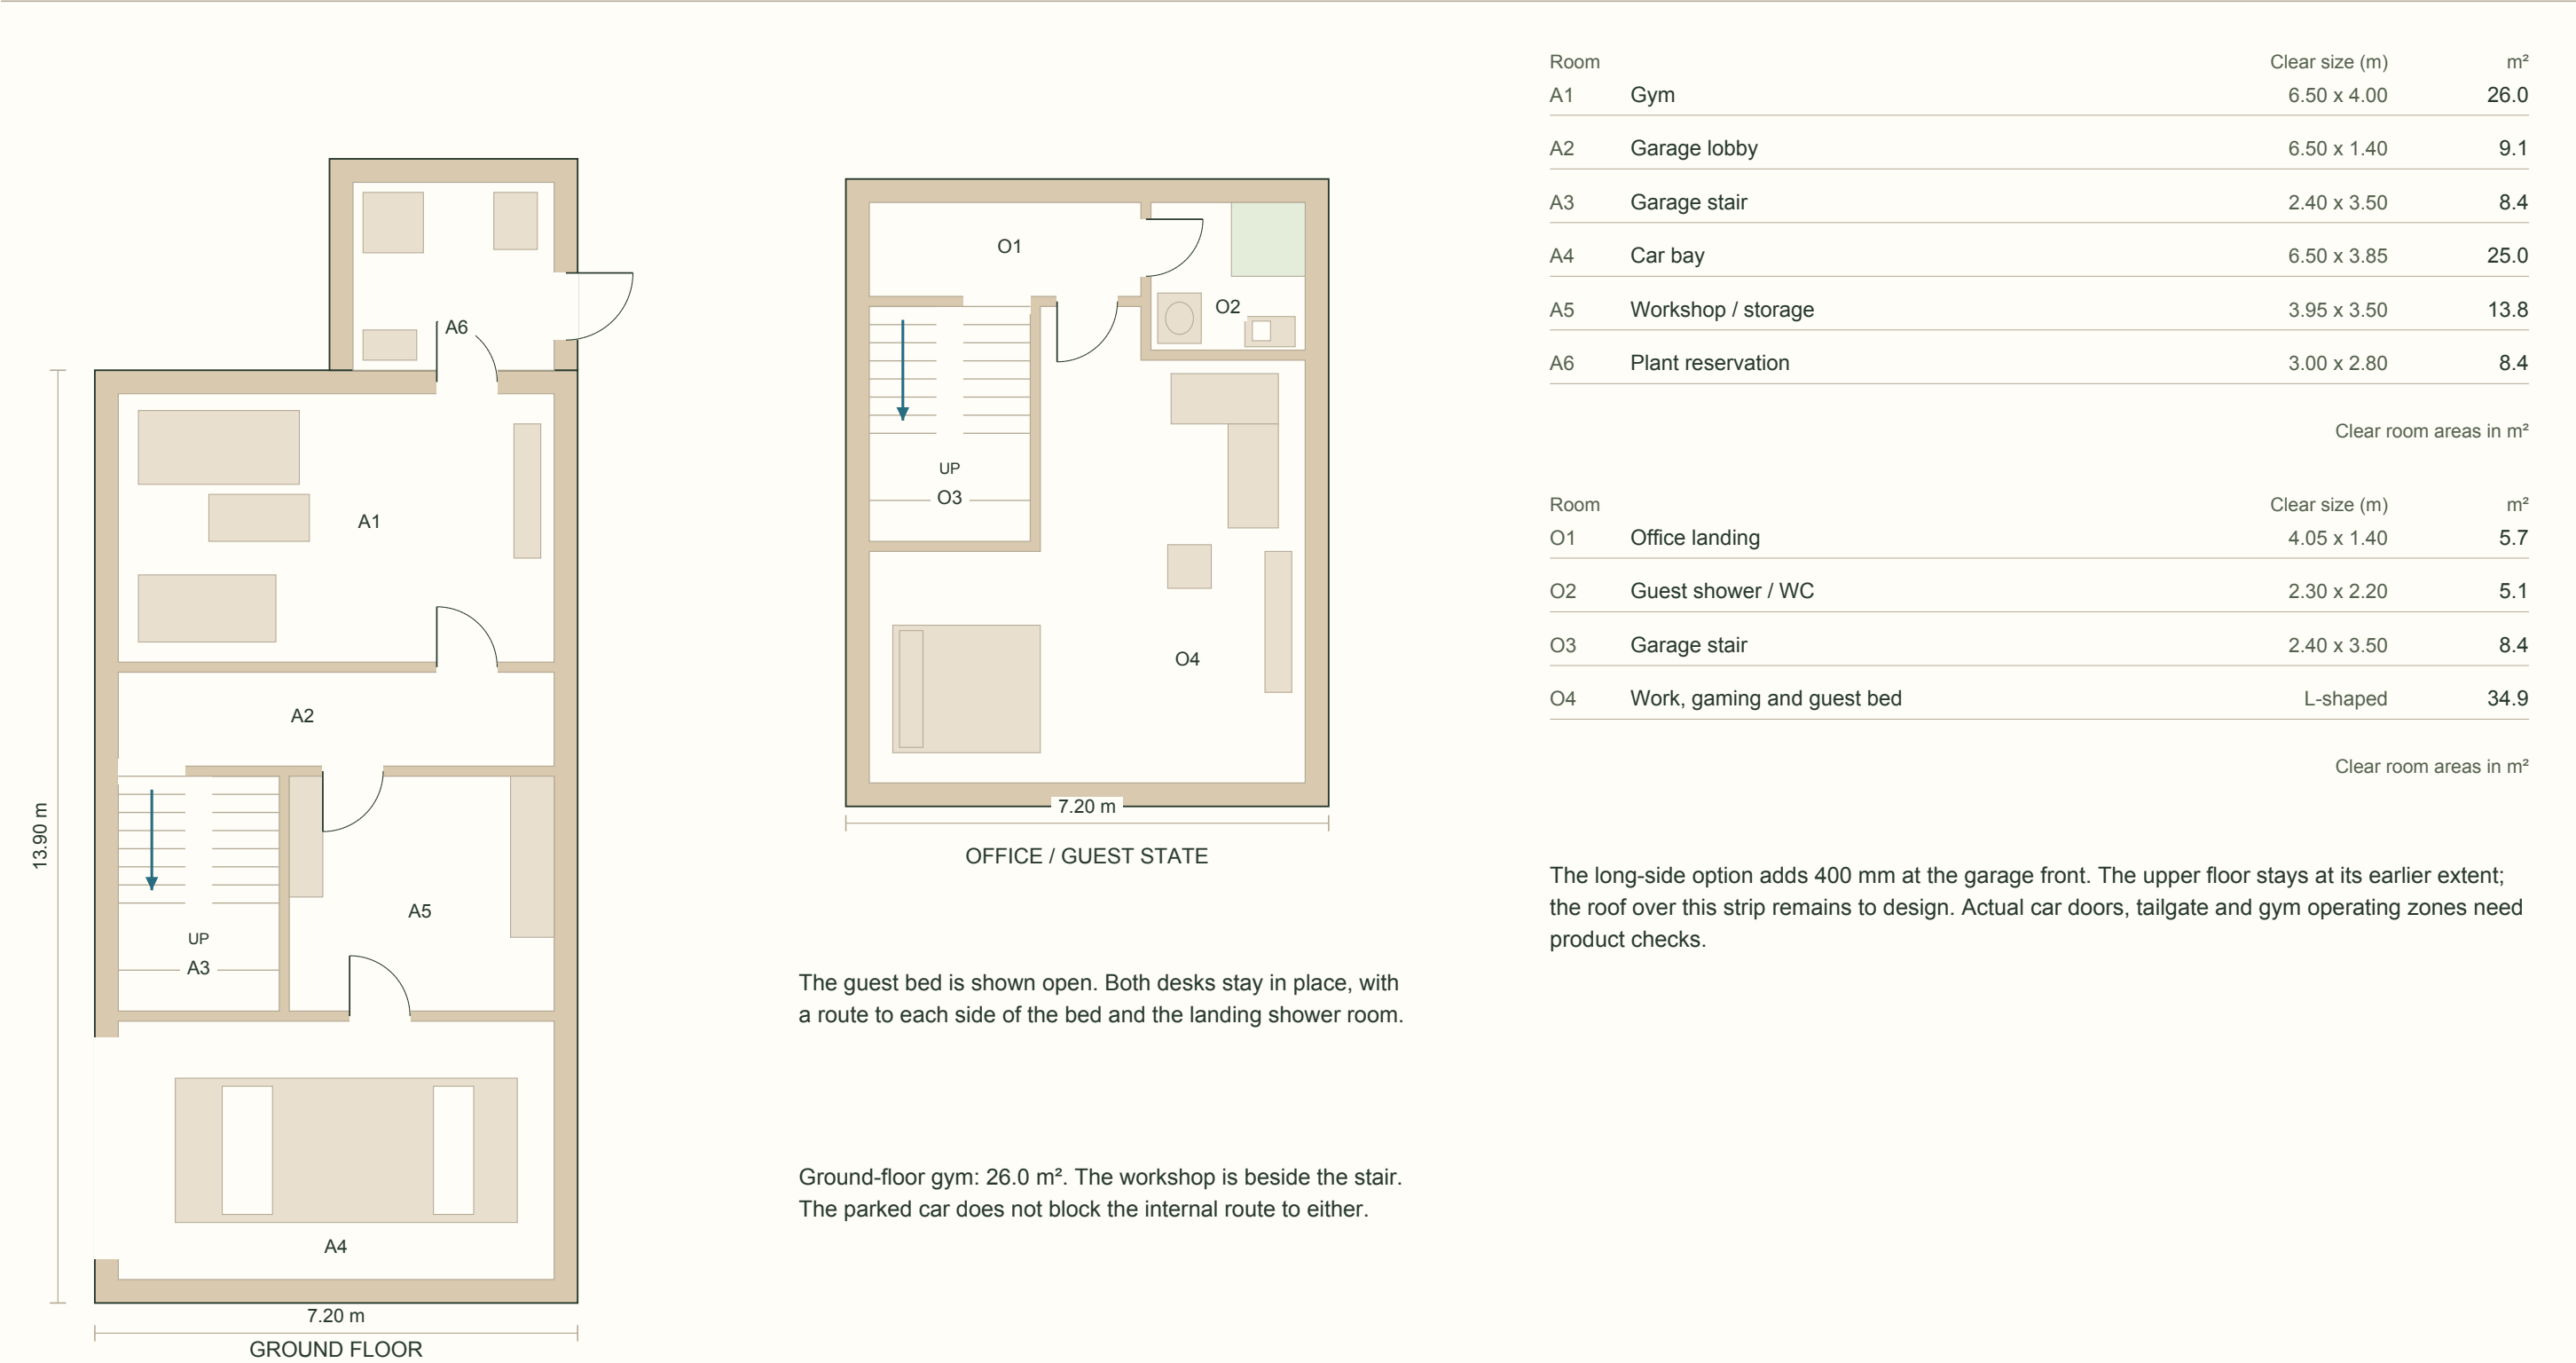

Pantry choice: connected by default, enclosed if preferred

Default kitchen and utility 1:50 | Enclosed pantry detail 1:50 | Both options keep direct kitchen access

DEFAULT / SHORT DIVIDER

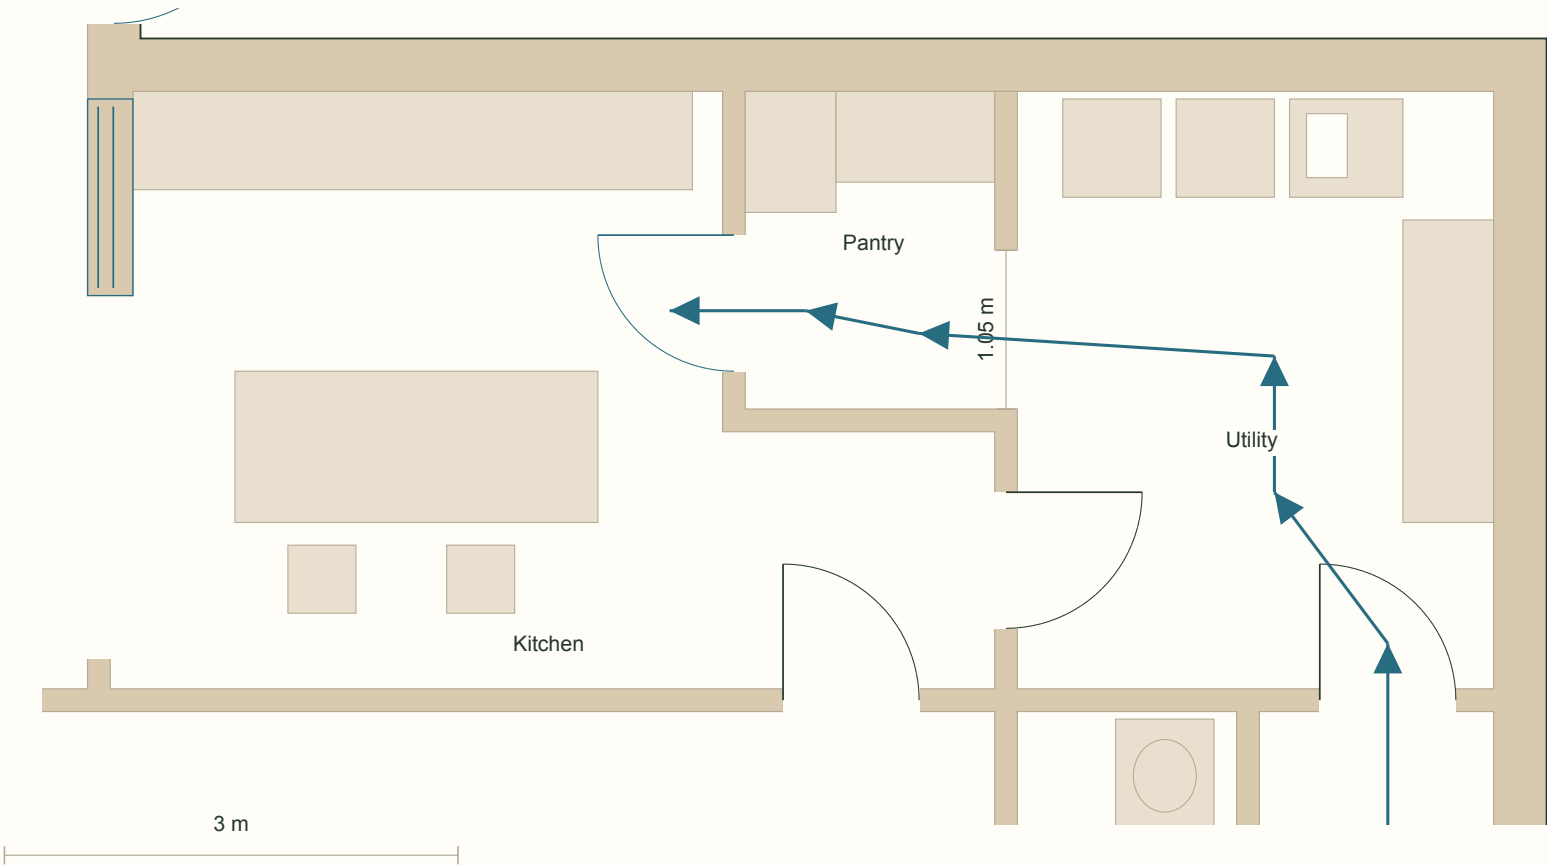


Default: two zones with an open connection

A full-height, 150 mm-thick divider projects 1.05 m from the rear wall. A 1.05 m passage connects pantry and utility. Dry storage stops clear of the partition. The shopping route runs directly from boot room to utility to pantry.

The kitchen door has a cabinet-style face and opens into the kitchen. The 2.40 m kitchen / dining opening can close with sliding panels. The drawing shows the panels retracted.

OPTION / ENCLOSED PANTRY

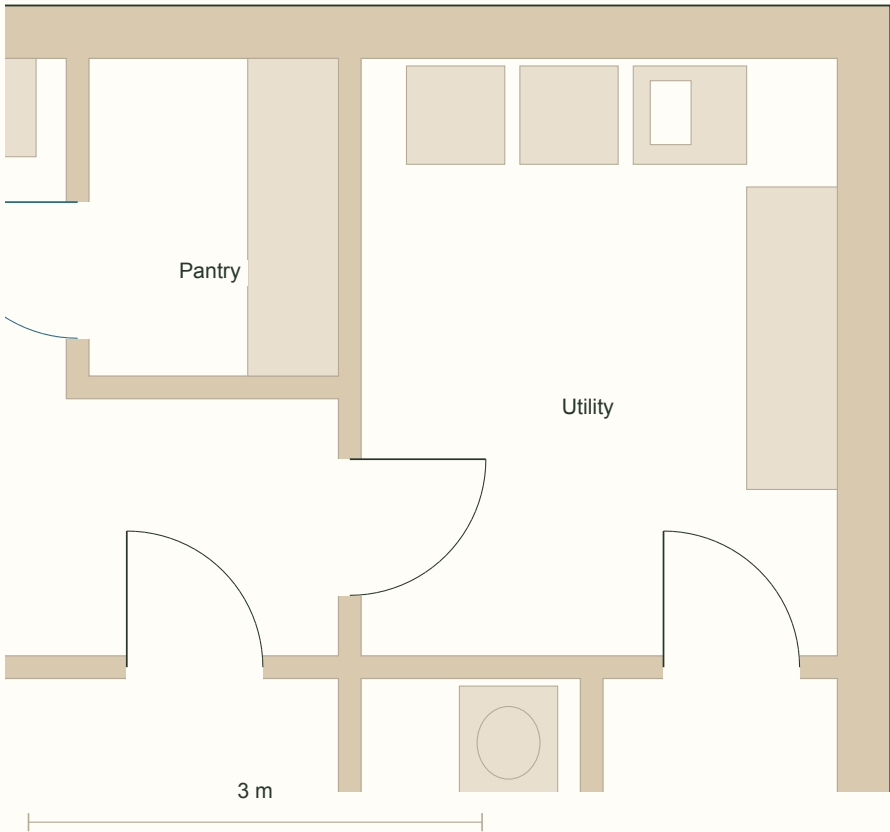


Enclosed option retained

This restores the full dividing wall and the earlier pantry shelving. The pantry opens directly from the kitchen; the utility keeps its kitchen and boot-room doors.

Trade-off: shopping reaches the pantry through the kitchen. There is no connecting pantry / utility door in this retained option.

Parents suite: private route and a deep soaking tub

Suite 1:75 | Ensuite detail 1:40 | Room boundaries unchanged

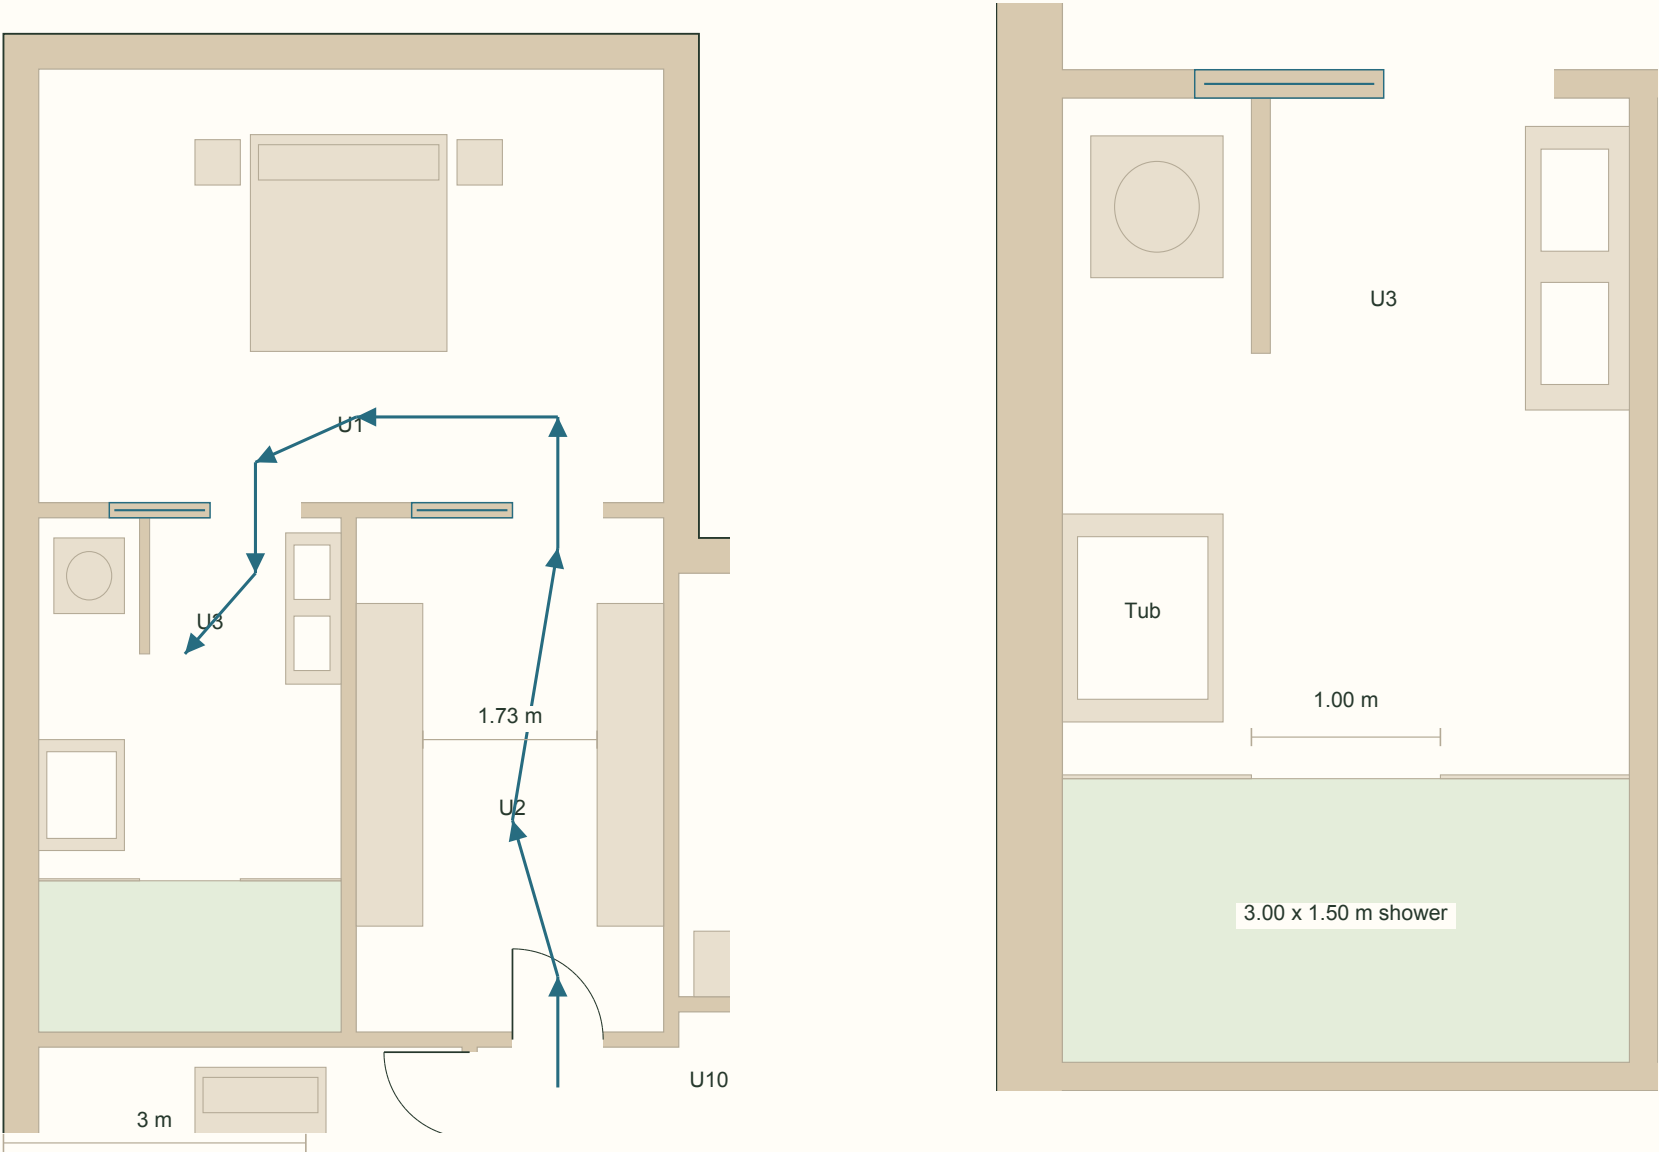

A clear view into the room

The WC sits behind a short return wall. Two basins are opposite. The far end is a full-width shower, with two fixed screens and a central entry.

Compact bath, generous shower

The tub space is 1.10 x 0.85 m. A manufacturer size reference is 1.05 x 0.75 m, with 0.60 m internal depth. Comfort, getting in and out, filled weight and drainage remain product checks.

Two pocket doors


The bedroom and ensuite openings each retain 900 mm width with a 1.00 m adjacent pocket reservation. Keep plumbing and fixings out of the cavities.

Size reference only, not a product selection:
[Omnitub Solo 1050 x 750 mm](#)
Manufacturer dimensions checked 6 October 2026.

Dressing room: 1.73 m between closed wardrobe fronts; 0.50 m open drawers leave about 1.23 m. The landing entry remains a hinged door. The same door positions are used in the full plan and these details.


Family bathroom and stair assumptions

Family bathroom 1:50 | Stair diagram 1:50 | Heights remain design assumptions

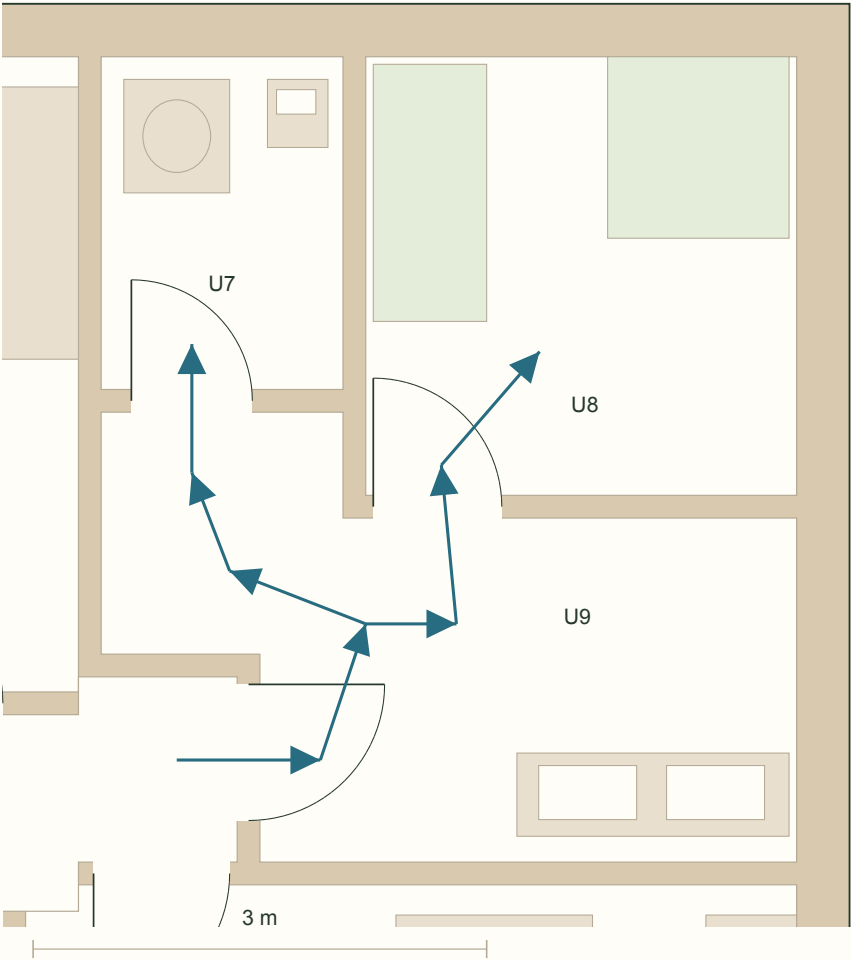

Three separate activities

Separate WC, separate bath / shower room, and a shared dry basin area. The WC also has its own hand basin. Changing space stays inside the wet room.

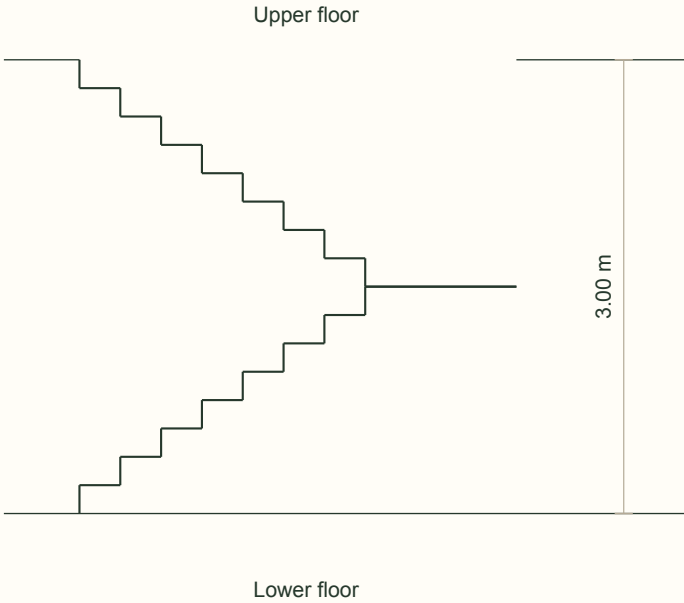

Both stairs

16 rises of 187.5 mm. Going 270 mm. Two 1.00 m clear flights and a 1.00 m half landing.

Section assumptions

Floor to floor: 3.00 m. Floor zone: 300 mm. Clear ceiling: 2.70 m. A full opening above both flights is reserved.

The drawing explains the assumed stair rise and run. Final headroom needs the roof, beams, landings and floor openings to be designed together. It is not a verified building-regulation section.

The next design stage will establish roof shapes, windows and structure, then build the approved plan in 3D. Detailed services routes must also be reworked for two storeys.

Review the plan first, then build the 3D alternative

Area summary, retained brief and decisions | This booklet is the approval stage for the floor plan

Proposed plot	2,600 m²
Rear garden strip before terrace / planting	1,120 m²
House external floor area, both floors	386.52 m²
Garage, gym, workshop and stair footprint	100.08 m²
Office external floor area	67.32 m²
Plant and enclosed link footprints	17.66 m²
Total building footprint	311.00 m²
Total external floor envelopes	571.58 m²

External areas include walls and stairs. Room schedules use clear room polygons, so the totals differ. These are study measurements, not certified floor areas. The garden strip is not a net lawn-area claim.

Evidence: shared geometry for full plans and details; two pantry snapshots; earlier furniture, door and walking checks; and a new plot-level illustrative vehicle sweep. No 3D model or published baseline is changed.

Review now

Plot proportions and garden depth; the arrival court and visitor spaces; both floor plans; garage and office use; and the default pantry arrangement. The enclosed pantry remains a documented alternative.

Carry into the next stage

Warm stone, timber and ivory; no grey finish palette. Retain footwear boundaries, separate family bathroom uses, landscape views, wet underfloor heating, active cooling and solar contribution.

Resolve after floor-plan approval

Roof and window design, stair headroom, structure above the garage opening, bathroom and plant routes, ventilation, and a real-site car-turning check. The former courtyard vault and glazed garden-room roof are not resolved by this two-storey plan.

Sequence: approve or revise this booklet, then establish the vertical design and create the furnished 3D alternative. The existing courtyard model stays available for comparison.