


A dining terrace, a quiet seat and a planted edge

Courtyard plan 1:75 at A3, printed at 100% | Existing footprint and opening widths retained | Plan top points toward the main garden

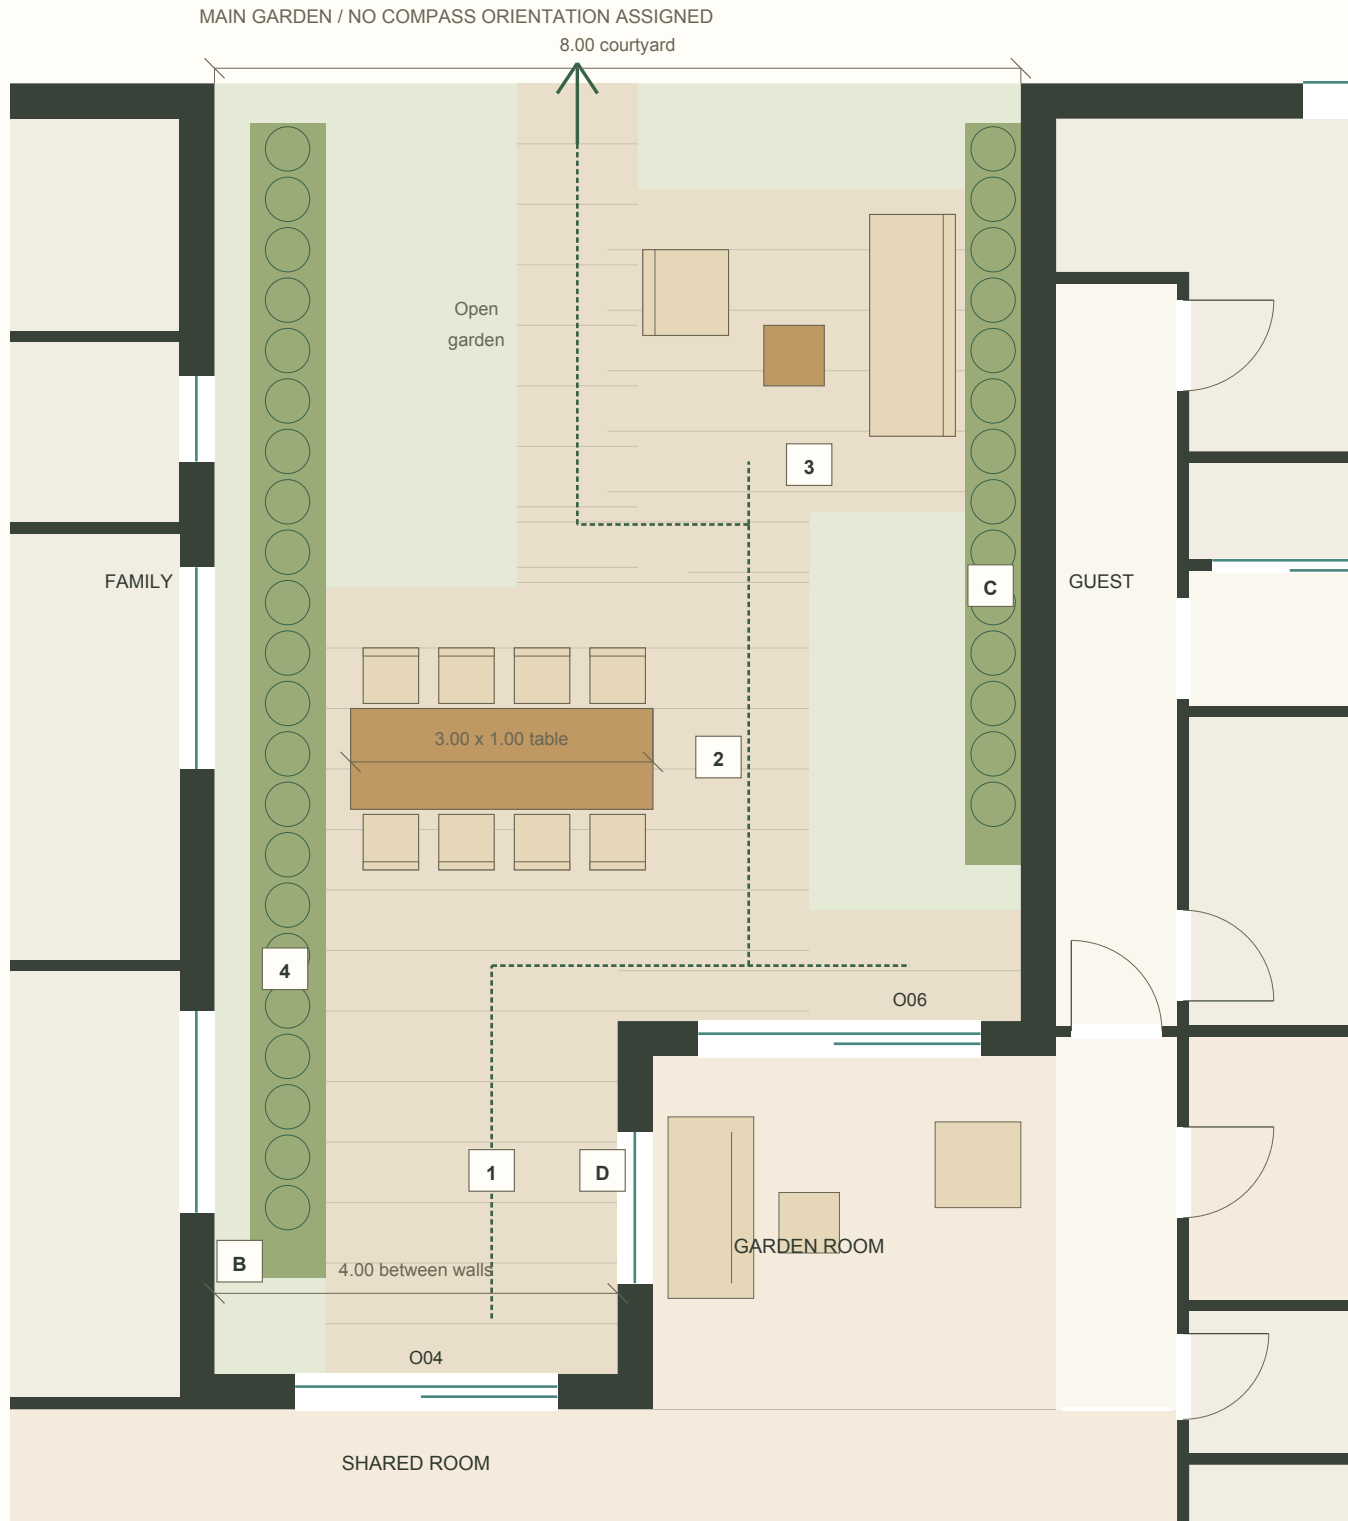

1 / KEEP THE NECK OPEN

The 4.00 m strip beside the garden room is the route out.
A broad paved landing connects the two existing sliders.
Keep furniture out of the final approaches to both doors.

2 / EIGHT OUTSIDE, CLOSE TO THE KITCHEN

A 3.00 x 1.00 m table sits in the wider part of the court.
Four chairs per long side; none at the ends.
The main route passes on the guest-wing side of dining.
Pulled-out chairs leave 1.10 m before the garden-room face.

3 / A SEPARATE PLACE TO SIT

A 2.20 m sofa, one chair and a low table face into planting.
This pad sits beside the guest wing's existing solid return.
It offers a different outlook from the dining terrace.
Sun, wind shelter and any overhead shade remain untested.

4 / FILTER THE BEDROOM EDGE

A 0.75 m planted band sits beyond a 0.35 m wall-side strip.
Test a maintained 0.90-1.20 m planting height by dining.
Lower planting nearer the garden keeps the mouth open.
This filters views; it does not establish bedroom privacy.
Review the actual window sills, daylight and mature growth.

MATERIALS + SPACE ALLOCATION

Warm buff paving, textured stone and warm-toned timber.
Open court: 88.40 m²; proposed paving: 50.78 m².
Remaining soft landscape / wall-side strips: 37.62 m².
Paving is more extensive than the earlier rough terrace.
Levels, drainage and surface specification are still open.


CHECKED / STILL TO CONFIRM

Four outside routes: sampled 1.00 m walking envelope.
Passes with dining chairs normal and pulled out 0.40 m.
Routes stop outside door faces; actual slider clear openings
and accessible thresholds require product and level design.

Stone wings, warm timber and a lighter garden room

Garden elevation A and courtyard returns B-D at 1:100 on A3 | Heights follow concepts 06B / 07B and remain provisional

A / FROM THE MAIN GARDEN: GYM LEFT, FAMILY WING RIGHT

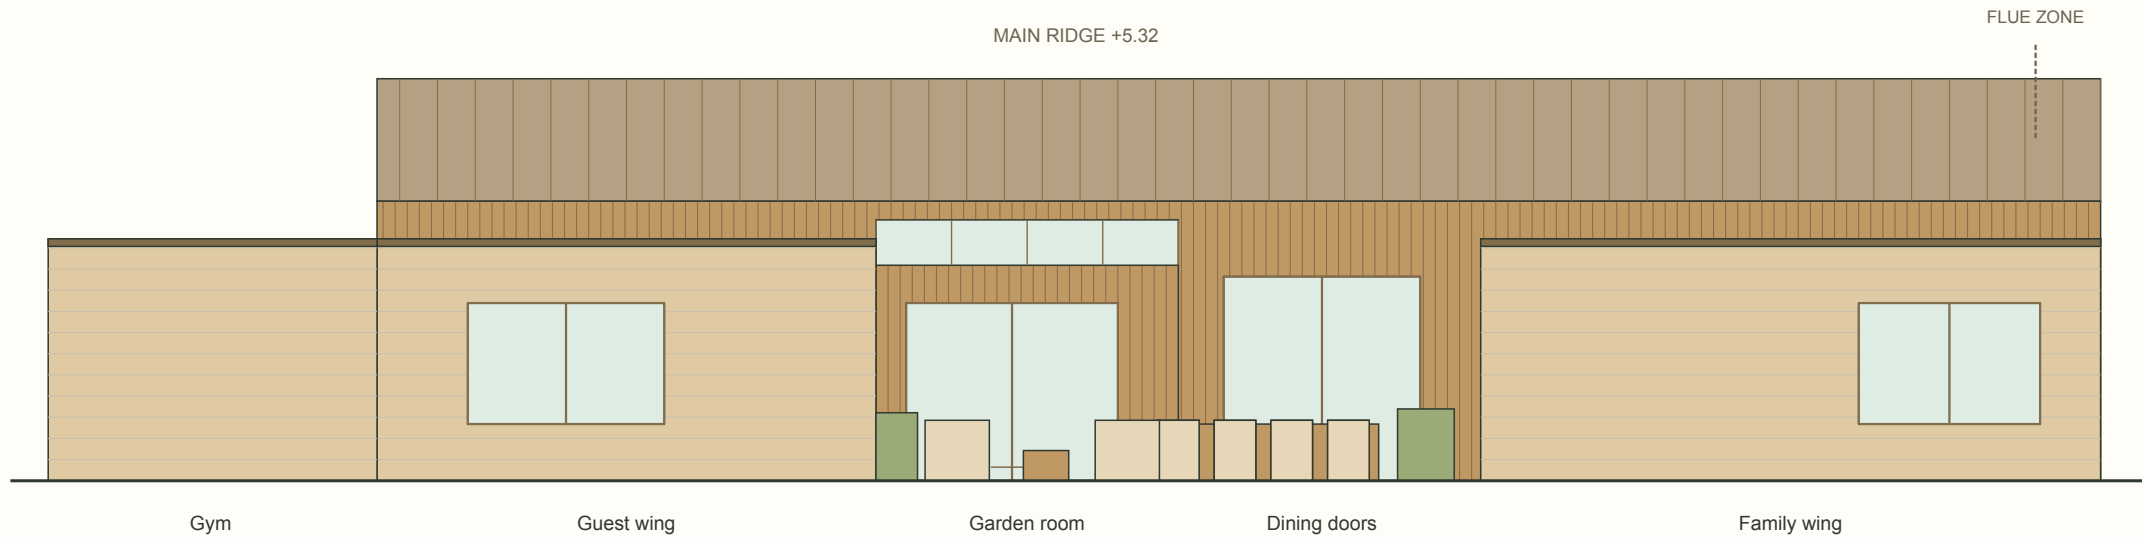

Orthographic projection: the front wings and deeper shared room align on paper. Use the plan to read their depth.


THE MATERIAL RULE

Stone on the projecting wings.
Vertical timber on shared living.
Warm bronze frames and slim edges.
Roof covering is a colour placeholder.
Timber finish needs a plan for retaining warmth as it weathers.


LEVELS BEING TESTED

Main eave +3.70 / ridge +5.32.
Low-wing roof envelope +3.20.
Garden glass +2.85 to +3.45.
Flue marker: termination height unresolved.


B / FAMILY RETURN

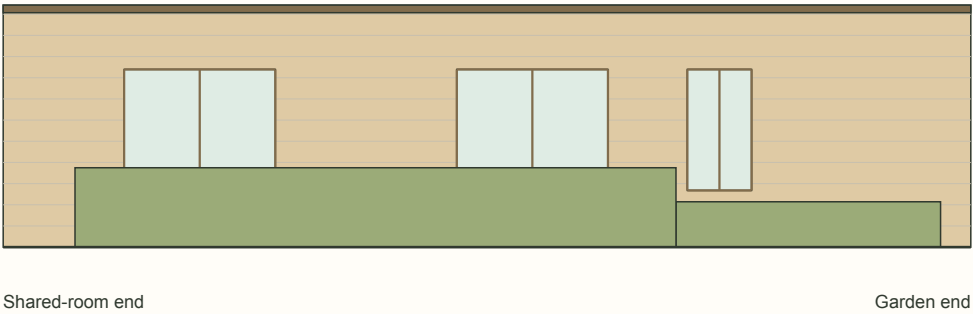

C / GUEST RETURN

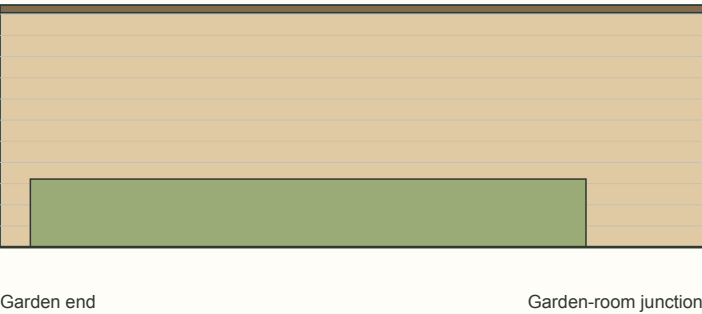

D / GARDEN-ROOM SIDE

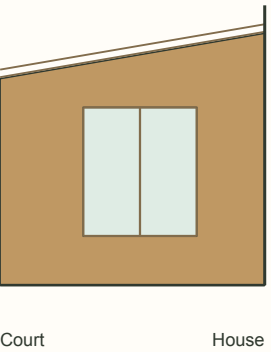

Glass rises
0.60 over 3.50 m
toward the house.

Approx. 9.7 degrees.

WINDOWS + PRIVACY

Existing family-side window positions and widths stay.
Planting height is a proposal to test against views and light.
The guest return stays solid above its planted edge.
Its existing outward-facing windows are on the other side.

SLIDERS + THRESHOLDS

O04: 2.60 m overall; O06: 2.80 m overall opening.
Two-panel operation shown; aim for at least 1.20 m
clear passage after framing, subject to supplier design.
Drainage, flush access and shading hardware need fitting.

JUNCTIONS TO DEVELOP

Low-wing roofs against the taller main eave.
Glass roof against timber wall and guest wing.
Coordinate gutters, flashings, insulation and
external shading before fixing edge dimensions.

