


A place for the things that arrive with you

Furnished plan 1:50 at A3 | D19 adds direct kitchen / utility access | South up / north down / east left / west right

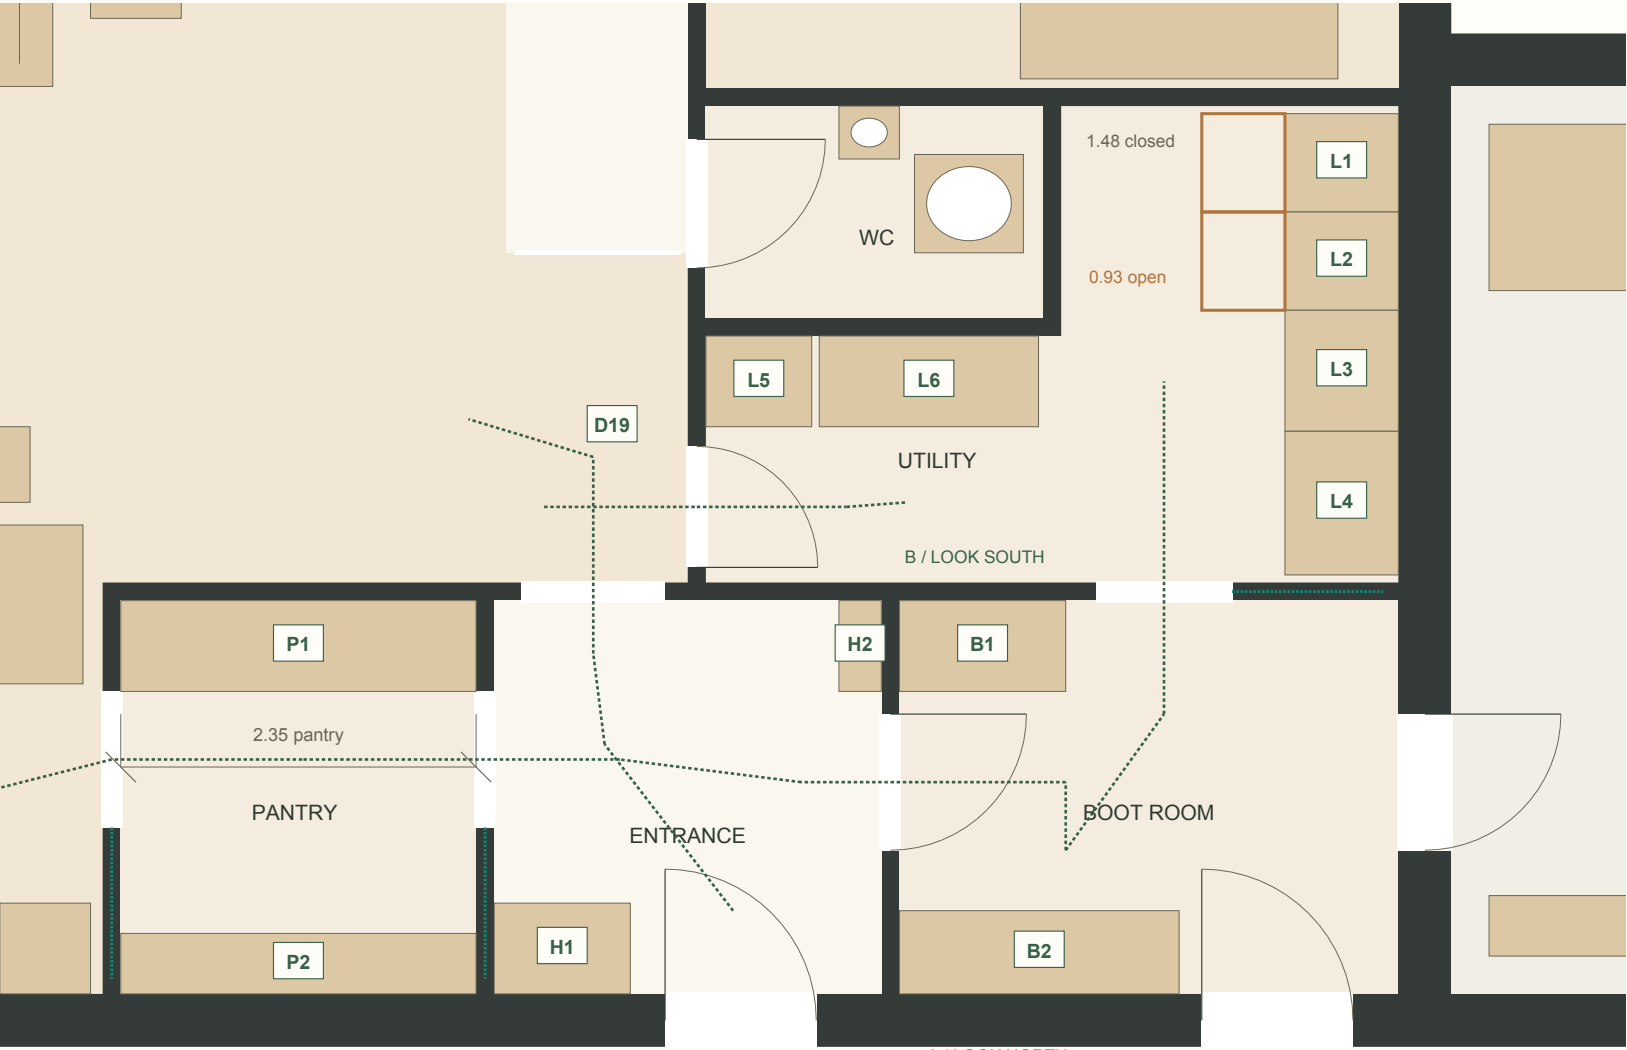

Dashed green: arrival / shopping / laundry routes.

Amber outlines: 0.55 m open-machine projections.



D19 / DIRECT KITCHEN ACCESS

0.80 m opening allowance; leaf opens back into the utility.

Retain boot-room access. Final frame / clear passage to specify.

Coordinate the door head with the adjacent ambient lighting.

B1 + B2 / BOOT ROOM

1.10 m closed coats / bags; 1.85 m oak bench.

Three shoe bays below and five staggered hooks above.

Wet coats stay on the open hooks, not in closed storage.

Bench stays outside the house-door swing.

H1 + H2 / ENTRANCE

0.90 m visitor-coat cupboard beside the front door.

A 0.28 m-deep keys ledge and mirror near the shared room.

Use the boot-room bench for muddy shoes and bags.

L1 - L6 / UTILITY

Separate washer / dryer bays, sink and sorting drawers.

1.45 m folding counter with basket spaces below.

0.70 m ventilated hanging-cupboard reservation.

Its airflow and drying capacity still need design.

P1 + P2 / PANTRY

2.35 m counter wall, 0.60 m deep, with open shelves above.

Opposite: 0.40 m-deep food shelving.

1.60 m clear between fronts with drawers closed.

WHAT WAS CHECKED

17 sampled routes pass at 0.70 m width.

Room-door sweeps clear the proposed furniture.

Routes pass with machines and the D19 leaf fully open.

Actual appliance hinges and cupboard use need checking.

THE TRADE-OFF

The utility return has a 1.03 m aisle beside the folding top.

It is primarily a one-person work zone.


Drawers / baskets occupy circulation while being used.

No claim of two-person access or accessibility compliance.


Open hooks for wet things, cupboards for the rest

Boot-room elevations A / B at 1:25 | Hall cupboard at 1:40 | Heights are joinery proposals within a provisional 2.60 m room height


A / BENCH WALL - LOOKING NORTH

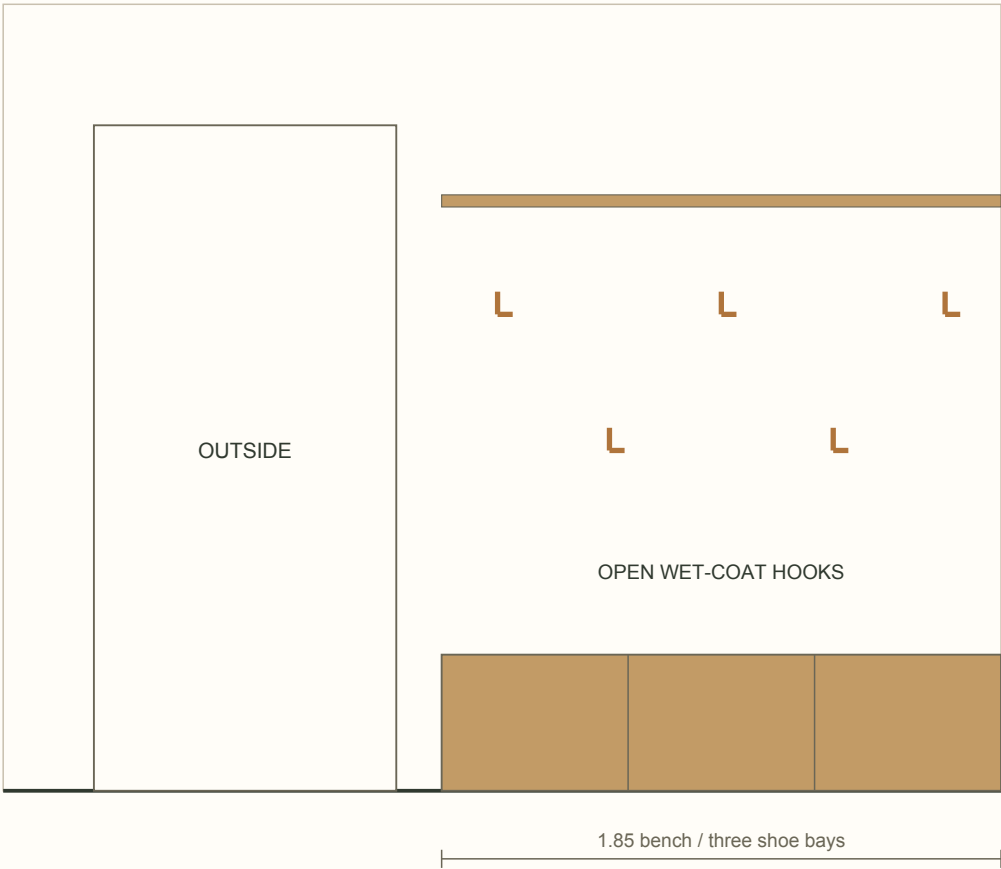

B / COATS + LAUNDRY DOOR - LOOKING SOUTH

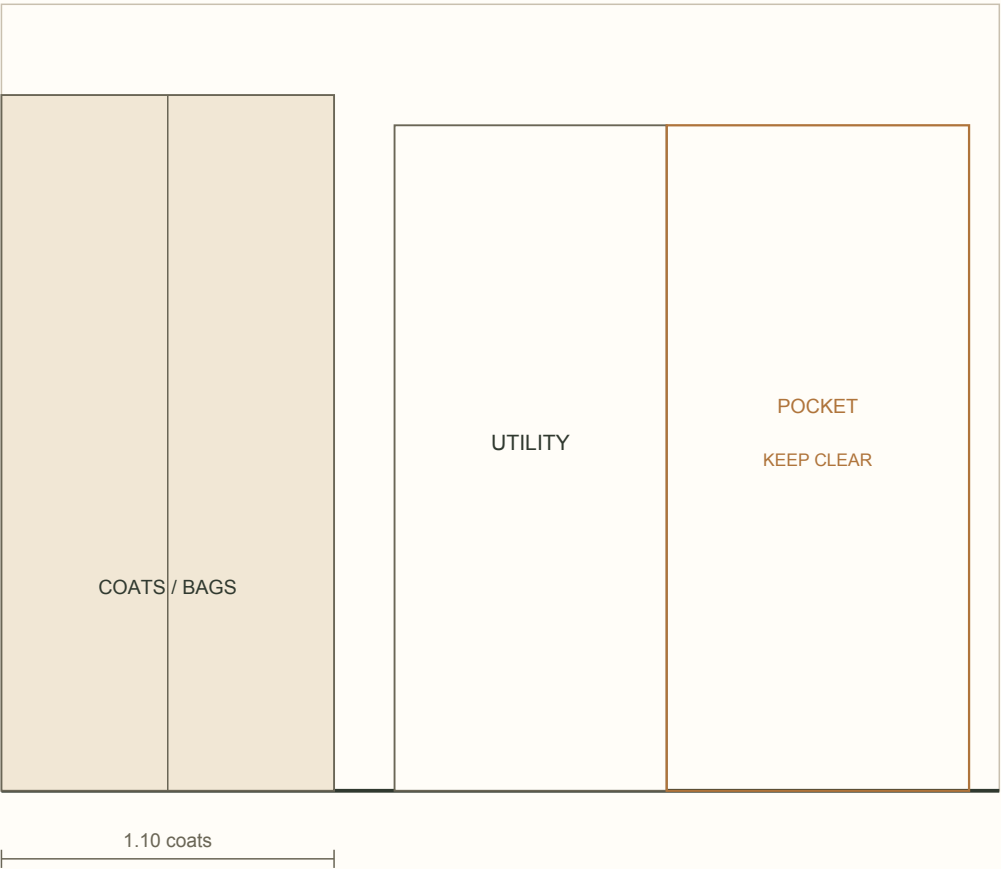

H1 / HALL COATS - 1:40

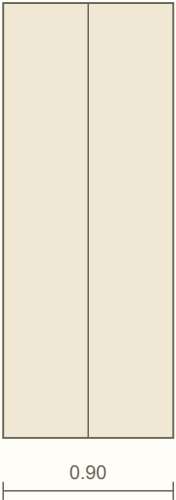

A QUIETER ENTRANCE

Visitor coats behind warm-ivory doors; shelf for hats / gloves.
H2: 0.60 m-long, 0.28 m-deep ledge at approximately 0.90 m.
Mirror above; exact size and wall fixings to coordinate.
Bench height 0.45 m; hook heights are 1.20 / 1.65 m proposals.

D19 / SOUND CONTROL

Investigate a solid-core leaf, perimeter seals and a suitable bottom seal.
Specify the complete doorset; no sound-reduction rating is claimed.
Coordinate the seals with a designed ventilation transfer path.

MATERIALS + INSTALLATION


Warm ivory closed storage, honey oak bench and bronze hooks.
Continue the warm hard floor; allow a washable entrance mat.
Use sliding fronts for B1 / H1 to limit cupboard-door projection.
Check hanger depth, tracks, ventilation and actual usable storage.
Keep laundry pocket cavities free of service runs and fixings.

Acoustic reference: Lorient sealing systems

Wash, sort and fold within one room

Utility elevations at 1:25 | L1-L4 looking west; L5-L6 looking south | Cabinet / machine dimensions are allowances, not selected products


LONG WALL / 3.15 M

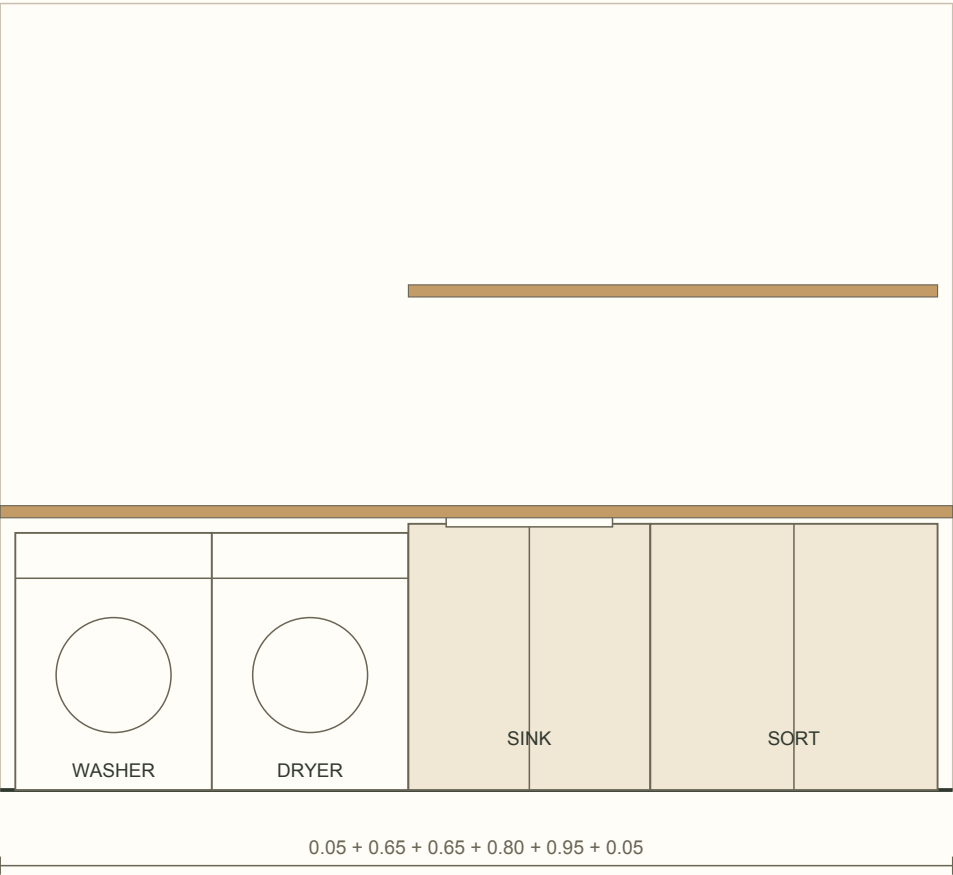

APPLIANCE ACCESS

Reserve 0.75 m from wall to worktop front for appliances / connections.
Machine bays are 0.65 m wide; model, hoses and tolerances still matter.
1.48 m aisle closed; 0.93 m behind the 0.55 m open-door allowance.
This checks a rectangular reservation, not a selected hinge sweep.
Keep isolation valves, drainage and sockets accessible.

RETURN / 2.20 M

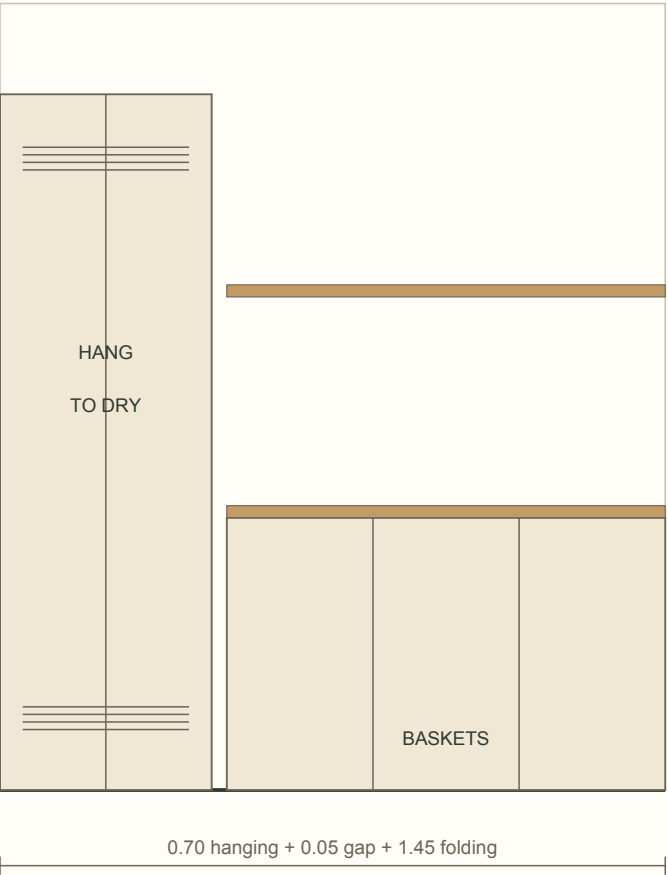

DRYING + WORKFLOW


The 0.70 m hanging cupboard is modest air-drying provision.
Use sliding fronts; airflow / extraction and moisture control need design.
It is not a demonstrated substitute for a full drying room.
Sort below the counter, fold on top and return baskets to the house.
Keep laundry noise and service penetrations away from the snug / WC.

Size reference only: Bosch WGG245S2GB lists 0.632 m depth including door and 1.049 m with door open; no appliance selected.

A pantry you can walk through and actually use

Pantry end-wall elevations at 1:25 | Clear room 2.35 x 2.60 m | Side walls reserved for the two pocket doors


P1 / COUNTER WALL - LOOKING SOUTH

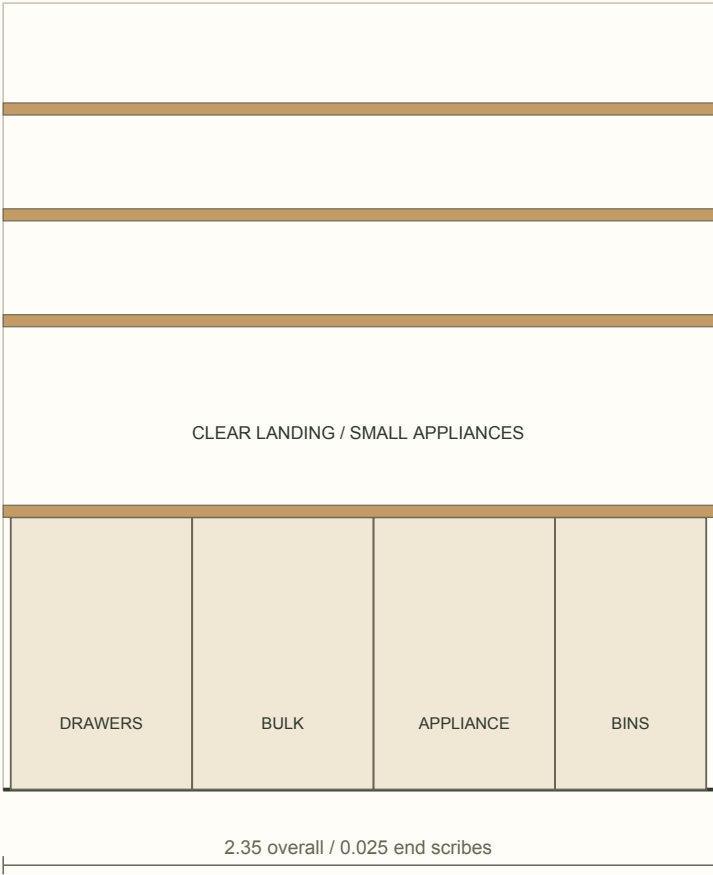

COUNTER WALL

0.60 m base depth; 0.30 m upper shelves; 0.92 m worktop height.
2.30 m nominal modules plus two 0.025 m end scribes.
Keep daily items reachable; use upper shelves for lighter stores.
Coordinate the shelf light beneath the first shelf and accessible sockets.
Select any countertop appliances before deciding shelf clearance.

P2 / FOOD SHELVES - LOOKING NORTH

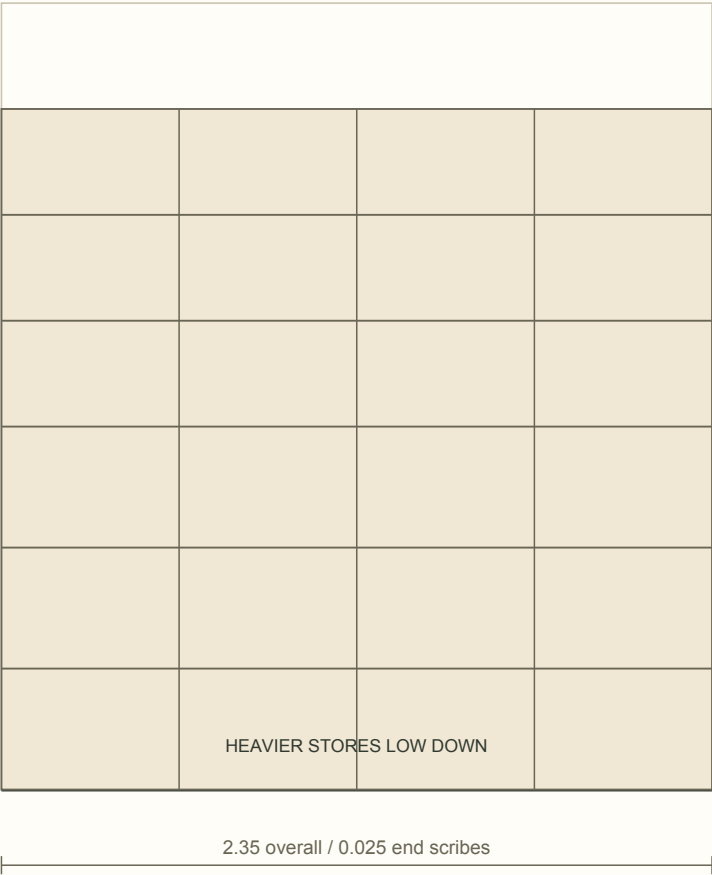

KEEP THE THROUGH-ROUTE USEFUL

Opposite shelves are 0.40 m deep, leaving a 1.60 m clear aisle.
One 0.50 m drawer projection leaves 1.10 m between fronts.
Doorways remain 0.90 m: avoid drawer use during shopping passage.
Do not fix shelves or run services through either pocket cavity.
No extra sink or refrigerator is assumed in this pantry.

Proposed joinery follows the ivory / honey oak / warm bronze palette. Cabinet divisions are preliminary; carcasses and hardware reduce usable space.