

Sleep, dress and get ready without a squeeze

Suite plan 1:40 at A3 | South up / north down / east left / west right | Super king confirmed | Double basins and separate shower take priority over a bath



WHAT THE FIT TEST TELLS US

25 sampled whole-house routes pass at a 0.70 m envelope, including six new suite routes. The bed foot has 1.75 m to the south wall; window operation still needs checking. Room-door sweeps clear proposed fixtures and furniture. The shower screen is a checked obstacle. Wardrobe drawers, occupied use, frame tolerances and door rescue access are not validated.

BEDROOM / A SOLID HEADBOARD WALL

Confirmed 1.80 x 2.00 m mattress; allow a 1.95 x 2.15 m frame. Turn the bed away from the existing south window. Allow 0.80 m east and 1.45 m west of the frame. Keep bedside furniture clear of the entrance swing. Final frame dimensions remain to select.

DRESSING / ROOM TO USE THE STORAGE

W1: 3.00 m hanging wall, 0.66 m overall depth. W2: 2.10 m shallow drawers / shelves, 0.35 m deep. This leaves 1.09 m between the closed fronts. Use the shallow side for folded clothes and shoes. Keep the room-door pocket free of fixings / services.

ENSUITE / SHOWER-FIRST PROPOSAL

A 1.10 x 1.78 m shower zone occupies the far end. A compact 1.20 m double vanity and WC share the south wall. The shower uses a fixed screen and open entry. Option A retains the room sizes; Option B tests adding a bath. Sanitaryware and screen dimensions are allowances.


KEEP THE QUIET PART QUIET

The headboard backs onto the family bathroom. Coordinate plumbing and the separating wall build-up. Use individual bedside reading / dimming controls. Avoid a night-time route through the dressing room. No acoustic or lighting performance is claimed.

A calm bed wall and useful everyday storage


Bedroom head wall looking north and hanging wall looking south at 1:25 | Provisional 2.60 m ceiling

A / BED HEAD - LOOK NORTH

 

1.95 m frame fit test / low upholstered headboard

B / HANGING WALL - LOOK SOUTH

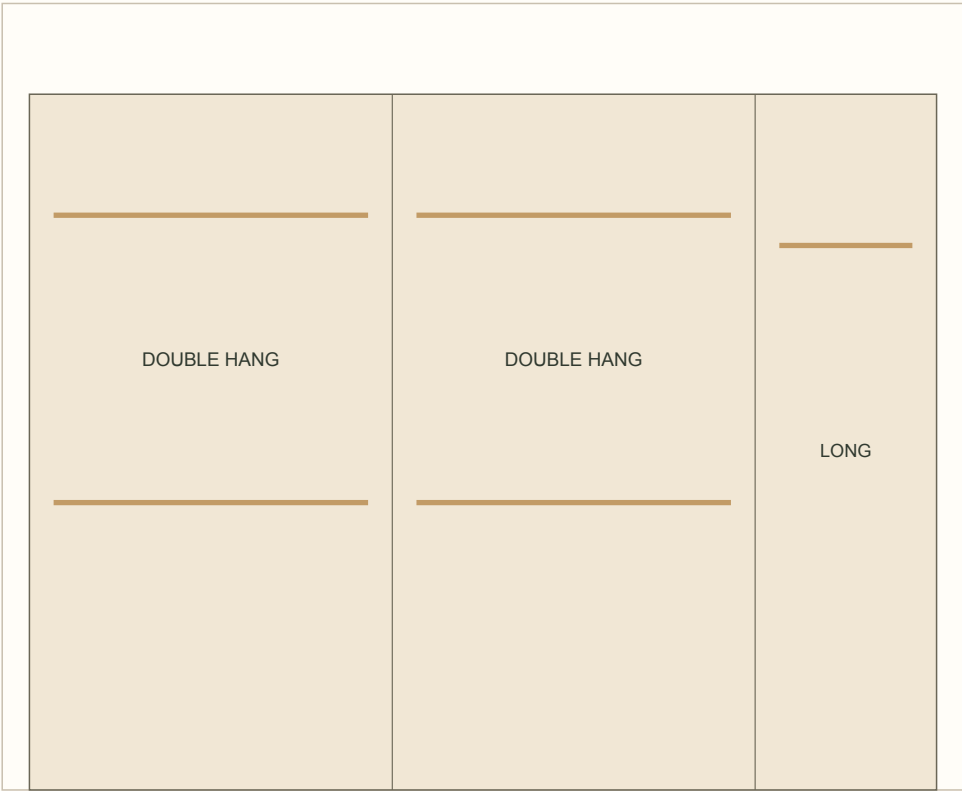

3.00 m overall / illustrative interiors, fronts omitted

BEDROOM LIGHT + MATERIALS

Warm ivory walls, linen headboard, oak bedside furniture and bronze lights.
Propose a wool-rich carpet; use blackout blinds at both bedroom windows.
Each side gets a reading light, accessible socket and independent control.
Separate soft general light from a low-level night route to the ensuite.
Choose the mattress / frame first; bedside heights should follow it.


DRESSING STORAGE + LIGHT

Two 1.20 m double-hanging bays and one 0.60 m long-hanging allowance.
Carcasses, dividers, door tracks and clothes reduce usable space.
Sliding fronts on the hanging wall; shallow drawers on the opposite side.
An end-wall mirror and front-facing wardrobe lights support dressing.
A pulled-out drawer temporarily occupies the aisle; test the hardware.

Depth reference: IKEA PAX / AULI is 0.66 m overall with sliding doors. This is a dimensional reference, not a selected wardrobe.

Give the shower the space it needs

Ensuite plan 1:20 and south-wall elevation 1:25 | 3.18 x 1.78 m clear / 5.66 m2 | Option A: double vanity and generous shower

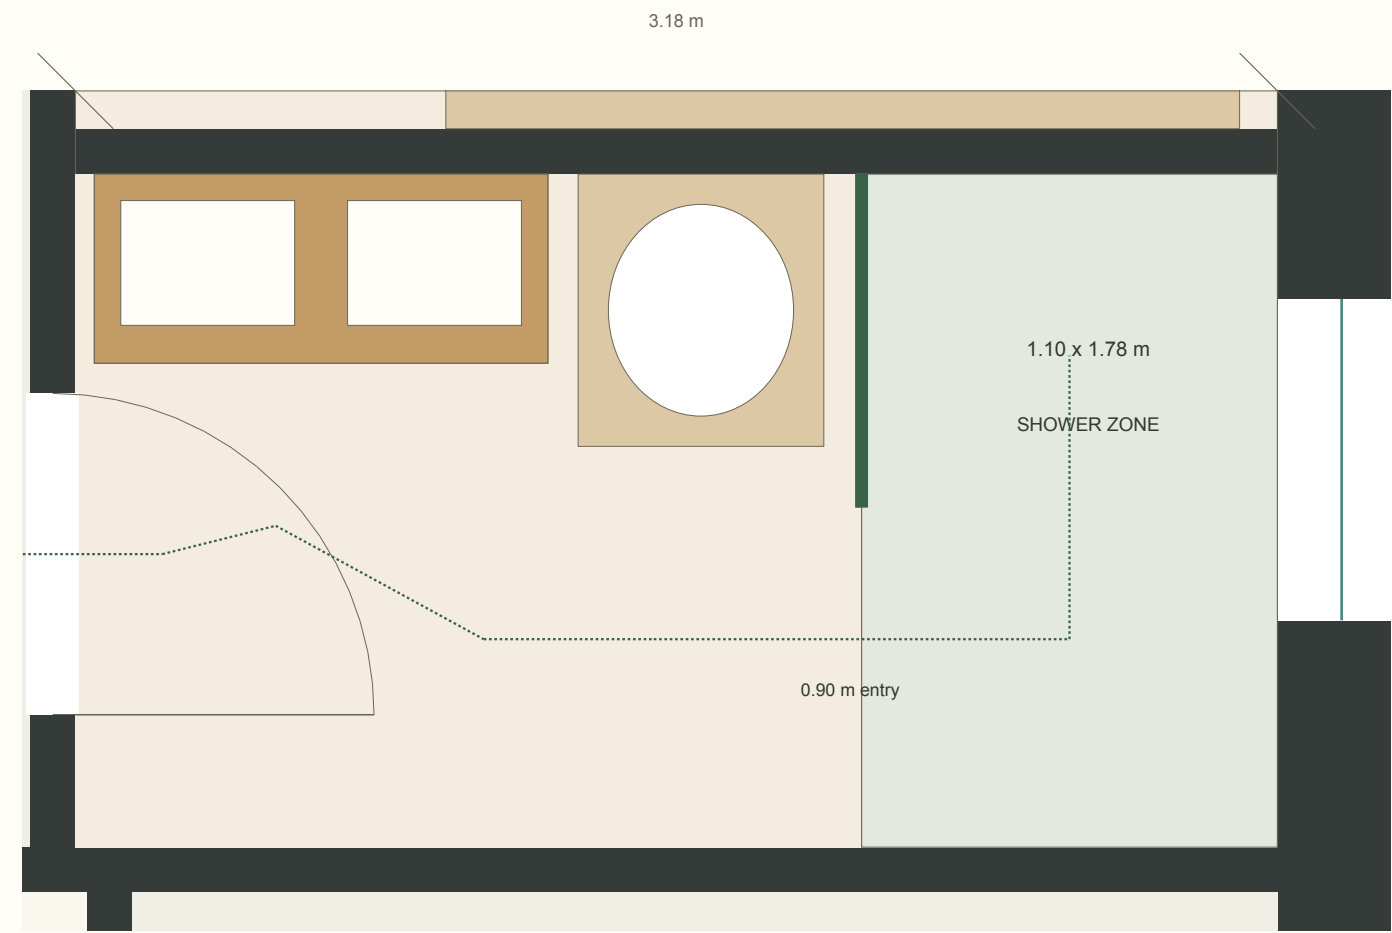

WATER + WINDOW

Treat this as a designed wetroom, not a loose tray allowance.
Coordinate floor falls, drainage, waterproofing and ventilation.
The existing courtyard-side window falls inside the shower zone.
Resolve privacy, waterproof reveals, sill and opening hardware.
Screen length and spray containment need product-level testing.

DAILY USE

Two basins share a compact 1.20 m vanity allowance.
Choose small basins, useful drawers and mirrored storage.
Fit controls near the shower entry to avoid reaching through spray.
Locate towel storage on the dry side, outside the door sweep.
Choose easy-clean, slip-appropriate surfaces and floor transitions.

LIGHT + FINISH


Propose warm ivory / buff porcelain and a honey-oak vanity.
Bronze fittings connect to the rest of the house.
Light the mirror from both sides; separate the low-level night light.
Bathroom electrical zones and suitable fittings require design.
No waterproofing, electrical or accessibility compliance is claimed.

DECISIONS TO CONFIRM

Super king, double basins and a generous separate shower are confirmed.
A bath is secondary; see Option B and its dressing-room trade-off.
Final WC, vanity, shower screen and wardrobe hardware.
The geometry fits; it is not a construction-ready bathroom design.


Wetroom reference: Schluter bathroom and wetroom systems

SOUTH WALL / LOOKING SOUTH - 1:25

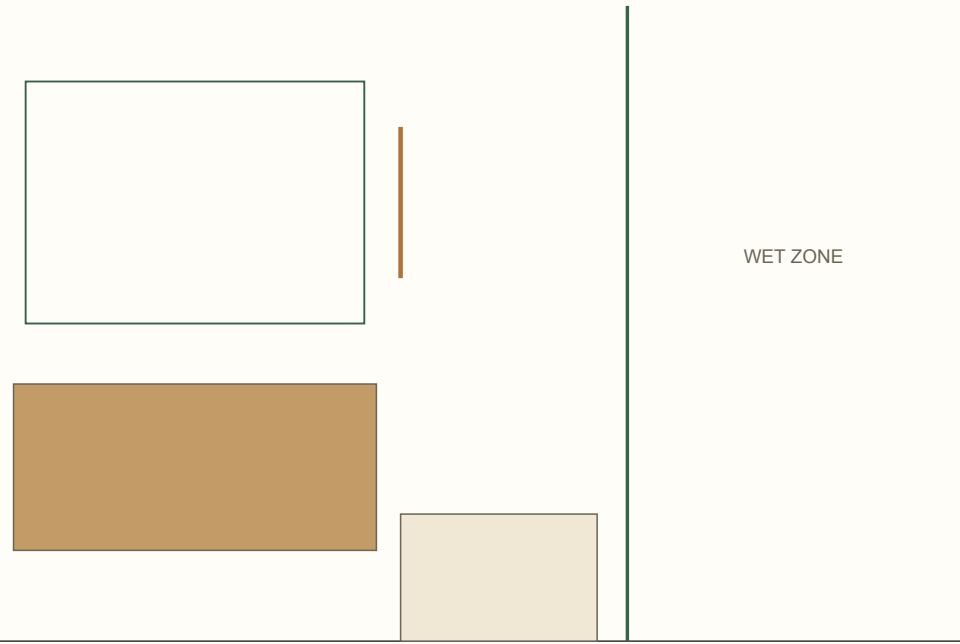

A bath fits, but the dressing room pays for it

Option B: move the ensuite partition 0.70 m towards the wardrobe | Suite plan 1:40 at A3 | Alternative for review, not a selected revision

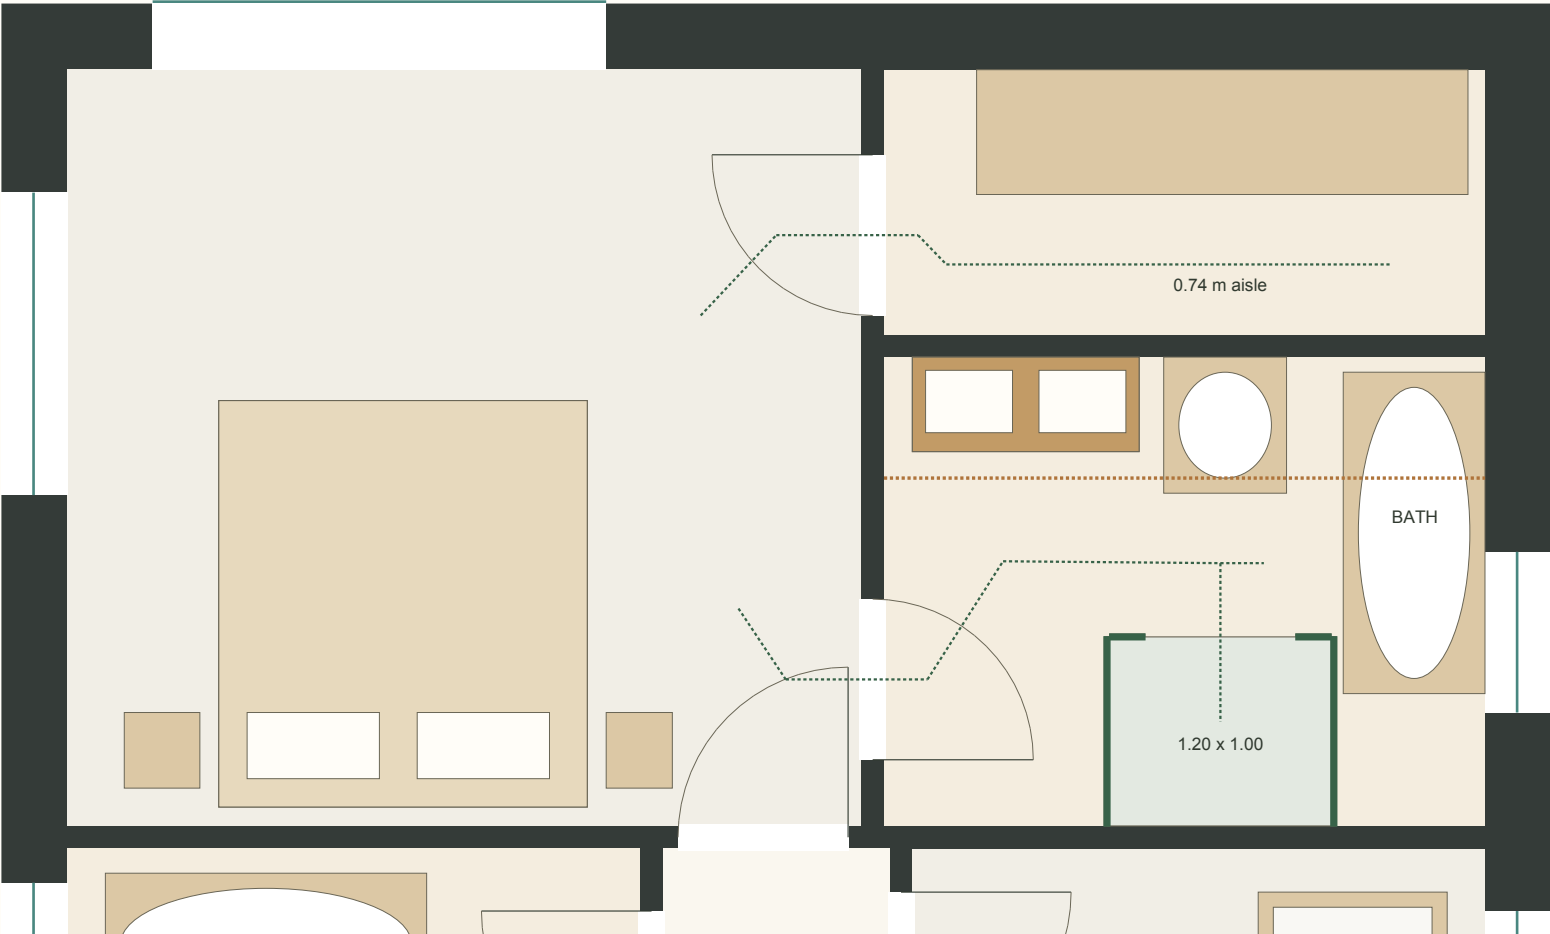

MY RECOMMENDATION / OPTION A

Choose A if double basins and a generous shower matter more than an ensuite bath.
It retains the larger 1.10 x 1.78 m shower, useful storage and a 1.09 m dressing aisle.
Option B adds the bath but makes the clothes store and bathroom approaches much tighter.
Amber dashed line: previous partition location. Both layouts retain a bath in the family bathroom.

PRIORITIES RETAINED

Super-king bed, 1.20 m double vanity and separate shower.
Shower allowance: 1.20 x 1.00 m with 0.80 m entry.
Bath allowance: 1.70 x 0.75 m along the outside wall.
Existing external walls and windows stay in place.

WHAT CHANGES

Ensuite grows from 5.66 to 7.89 m2.
Dressing room reduces from 6.68 to 4.45 m2.
Move the shared partition by 0.70 m.
Replace the wardrobe pocket door with relocated D20.
The new hinged door opens into the bedroom.

THE STORAGE COST

Hanging wall reduces from 3.00 to 2.60 m.
The 2.10 m shallow drawer / folded-clothes run is lost.
Only 0.74 m remains in front of the wardrobes.
Most dressing would happen in the bedroom.
This is a compact clothes store, not a generous dressing room.

FIT CHECK / OPTION B

26 sampled routes and door / furniture sweeps pass.
The shower approach has only about 0.75 m clear depth.
Door / screen frames and actual fixtures may consume that margin.
Do not freeze B without a detailed product and service layout.