


A small library with a comfortable place to watch TV

Snug plan 1:25 at A3 | 4.58 x 2.60 m clear | Books take the main wall and the former window wall

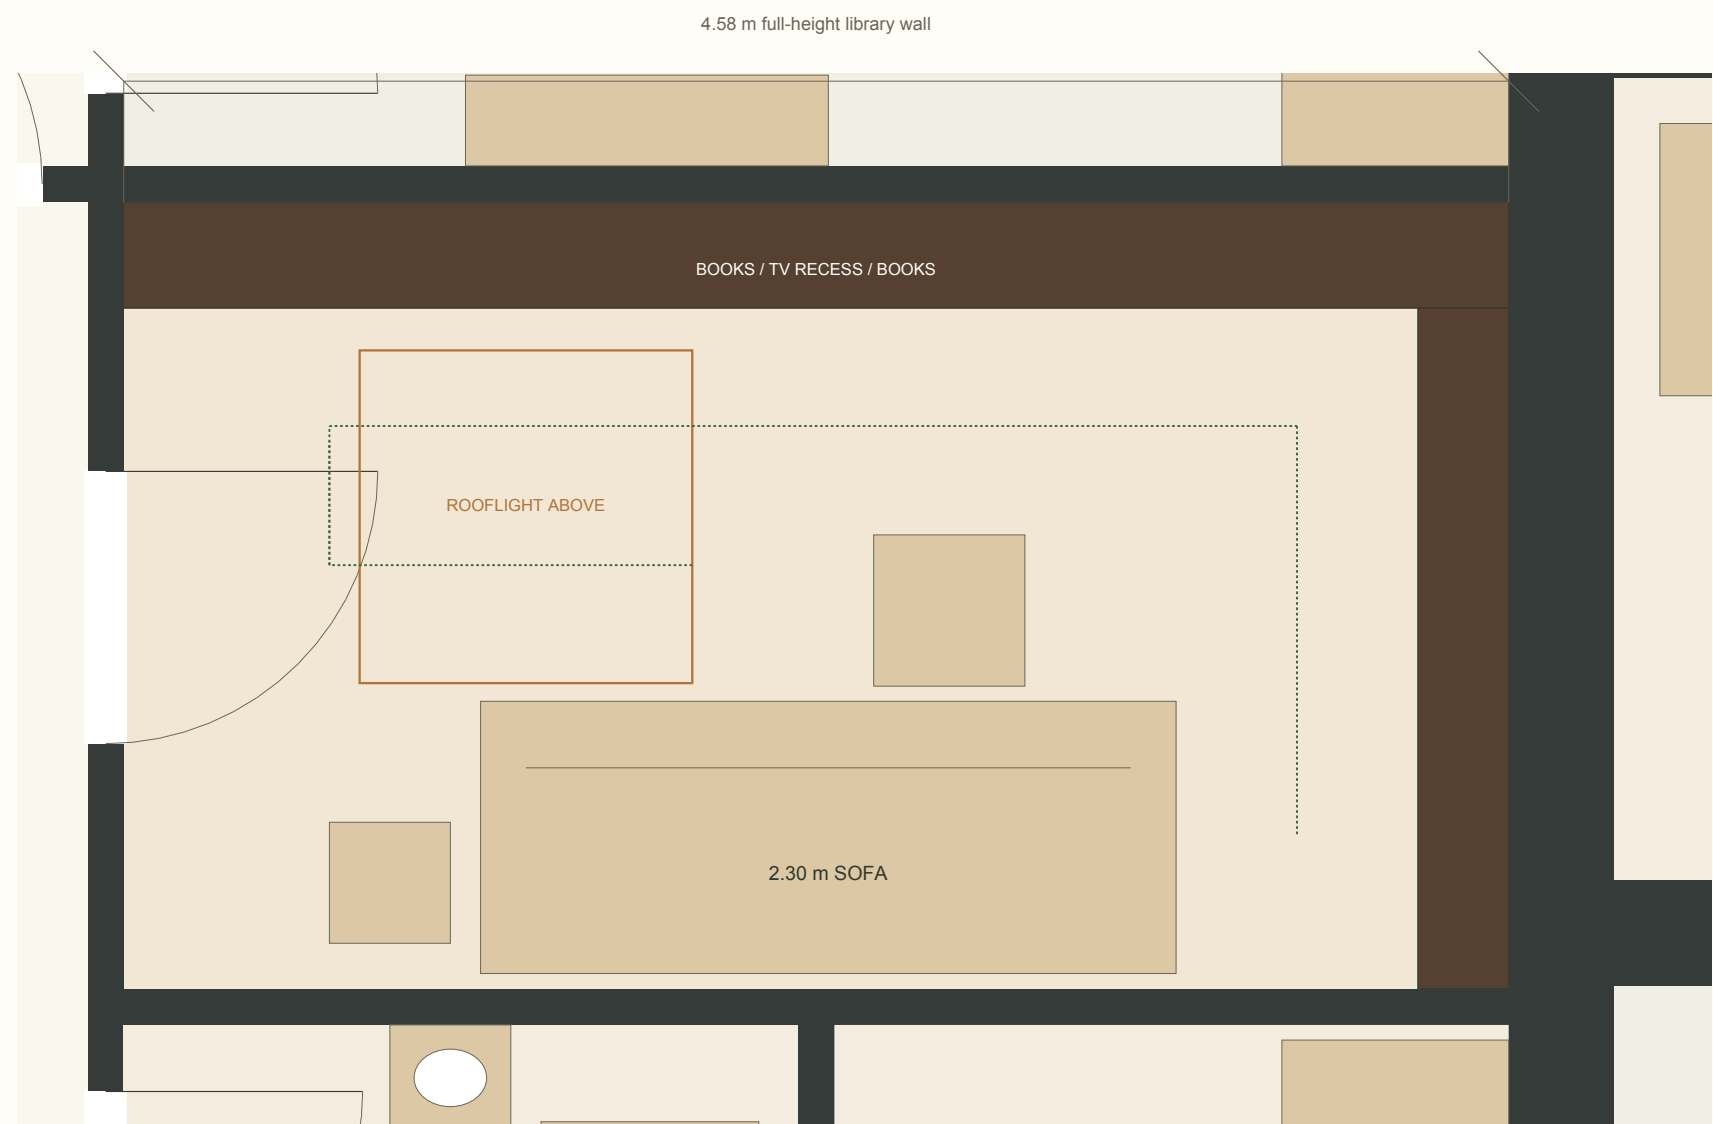

THE LIBRARY CHARACTER

Dark timber, framed cupboards and a modest cornice.
Full-height shelves with a central television recess.
Books continue onto the wall beside the plant room.
A soft sofa, footstool and warm reading light.

FIT WITHIN THE EXISTING ROOM

Main bookcase depth: 0.35 m.
Return bookcase depth: 0.30 m.
Sofa shifts 0.30 m toward the entrance side.
0.80 m remains between sofa end and return shelves.
0.75 m between footstool and main bookcase.

ROOFLIGHT AND PLANT ROOM


Retain the 1.10 m-square rooflight reservation.
Provide controllable shade for books and television.
Check glare, daylight, solar gain and roof structure.
The plant wall needs its own acoustic construction;
bookcases are not a substitute for sound isolation.

MEASURED CHECK

All 56 sampled routes pass in both office work modes and the overnight mode, including approaches to both bookcase runs.
The snug door, room size and garden-side plant proposal are retained. The side table moves away from the return shelves.
Shelf depth, cornice and cupboard projections must stay within these footprints. Upper-shelf access remains to plan.

The television sits within the books

South wall elevation 1:25 at A3 | Indicative 2.60 m joinery height, subject to actual ceiling and roof build-up

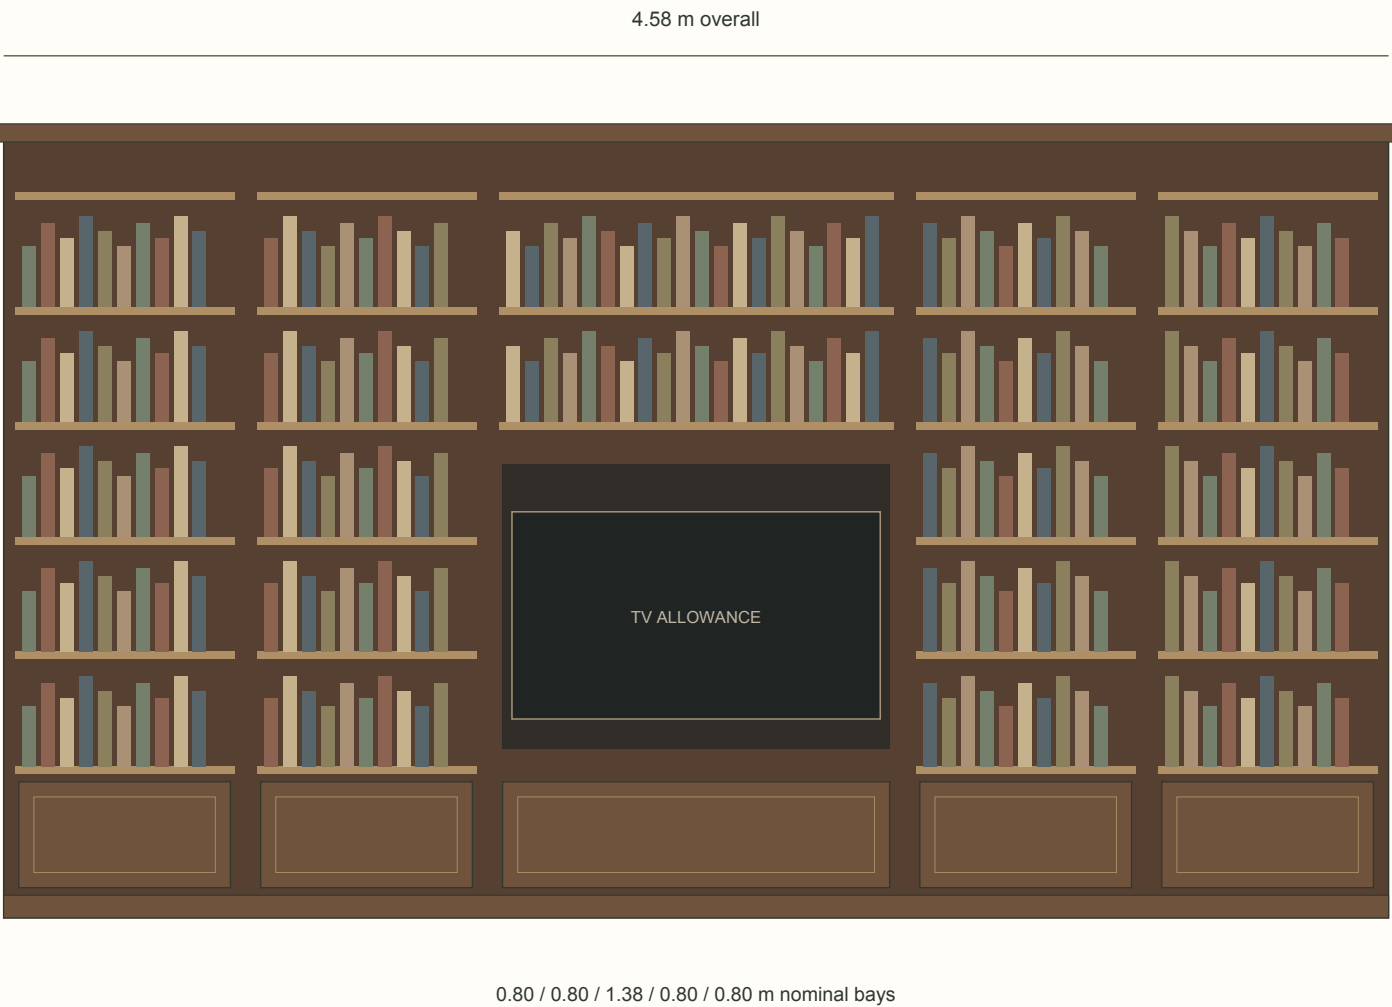

JOINERY LANGUAGE

Walnut-stained oak is a proposed material direction.
Framed lower cupboards, slim uprights and a cornice.
Adjustable shelves above; concealed storage below.
Shelf spans / fixings designed for the actual book load.

TELEVISION PROVISION

Indicative 55-inch, 16:9 screen within a 1.38 m bay.
Screen centre approximately 1.00 m above the floor.
TV size, viewing height and audio equipment to select.
Provide power, data, ventilation and removable access.
Final clear opening depends on the joinery members.

LIGHTING

Dimmable reading lights near each end of the sofa.
Optional small bronze picture lights on the bookcase.
Warm light and separate controls for reading / TV.
Check lamp positions against reflections on the screen.

ANTIQUE CHARACTER WITHOUT FILLING THE FLOOR

The detail is concentrated in the timber joinery, books, light fittings and upholstery. Keep the middle of this narrow room calm.
Choose a compact movable step for occasional upper-shelf access; store it in a lower cupboard and keep it out of the normal routes.

A return of books gives the room its library feeling

West / former-window wall elevation 1:25 at A3 | Joinery and material direction



2.25 m return beyond the main bookcase


A QUIET, WARM PALETTE

Dark stained timber and muted bronze fittings.

Warm cream or subdued moss on the remaining walls.

Textured wool upholstery and a comfortable footstool.


Use real material samples together before specifying.

 

TIMBER



MOSS

 

CREAM



BRONZE

COORDINATE BEFORE ORDERING JOINERY

Ceiling height and the meeting of both bookcase runs.

Rooflight structure, shade and opening / cleaning access.

Ventilation and any cooling outlet clear of the shelves.

Plant noise / vibration, wall fixings and service penetrations.

TV cables, equipment heat and access to sockets.

BRIEF UPDATE

The snug is now a library-led room with television provision. This supersedes the earlier low-storage / TV-led furnishing study.

No supplier, timber finish, TV, rooflight or light fitting has been selected; the drawings reserve space and establish the design direction.