


One plan, several roof junctions

Roof plan 1:100 at A3, printed at 100% | Metres | No north direction assigned

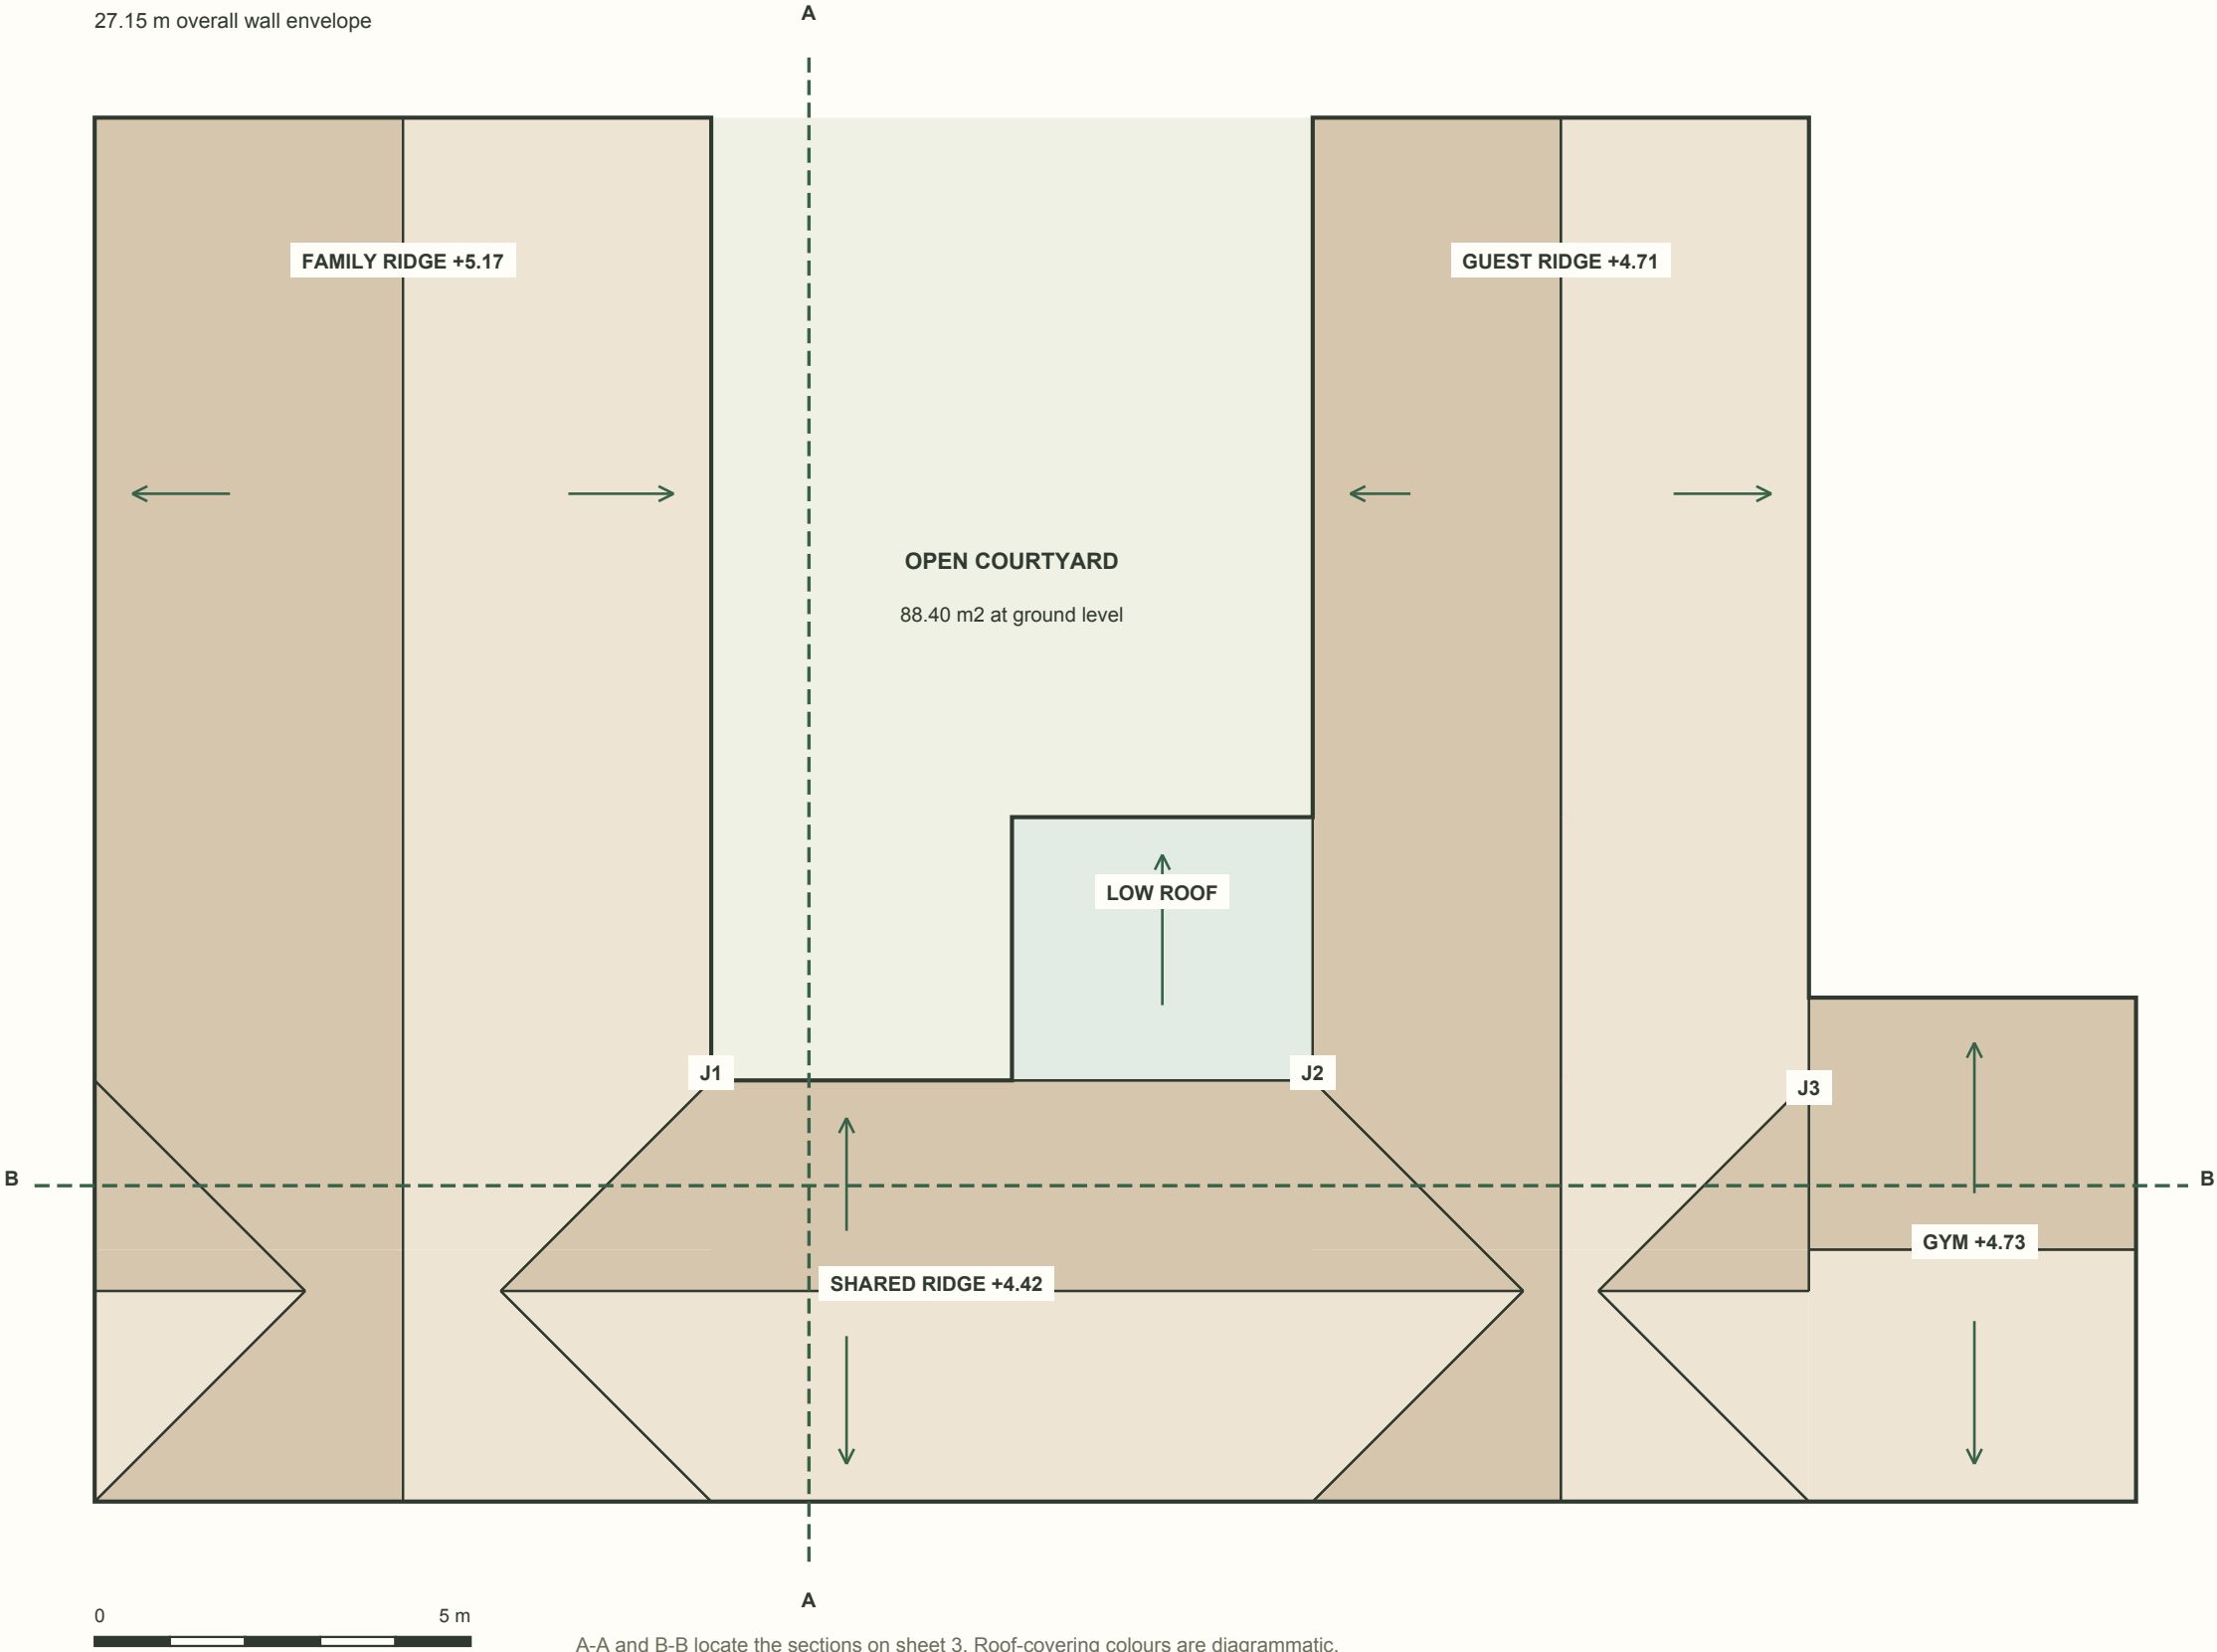

WORKING ASSUMPTIONS

30 degree main roof pitches.
+2.80 m roof datum at wall edges.
Levels measured above floor +0.00.
Roof lines stop at wall faces;
eaves overhangs remain open.

WHY THE RIDGES DIFFER

Family span: 8.20 m.
Guest span: 6.60 m.
Shared-room roof depth: 5.60 m.
Gym roof depth: 6.70 m.
A common pitch gives four heights.

JUNCTIONS TO RESOLVE

J1 Family roof meets shared roof.
J2 Guest / shared / orangery meet.
J3 Gym ridge runs across the wing;
a roof step needs detailing.

Arrows show surface fall only.
Valleys lead toward inside
corners; outlets are not designed.

ORANGERY: TEST ONLY

Low mono-pitch: +2.60 to +3.20 m.
Approx. 9.7 degrees, falling to court.
Its high edge meets the house
above the +2.80 m eave datum.
An abutment / local roof change
is required here, not yet resolved.


WHAT IS RETAINED

319.91 m2 GIA; 360.26 m2 footprint.
Room layout and wall geometry.
Rooflights await junction design.

Stone wings, timber shared room

Garden and arrival elevations 1:100 at A3 | Opening widths from concept 05; all vertical dimensions proposed

01 / FROM THE MAIN GARDEN, LOOKING INTO THE U

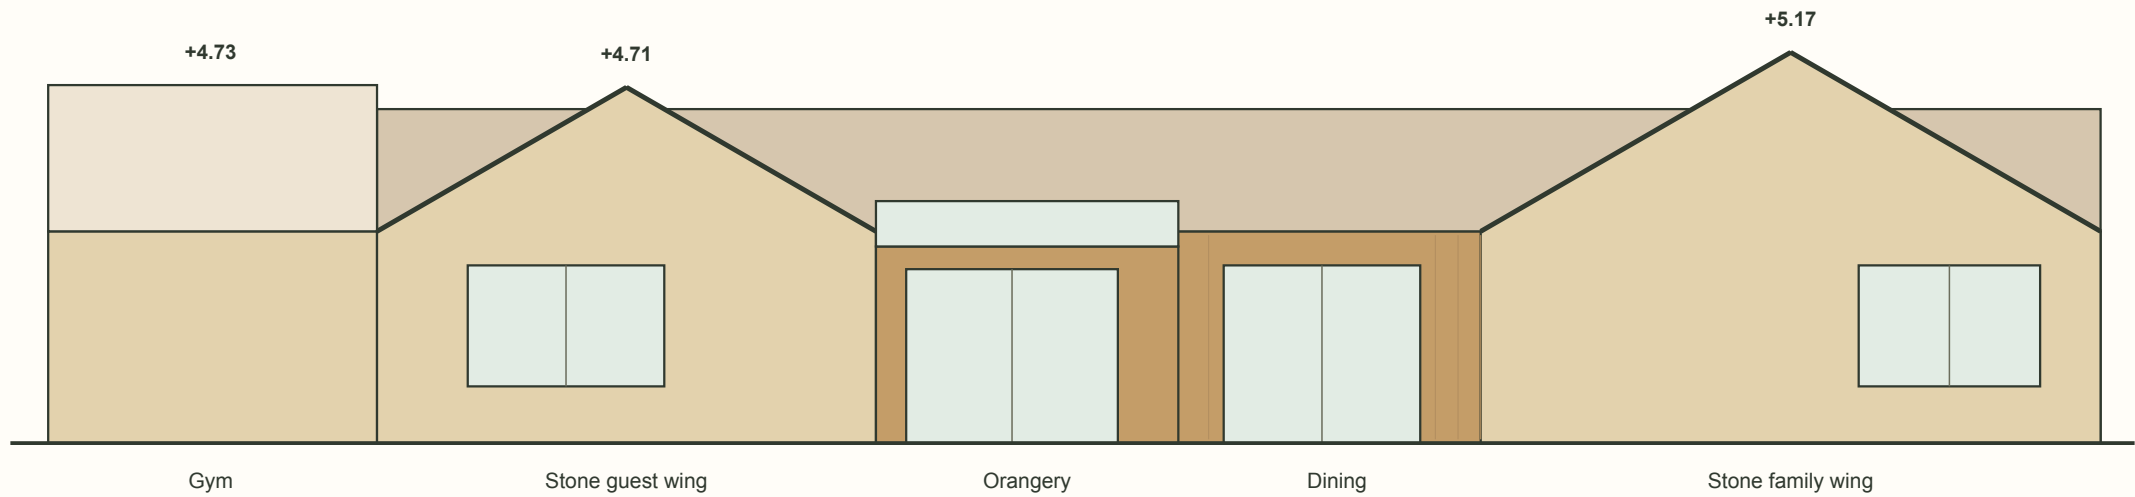


A RECESSED CENTRE

The stone gables frame the view. Dining sits at the back of the U; the lounge remains behind the family wing, as in arrangement A.

Orthographic view: depth is not visible here. Use the roof plan to read the courtyard setback.

02 / FROM THE ARRIVAL SIDE, LOOKING TOWARD THE GARDEN

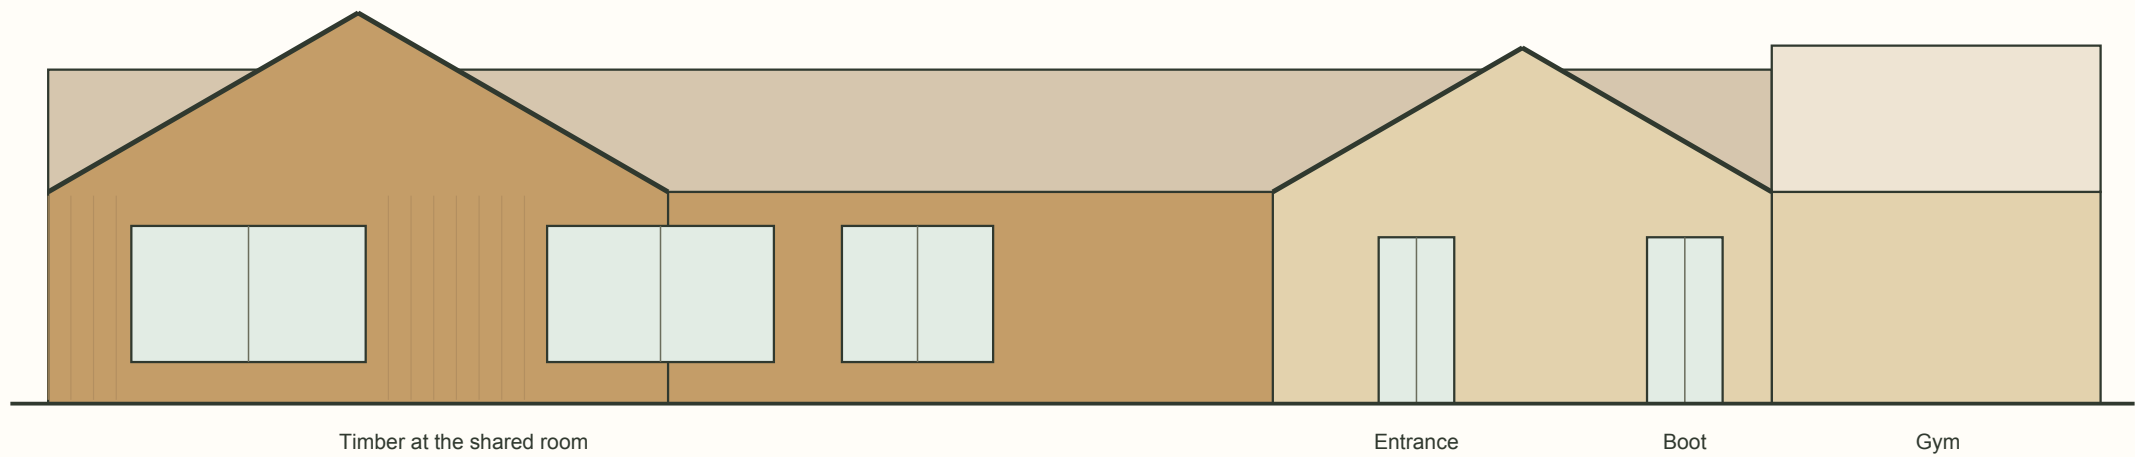

THE EVERYDAY FRONT

Timber follows the shared-room wall, including its lounge end. Stone continues around the entrance / service wing and gym.

Entrance and boot doors keep their measured positions. Canopies, steps and carport are outside this first study.

READING THESE ELEVATIONS


Warm buff stone, honey timber and a warm muted roof tone express the materials brief. Roof colour is a placeholder. Covering, pitch suitability, eaves, gutters and timber weathering remain open. Window heads: +2.35 m. Garden bedroom sills: +0.75 m; arrival shared-room sills: +0.55 m. The stove / flue and proposed rooflights are deferred until roof junctions and internal positions are agreed.



The ceiling needs its own design

Two located sections 1:100 at A3 | Vertical roof profiles derive from the same geometry as sheet 1

B-B / ACROSS LOUNGE, DINING, KITCHEN, LAUNDRY AND GYM

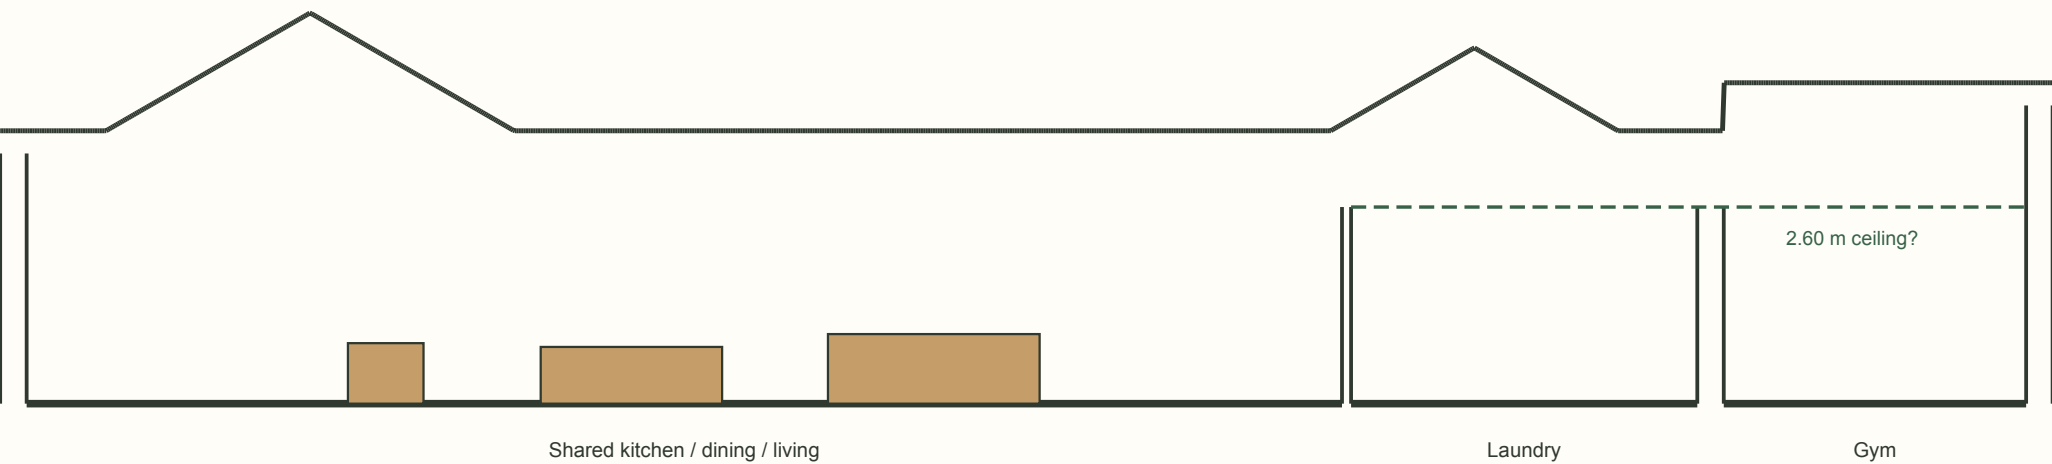


A CHANGE ABOVE THE SOFA

The family-wing roof continues over the lounge end. A fully open ceiling would change direction between lounge and dining.

Test a deliberate ceiling transition or a revised roof junction before assuming one uninterrupted vault.

Furniture is shown beyond the cut. Gym height needs equipment checks.

A-A / THROUGH THE COURTYARD AND SHARED ROOM AT x = 9.50 m

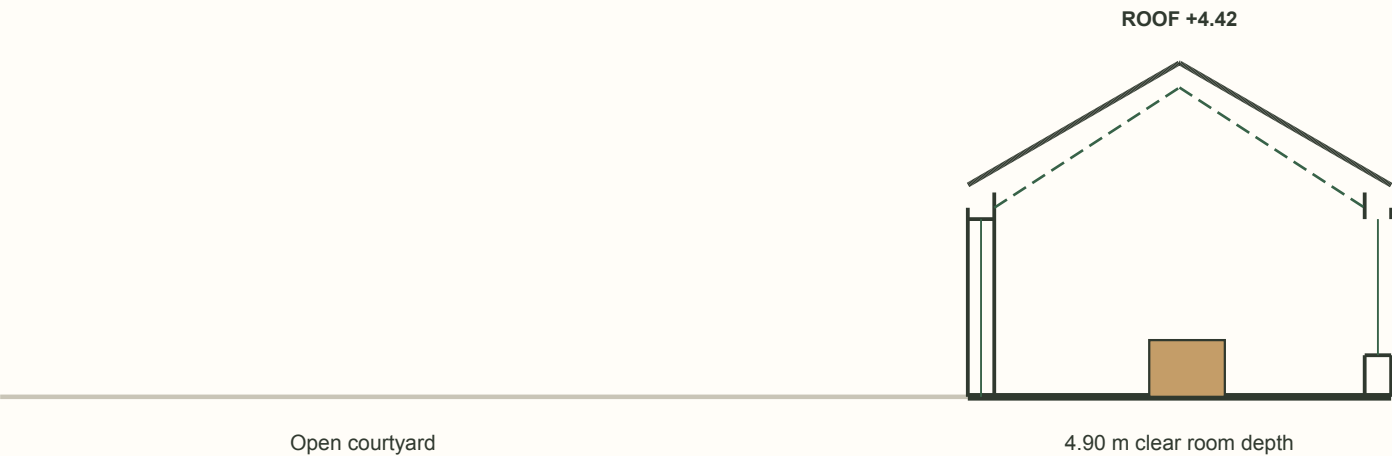

HEIGHTS TO TEST, NOT TARGETS TO FREEZE

The main roof datum is +2.80 m at the external wall face. A 2.60 m flat ceiling is tested in laundry and gym. The dashed pitched ceiling indicates the shared-room intent; its exact underside depends on structure and insulation. No beam, truss, roof thickness or clear apex height is specified.

THE NEXT TWO DECISIONS

1. Should the lounge join the dining vault, or have a calmer separate ceiling beneath the intersecting family roof?
2. Is the orangery seasonal or a year-round heated room? Its low roof and three-way junction need that brief.

Checked: source outline and window widths retained; ridge calculations, roof coverage and section samples agree.
Unresolved: structural support, roof steps/abutments, rainwater outlets, insulation, acoustics, daylight and stove/flue.
This study exposes those interfaces; it does not establish technical compliance or suitability for a particular site.