


Let the shared room lead

Roof arrangement 1:100 at A3, printed at 100% | Low-roof outlines show envelope tops, not drainage surfaces

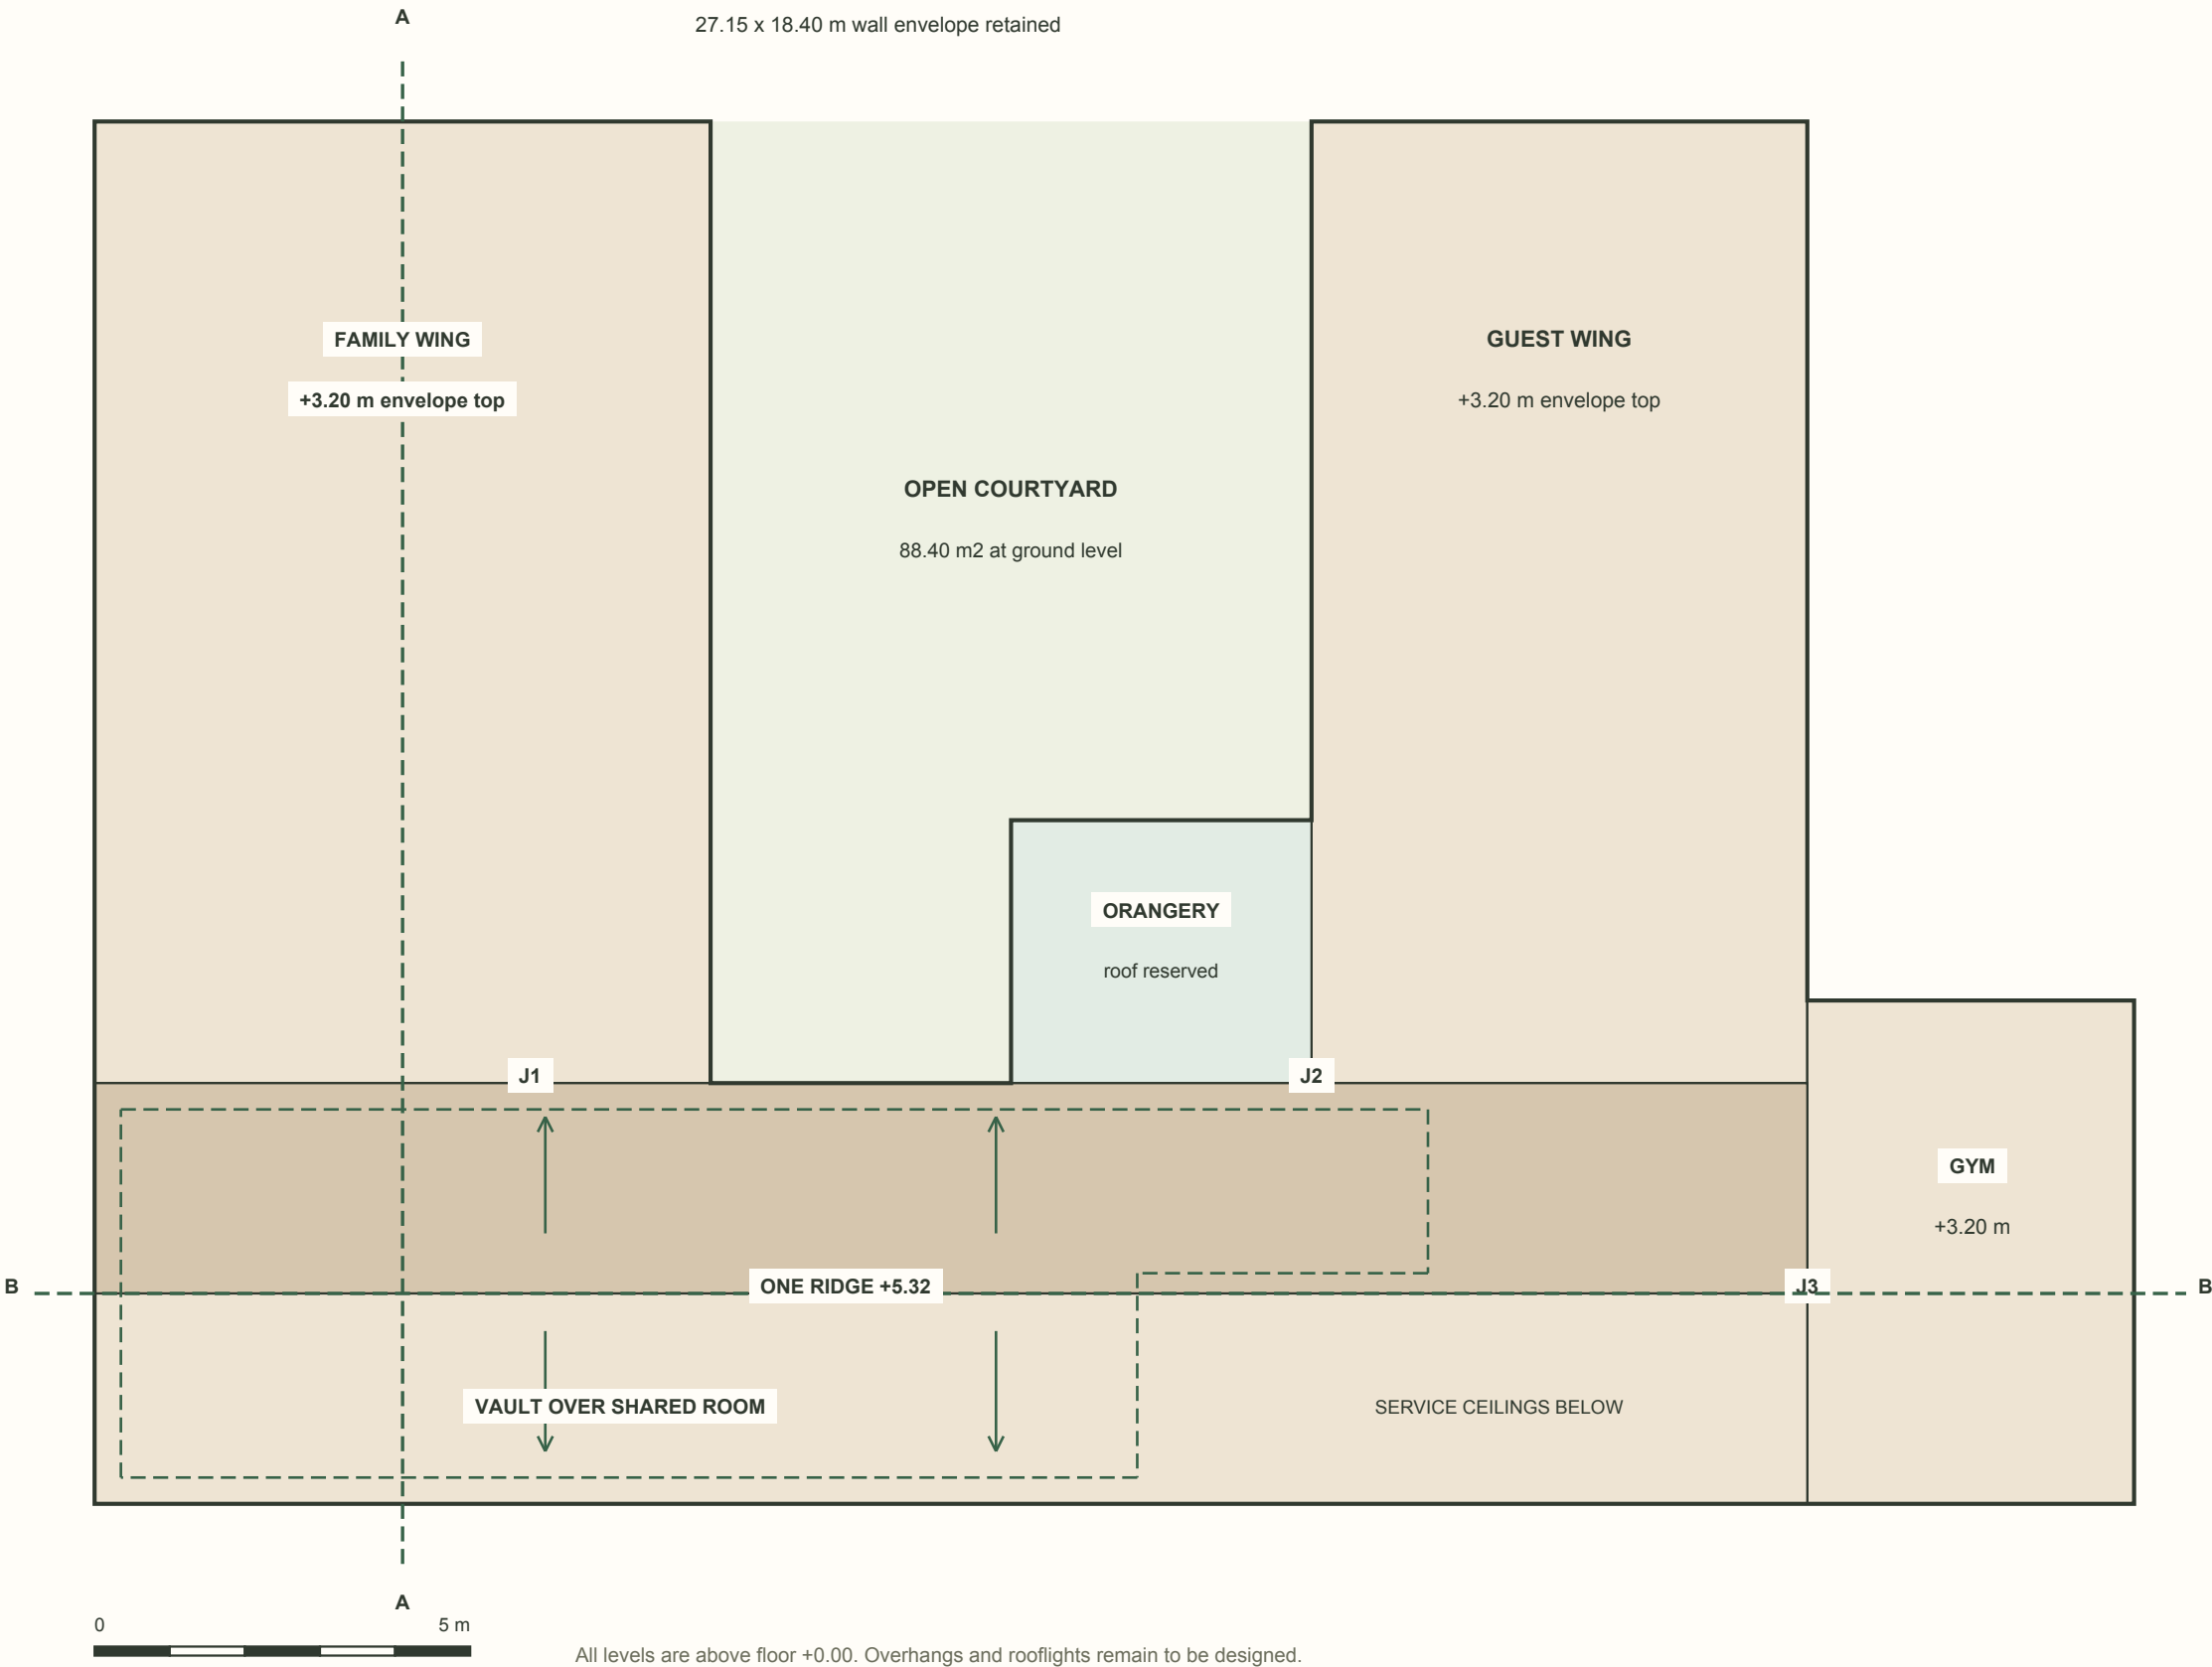

THE DESIGN MOVE

The pitched roof runs across the whole rear block, including the lounge and enclosed service rooms. The two projecting wings stop beneath its courtyard-side eave.

A HEIGHT TEST

Main roof edge: +3.70 m.
Main ridge: +5.32 m at 30 degrees.
Lower roof envelope tops: +3.20 m.

The 0.50 m gross level difference is before fascia, gutter and flashing design. It is not a verified clearance.

WHAT THE LINES MEAN

Dashed green: shared-room outline below the roof; no new room walls.
Low roofs reserve a zone for falls, insulation, drainage and edge detail.
No low-roof drainage falls or outlet positions are fixed here.

CONNECTIONS TO DEVELOP


J1 Low family roof / main eave.
J2 Guest and orangery connections.
J3 Gym roof / main gable wall.

Orangery top shown at +3.20 m for massing only. Glazing and seasonal / year-round use stay open.

A taller centre, quieter wings

Elevations 1:100 at A3 | Window and door widths retained; shared glazing heads raised to +2.70 m as a proposal

FROM THE GARDEN / GYM ON THE LEFT

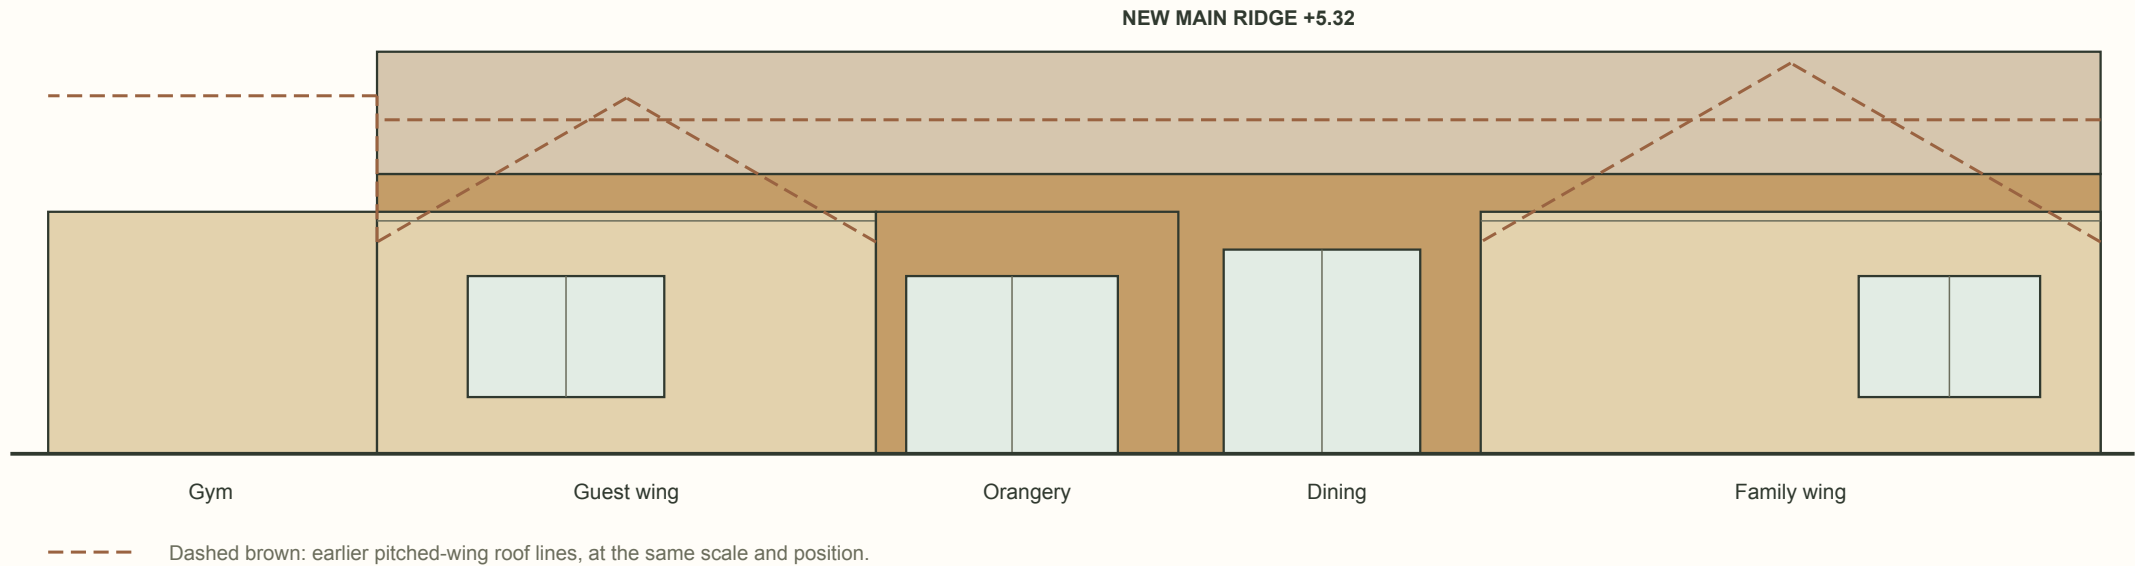


WHAT CHANGES

Wing gables disappear, leaving lower stone volumes in front of one continuous timber roof.

- Family top: 5.17 to 3.20 m.
- Guest top: 4.71 to 3.20 m.
- Gym top: 4.73 to 3.20 m.
- Main ridge: 4.42 to 5.32 m.
- Overall highest: 5.17 to 5.32 m.

FROM THE ARRIVAL SIDE / GYM ON THE RIGHT

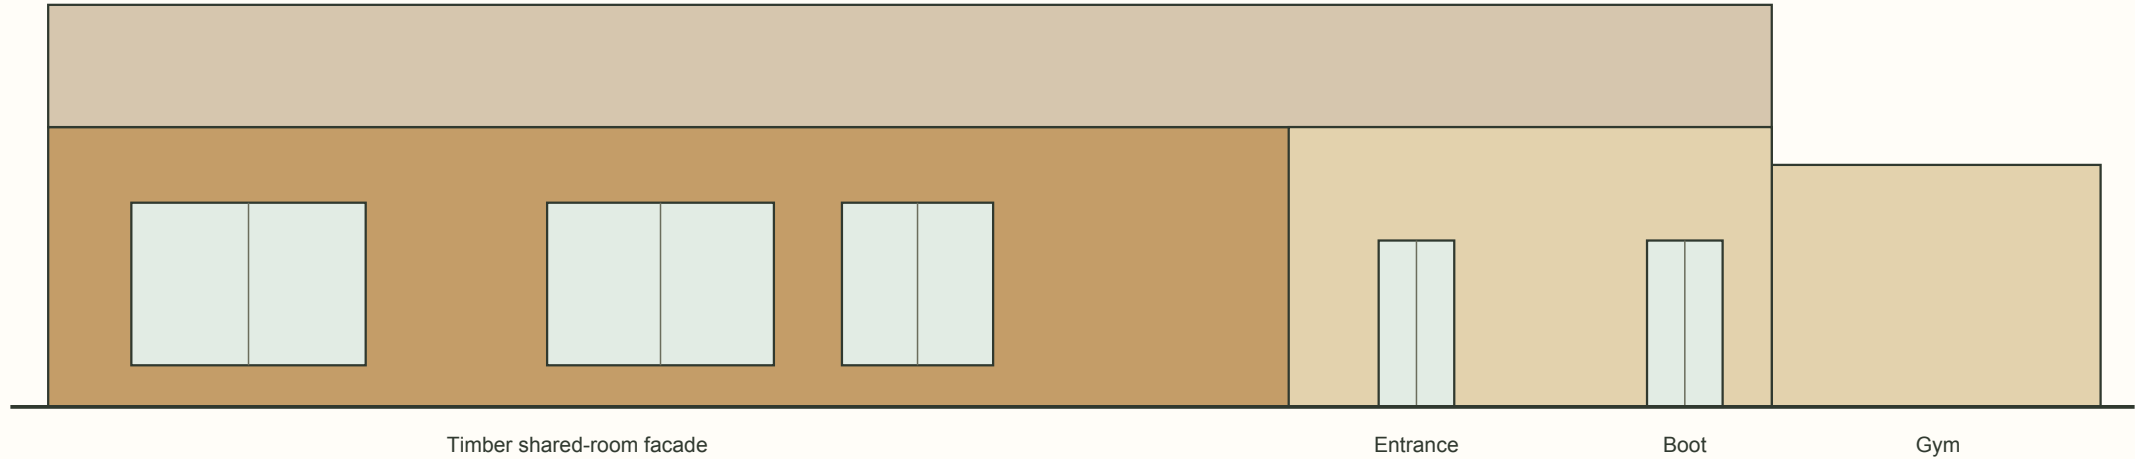

THE TRADEOFF

The rear pitched volume becomes more prominent. Its taller eaves reserve room to investigate the lower-roof connections.

This is a height study, not the minimum workable roof height. Roof-covering colours are placeholders.

The family and guest wings retain their positions and warm stone character. Main arrival wall: timber, with stone at services. These orthographic views compress depth. The courtyard plan on sheet 1 shows which volumes sit forward. Roof-edge details, window proportions, shade and daylight need refinement once the overall heights feel right. The orangery is shown as a low enclosure only; its roof system has not been selected.



One ceiling from sofa to kitchen

Located sections 1:100 at A3 | The pitched ceiling is continuous over the shared-room footprint

B-B / ALONG THE RIDGE, LOOKING TOWARD THE GARDEN




THE INTERIOR RESULT

The lounge no longer inherits a crossing bedroom-wing roof. One ridge runs over the sofa, dining table and kitchen.

Pantry, hall and boot room have flat ceilings under the same roof. Furniture beyond the cut is shown for context. No supports are designed.

A-A / THROUGH THE FAMILY WING AND LOUNGE, LOOKING TOWARD THE GYM

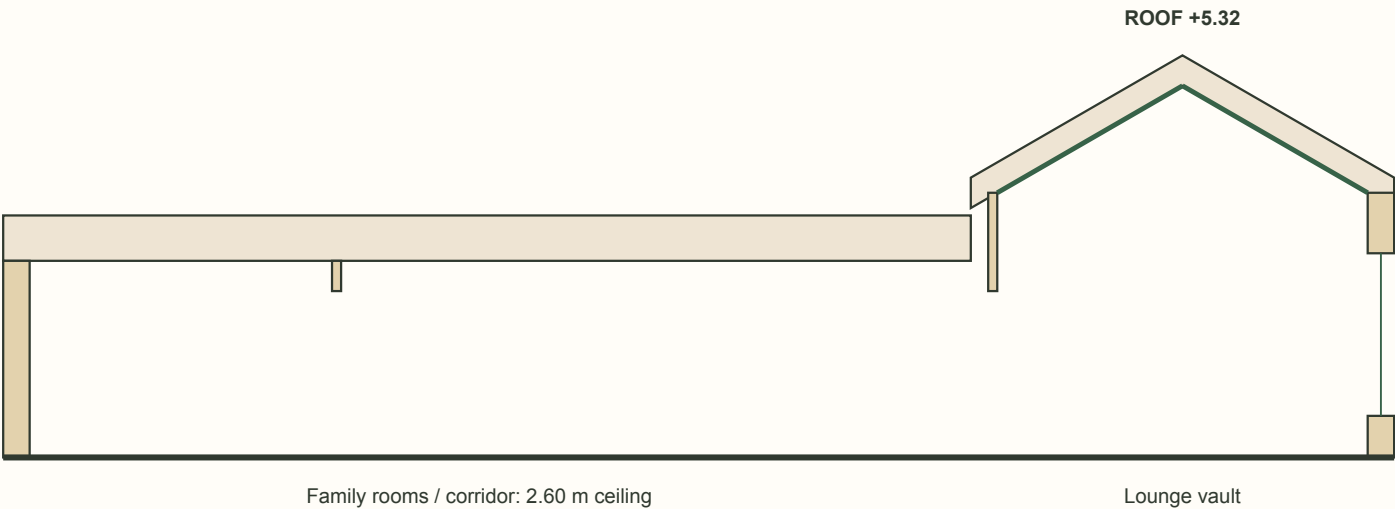

WORKING INTERNAL HEIGHTS

Shared ceiling: 3.50 m at the internal side walls, rising to 4.91 m. Wing / service ceilings: 2.60 m. Gym ceiling: 2.70 m for testing. Shaded roof bands are space reservations, not build-up details. The main roof edge is 0.50 m above the lower roof envelope; fascia, overhang and weatherproof connections still need fitting.

WHAT TO JUDGE NEXT

Does the shared room feel too tall, or comfortably generous? If the form is right, refine roof depth and junctions to see whether the main eaves can come down while retaining the continuous vault. Confirm gym equipment height and the orangery use separately.

Checked: unchanged floor geometry; full roof coverage; continuous shared vault; garden/arrival orientation; all three pages rendered.
Unresolved: structure, roof build-ups, low-roof falls/outlets, rooflights, thermal design, stove/flue and site-specific daylight.