

A garden room at the heart of the U

1:100 at A3, printed at 100% | Metres | 350 mm external walls and 120 mm internal partitions assumed



319.9 m2 GIA

360.3 m2 external footprint

The agreed additions

Orangery: 4.00 x 3.50 m footprint;
3.65 x 3.15 m / 11.5 m2 inside.
Hall and living connections;
direct hall/living route retained.

Gym: 4.00 x 6.00 m clear,
entered through the boot room.
Rack/cables, bench, dumbbells
and treadmill shown indicatively.

Pantry beside fridge and counter.
Smaller hall; wider laundry.
Visitor WC off the guest hall.

Courtyard and roof


88.4 m2 remains open to the sky.
4 m separates the orangery
from the bedroom wing.
Direct living/courtyard doors
remain beside the orangery.

Dashed teal: rooflight proposals
for orangery and laundry.
Heating, shading and ventilation
are not yet specified.

Furniture and nominated routes
checked; equipment-specific
clearances still need confirmation.

Space accounted for

Family detail at 1:60 on A3 | Net room areas include fitted furniture; GIA includes partitions

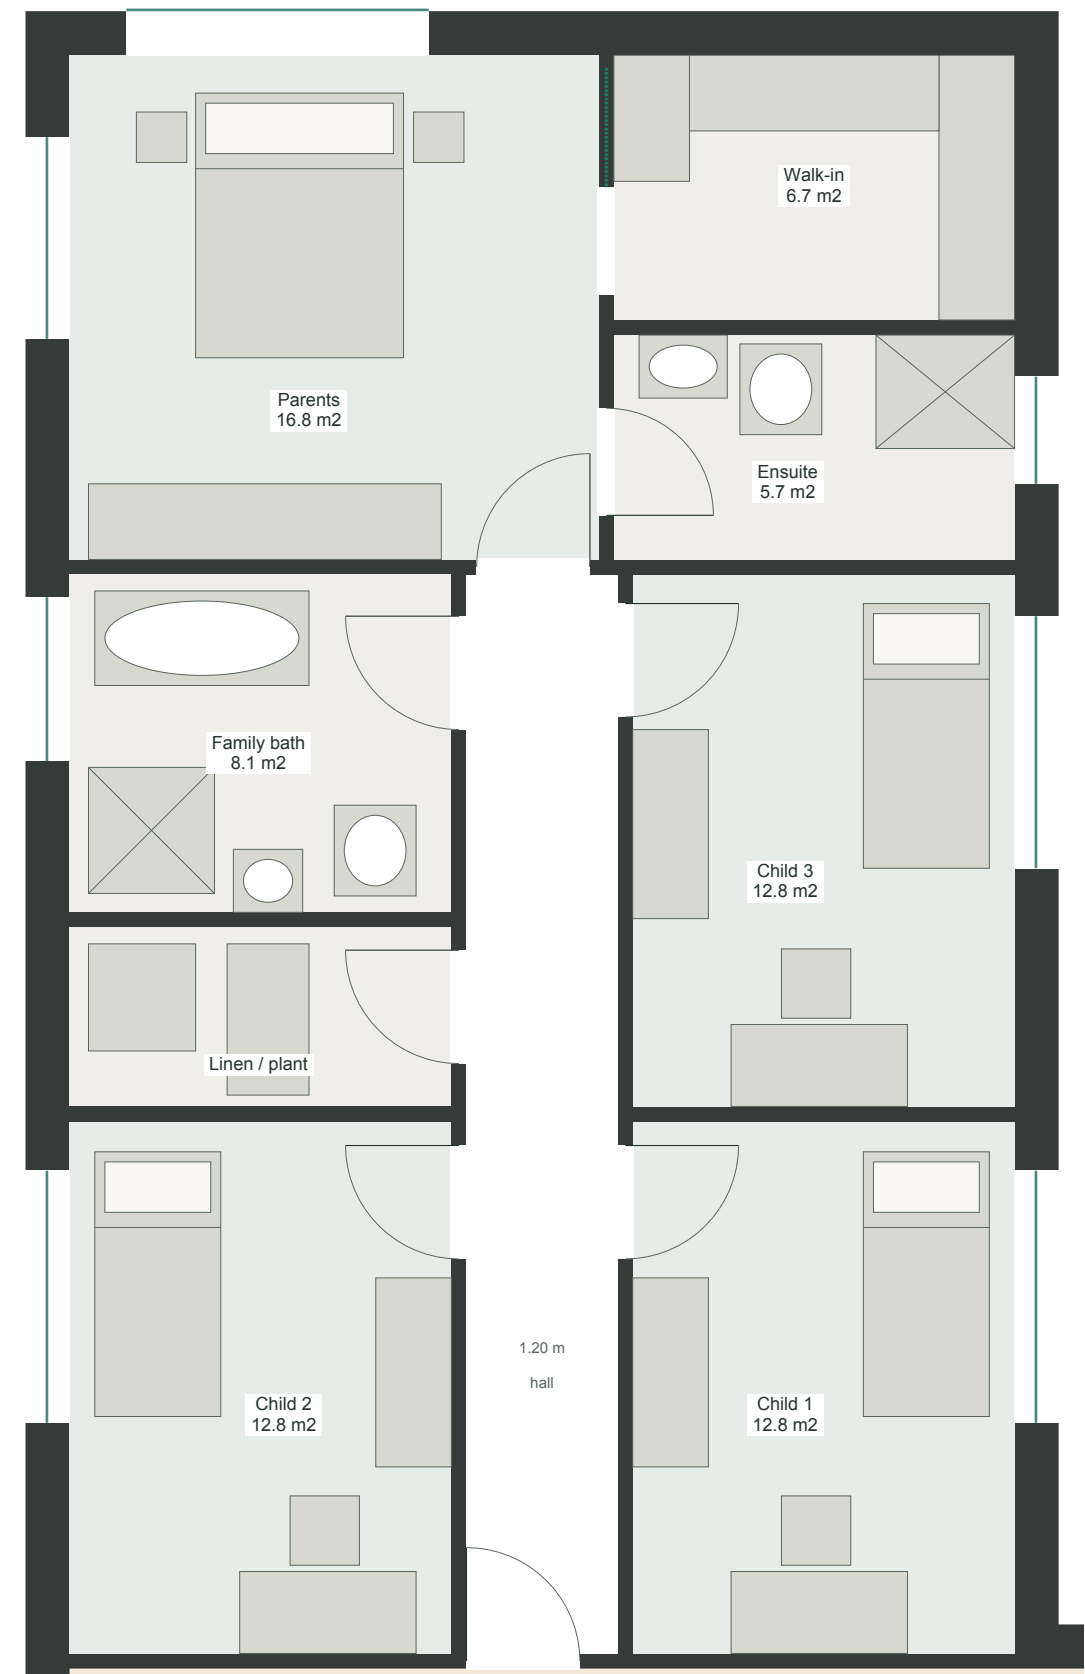


Family grouping retained from concept 04

ROOM	CLEAR SIZE (m)	m2
Shared living	4.90 deep / stepped	74.73
Parents bedroom	4.20 x 4.00	16.80
Walk-in wardrobe	3.18 x 2.10	6.68
Parents ensuite	3.18 x 1.78	5.66
Children: 3 rooms	Each 3.03 x 4.22 / 12.79 m2	38.36
Family bathroom	3.03 x 2.68	8.12
Guest bedroom	4.58 x 3.30 + wardrobe recess	17.12
Guest shower	2.10 x 2.40	5.04
Office / gaming	4.58 x 3.05	13.97
Snug	4.58 x 2.60	11.91
Corner orangery	3.65 x 3.15	11.50
Indoor gym	4.00 x 6.00	24.00
Pantry	2.35 x 2.60	6.11
Boot room	3.30 x 2.60	8.58
Laundry	L-shape; 4.58 x 3.15 envelope	10.86
Visitor WC	2.23 x 1.40	3.12
Linen / plant / guest storage	Two storage zones	6.54
Entrance hall	2.56 x 2.60	6.66
Other circulation	1.20-wide halls + shower lobby	26.80
Partitions + doorway thresholds		17.35
TOTAL GIA		319.91

Concept 04: 279.81 m2 GIA. This revision adds 40.10 m2.
Gym: 24.00 m2 clear plus 2.10 m2 of retained dividing wall.
Orangery: 11.50 m2 clear plus 2.50 m2 of wall / thresholds.
Open living remains 74.73 m2; hall reduces to 6.66 m2.
A 0.90 m pantry shift recovers 2.34 m2 of kitchen area compared with the preceding exploratory pantry option.

Making the connections work

Enlarged corner at 1:60 on A3 | Teal routes are checked with a sampled 0.70 m walking envelope

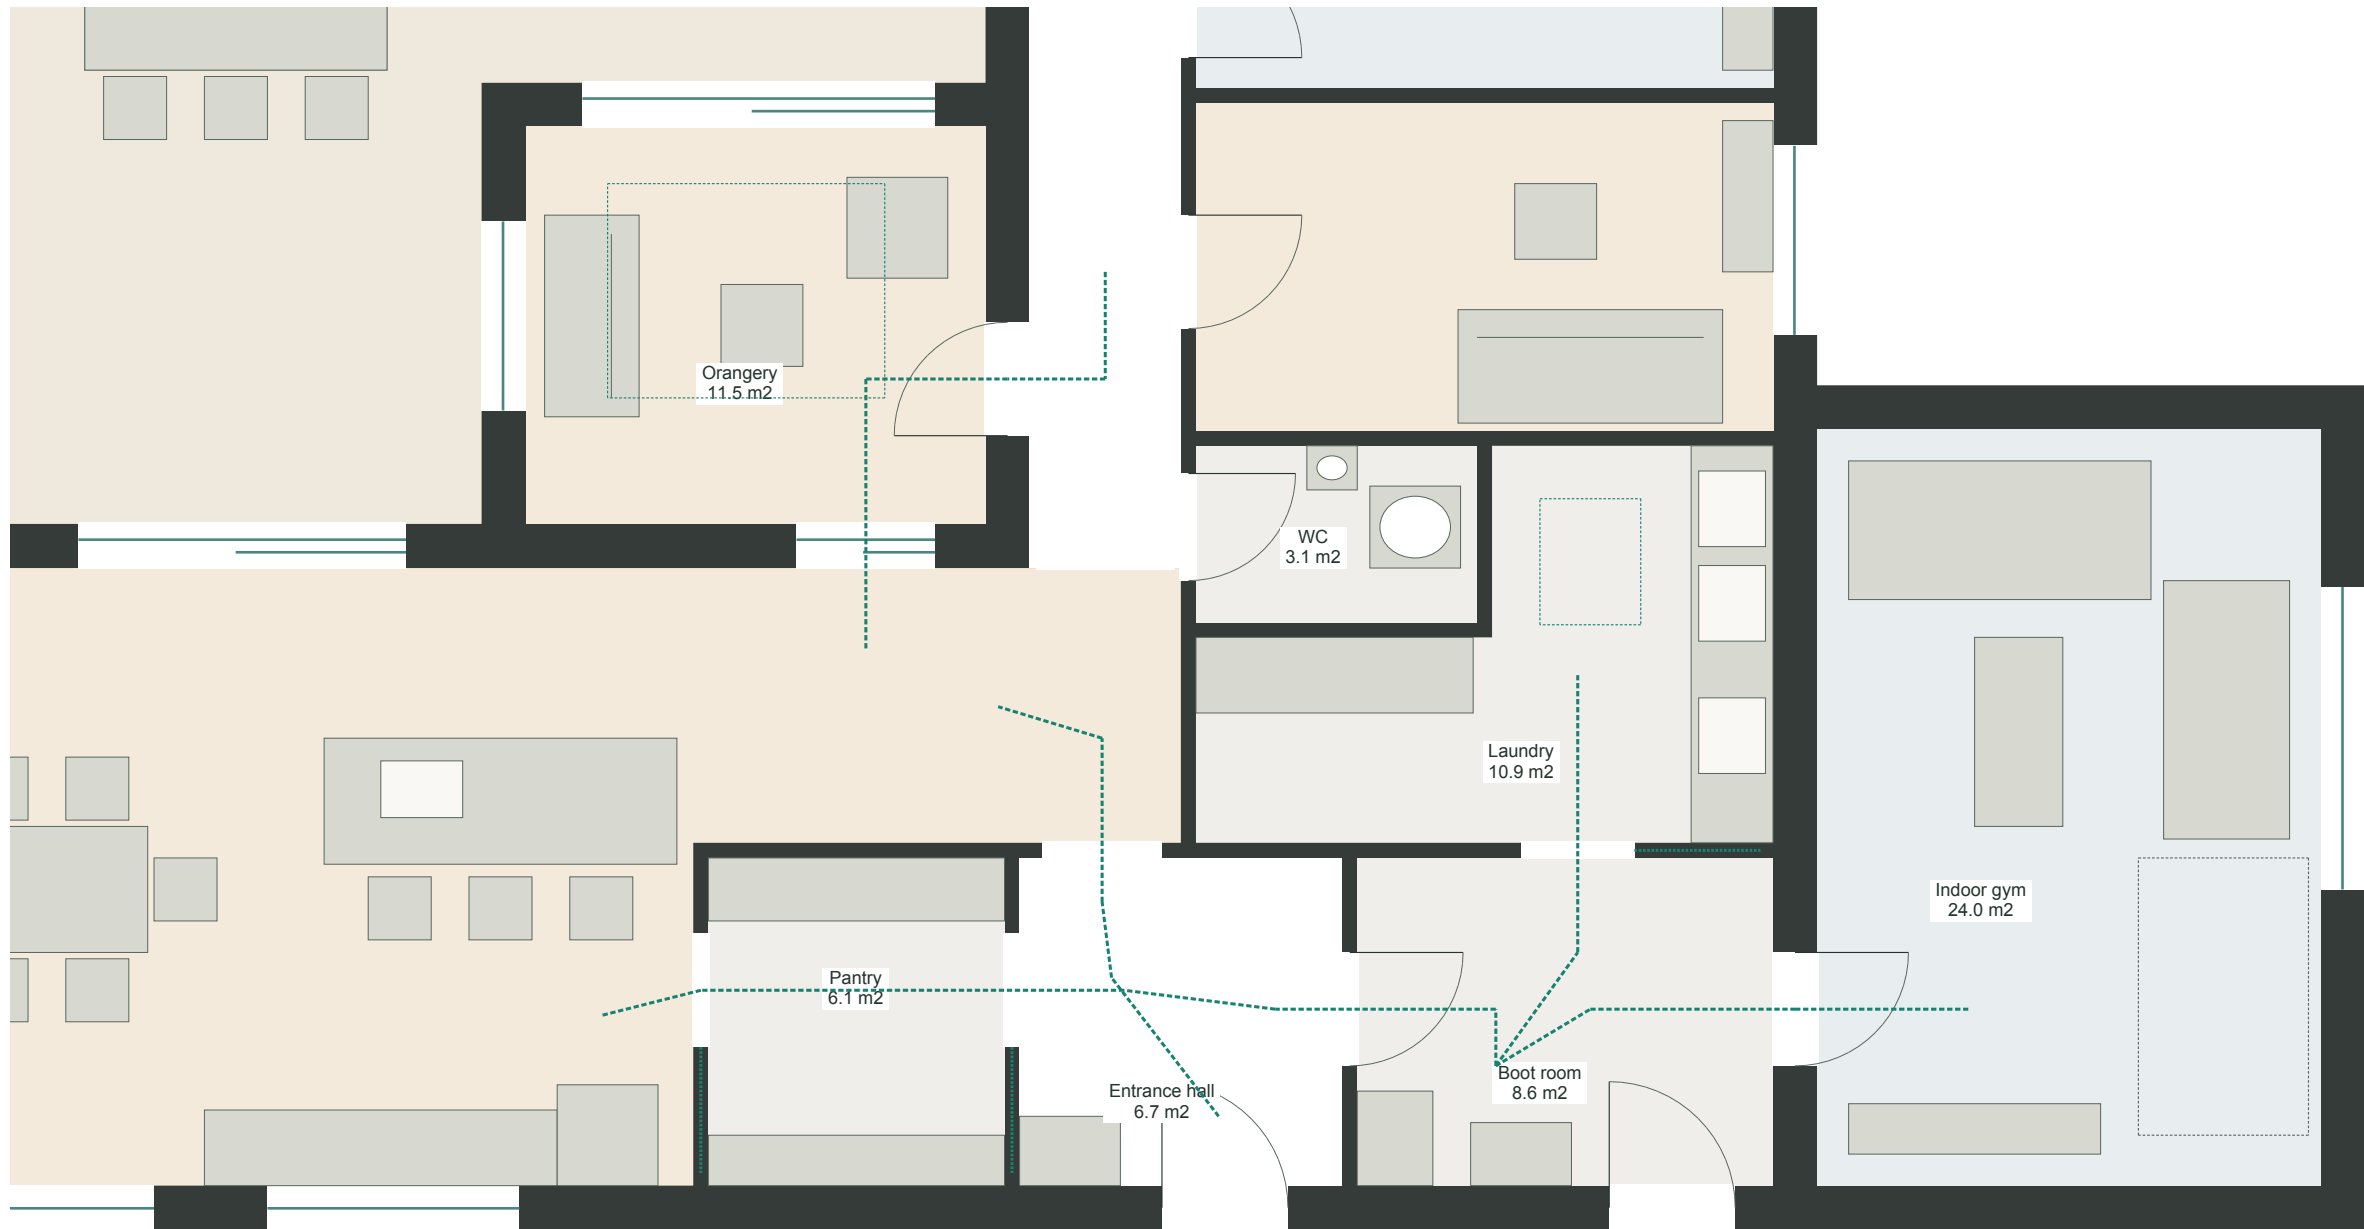

Everyday connections

- Boot room > hall > pantry > kitchen; direct hall/kitchen access remains.
- Orangery doors meet along its clear south/east edge, beside the seating.
- The smaller hall retains coat storage and access to boot room / kitchen.
- Laundry gains a folding counter; its daylight is now via a rooflight.
- Pantry and laundry pocket doors require clear wall cavities.

Gym and design limits

- Combined rack/cable unit and equipment are illustrative footprints.
- Dashed grey zone: 1.35 x 2.20 m treadmill rear allowance.
- Check the chosen machines, barbell handling, height and anchoring.
- Acoustics, structures, drainage, rooflight/shading design and building compliance require detailed work; these are concept checks.

The wider house on the same test plot

1:200 at A3, printed at 100% | Hypothetical 35 x 45 m plot | Orientation and boundary clearances unassigned



1,575 m2 illustrative plot

Approximately 0.39 acres

House including gym and orangery: 360.3 m2 external footprint.

Open courtyard: 88.4 m2; approximately 38 m2 paved.

Orangery allocation: 14 m2 within the original courtyard.

Gym is inside the house; the detached studio is removed.

Carport: 42.2 m2 clear; provisional roof envelope 47.5 m2.

Guest bay: 3.2 x 6.0 m, independent of the carport.

Arrival and boundary assumptions

The gym leaves 4.55 m to the right test boundary.

A 1.4 m strip separates the house and parking allocations.

Cars shown as 2.0 x 4.9 m bodies, excluding mirrors.

The 6 m manoeuvring apron remains clear of structures.

Chosen vehicles require a proper swept-path check.

Carport columns sit outside its clear parking allocation.

Before choosing a plot

Test orientation, winter sunlight, privacy and overheating.

Check access rights, local planning, drainage and services.

Allow for topography, trees and boundary constraints.

This rectangle demonstrates a fit; it is not a minimum plot size or evidence that a particular site is buildable.

Area convention

GIA is measured to the internal faces of external walls.

Gym and orangery are included, with internal partitions.

Room areas include fitted joinery footprints; carport and remaining open courtyard are additional.