

A comfortable home, made measurable

1:100 at A3, printed at 100% | Metres throughout | Proposed 350 mm external walls and 120 mm partitions



279.8 m2 GIA

317.1 m2 external footprint | 280 m2 target

ROOM	CLEAR SIZE (m)	m2	TARGET
Shared living	4.90 deep / stepped	75.5	72
Parents bedroom	4.20 x 4.00	16.8	16
Walk-in wardrobe	3.18 x 2.10	6.7	7
Parents ensuite	3.18 x 1.78	5.7	6
Children: 3 rooms	3.03 x 4.22	38.4	39
Family bathroom	3.03 x 2.68	8.1	8
Guest bedroom	4.58 x 3.30 + recess	17.1	15
Guest shower	2.10 x 2.40	5.0	5
Office / gaming	4.58 x 3.05	14.0	14
Snug	4.58 x 2.60	11.9	12
Pantry	2.23 x 3.15	7.0	7
Boot room	3.30 x 2.60	8.6	8
Laundry	2.23 x 3.15	7.0	7
Visitor WC	1.52 x 2.02	3.1	3
Linen / plant / guest storage	Two storage zones	6.5	7
Entrance hall	3.46 x 2.60	9.0	9
Other circulation	1.20-wide halls	26.8	24
Partitions + doorway thresholds		12.6	21

What changed from the schedule

Open living: 75.5 m2, against 72 m2.

Children: 12.8 m2 each; 3.03 x 4.22 m.

Guest room gains a wardrobe recess.

Circulation is a little above its allowance.

Courtyard is longer; only part is paved.



Pocket doors shown in teal; reserve their cavities.

Furniture is drawn to scale. Detail checks on sheet 2.

Final wall build-ups may change the area balance.

Testing the places where space matters

Enlarged details at 1:60 on A3 | Hinged bedrooms and office; selected internal pocket doors

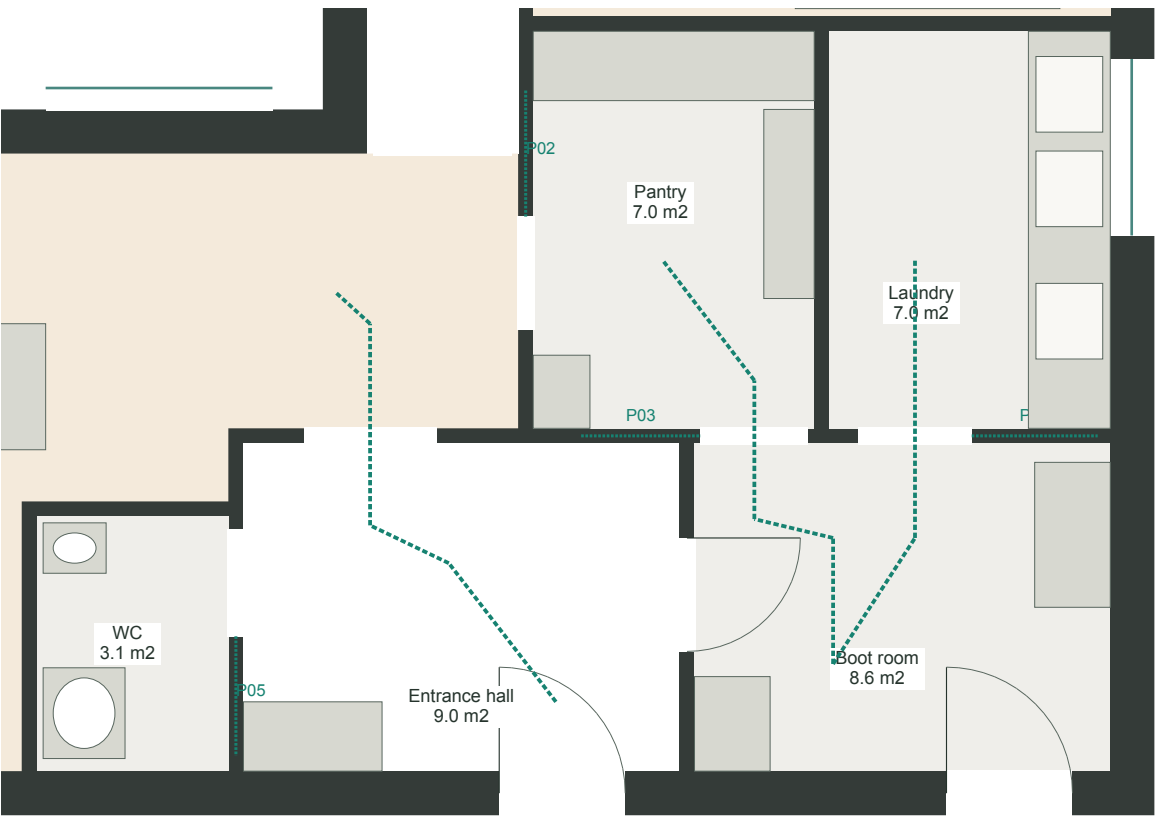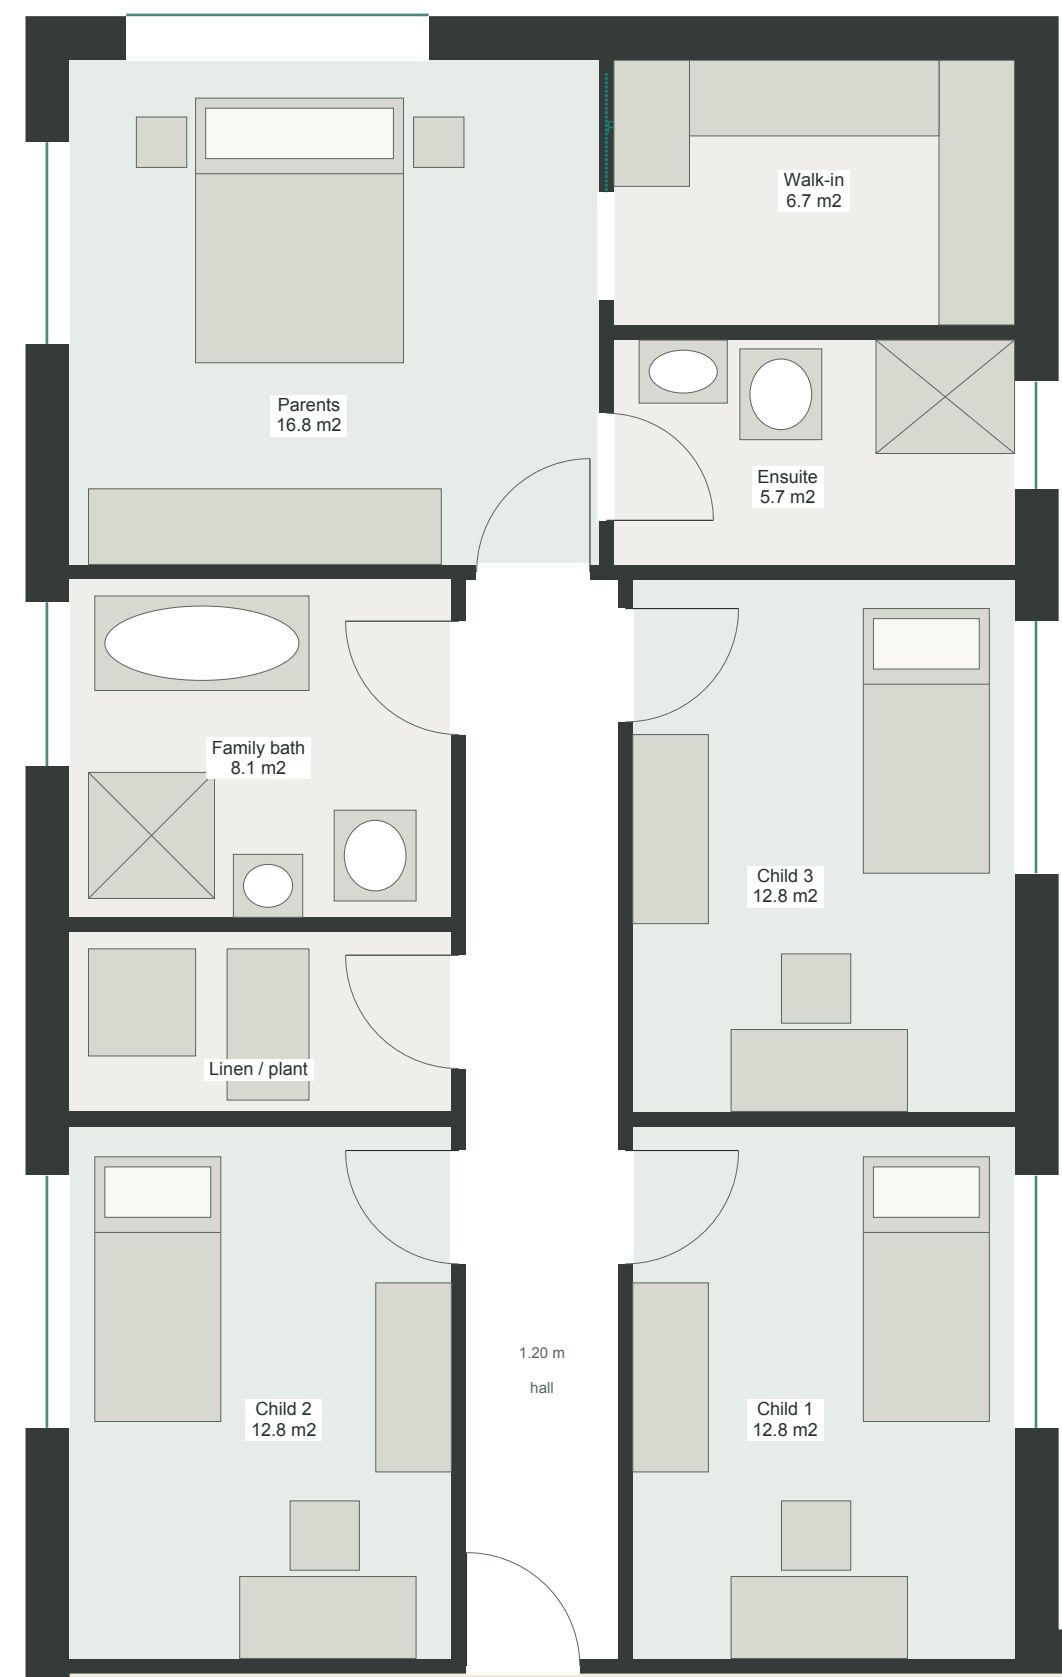

Direct hall / kitchen route; pantry is optional on arrival

Measured furniture and circulation checks

- Family and guest corridors: 1.20 m clear between finishes.
- Children: 1.00 x 2.10 m beds, 1.40 m desks, 0.60 m wardrobes.
- Parents: 1.65 x 2.10 m bed frame; 1.00 m at the foot to storage.
- Kitchen: 2.80 x 1.00 m island; 1.35 m aisle on courtyard side.
- Dining: 2.40 x 1.00 m table, eight chairs; 1.30 m behind front chairs.
- Laundry: 0.65 m appliance counter leaves 1.58 m working width.
- Door openings: 0.85-1.05 m proposed; final clear widths depend on frames.
- Pocket reservations: walk-in, pantry/kitchen, pantry/boot, laundry/boot, WC.
- Pocket cavities remain clear of plumbing; final kits need detailed sizing.

Limits of this check

Room polygons, furniture, door sweeps and a 0.70 m envelope on the five nominated routes are checked. This is not a regulatory, structural, acoustic, accessibility or vehicle swept-path certification. Roof spans, services and solar orientation remain site-dependent.

What the house asks of a site

1:200 at A3, printed at 100% | Hypothetical 35 x 45 m plot | Orientation and boundary clearances unassigned



1,575 m2 illustrative plot

Approximately 0.39 acres

House: 317.1 m2 external footprint.

Courtyard recess: 102.4 m2; paved terrace approx. 52 m2.

Carport: 42.2 m2 clear; provisional roof envelope 47.5 m2.

Guest bay: 3.2 x 6.0 m, independent of the carport.

Detached exercise studio: 24 m2 external envelope.

Short pedestrian route to boot room and entrance hall.

Arrival assumptions

Cars shown as 2.0 x 4.9 m bodies, excluding mirrors.
The 6 m apron is kept clear of planters and structures.
Final turning movements require the chosen vehicles and a proper swept-path check; this reserves space only.
Columns are outside the 6.8 x 6.2 m clear parking area.
Solar supports and roof sizing require engineering.

Before choosing a plot

Test orientation, winter sunlight and overheating.
Check access rights, local planning, drainage and services.
Allow for topography, trees and boundary constraints.
This rectangle demonstrates a fit; it is not a minimum plot size or evidence that a particular site is buildable.

Area convention

GIA is measured to the internal faces of external walls.
It includes internal partitions and doorway thresholds.
Room areas include fitted joinery footprints; carport, courtyard and detached studio are additional.